

EtecProjekt+Bau GmbH

CE

Heinrich-Hertz-Straße 22a  
40699 Erkrath  
021121023300 info@etecprojekt.de

Projektname: SEGRO Park Düsseldorf Flingern  
Kom-Nr./Angebots-NR.: A2024-2543 Ausführungsplan  
Bezeichnung Ort: UV Allgemein Technik 4  
Auftragsnummer: AB2024-1049 Klemmenfabrikat:  
Baujahr: 11 / 2025 WAGO

Farbkennzeichnung der Leiter (in Anlehnung an VDE0113 Teil1):

|                         |            |
|-------------------------|------------|
| Außenleiter:            | schwarz    |
| Neutralleiter:          | hellblau   |
| Steuerspannung 230V AC: | rot        |
| Steuerspannung 24V DC:  | dunkelblau |
| Steuerspannung 24V AC:  | braun      |
| Fremdspannung:          | orange     |
| Messung:                | weiss      |
| Sensorleitung:          | violett    |

Technische Daten der Schaltgerätekombination:


|                                                                 |                 |                       |                  |
|-----------------------------------------------------------------|-----------------|-----------------------|------------------|
| Bemessungsbetriebsspannung / -Frequenz:                         | Un: 400V / 50Hz | Netzform:             | TN-S             |
| Bemessungsstrom der Schaltgerätekombination:                    | InA: 63A        |                       |                  |
| Bemessungsstoßspannungsfestigkeit:                              | Uimp: 4kV       | Schutzklasse:         | 2 schutzisoliert |
| Bemessungsisolationsspannung:                                   | Ui: 230V        | Schutzart:            | IP44             |
| Bemessungsbelastungsfaktor:                                     | RDF: 0.6        | Schranks-tiefe:       | 161mm            |
| Bemessungsstoßstromfestigkeit:                                  | Ipk: 17kA       | Farbe:                | RAL7035          |
| Bemessungskurzzeitstromfestigkeit:                              | Icw: 3kA        | Umgebungs-temperatur: | 25°C             |
| Bedingte Bemessungskurzschlußstromfestigkeit:                   | Icc: kA         |                       |                  |
| (Ik3 nur bei Kurzschlußschutzeinrichtung (SCPD) in Einspeisung) |                 |                       |                  |
| Bemessungsschaltvermögen Leitungsschutzschalter:                | -               |                       |                  |


Installationsverteiler, nach DIN EN 61439-1/-3




Für dieses Dokument und den darin dargestellten Inhalt behalten wir uns alle Rechte vor. Die Vervielfältigung des Inhaltes ist ohne unsere ausdrückliche Zustimmung nicht gestattet. Hager Vertriebsgesellschaft mbH&Co.KG


|           |                |          |             |            |                                                    |   |                          |
|-----------|----------------|----------|-------------|------------|----------------------------------------------------|---|--------------------------|
| 3         |                |          | Angebotsnr. | A2024-2543 | Projektname:<br><br>SEGRO Park Düsseldorf Flingern | <br>EtecProjekt + Bau GmbH | Index: a                 |
| 2         |                |          | Datum       | 12.11.2025 |                                                    |   | = TECHNIKZENTRALEN       |
| 1         |                |          | Erstellt    |            |                                                    |   | + UV Allgemein Technik 4 |
| Änderung  | Änderungsdatum | Geändert | Bestätigt   |            | Deckblatt                                          |   |                          |
| Massstab: | Ik3: kA        | Ik1: kA  | TN-S        |            |                                                    |   | Blatt: 1 / 5             |

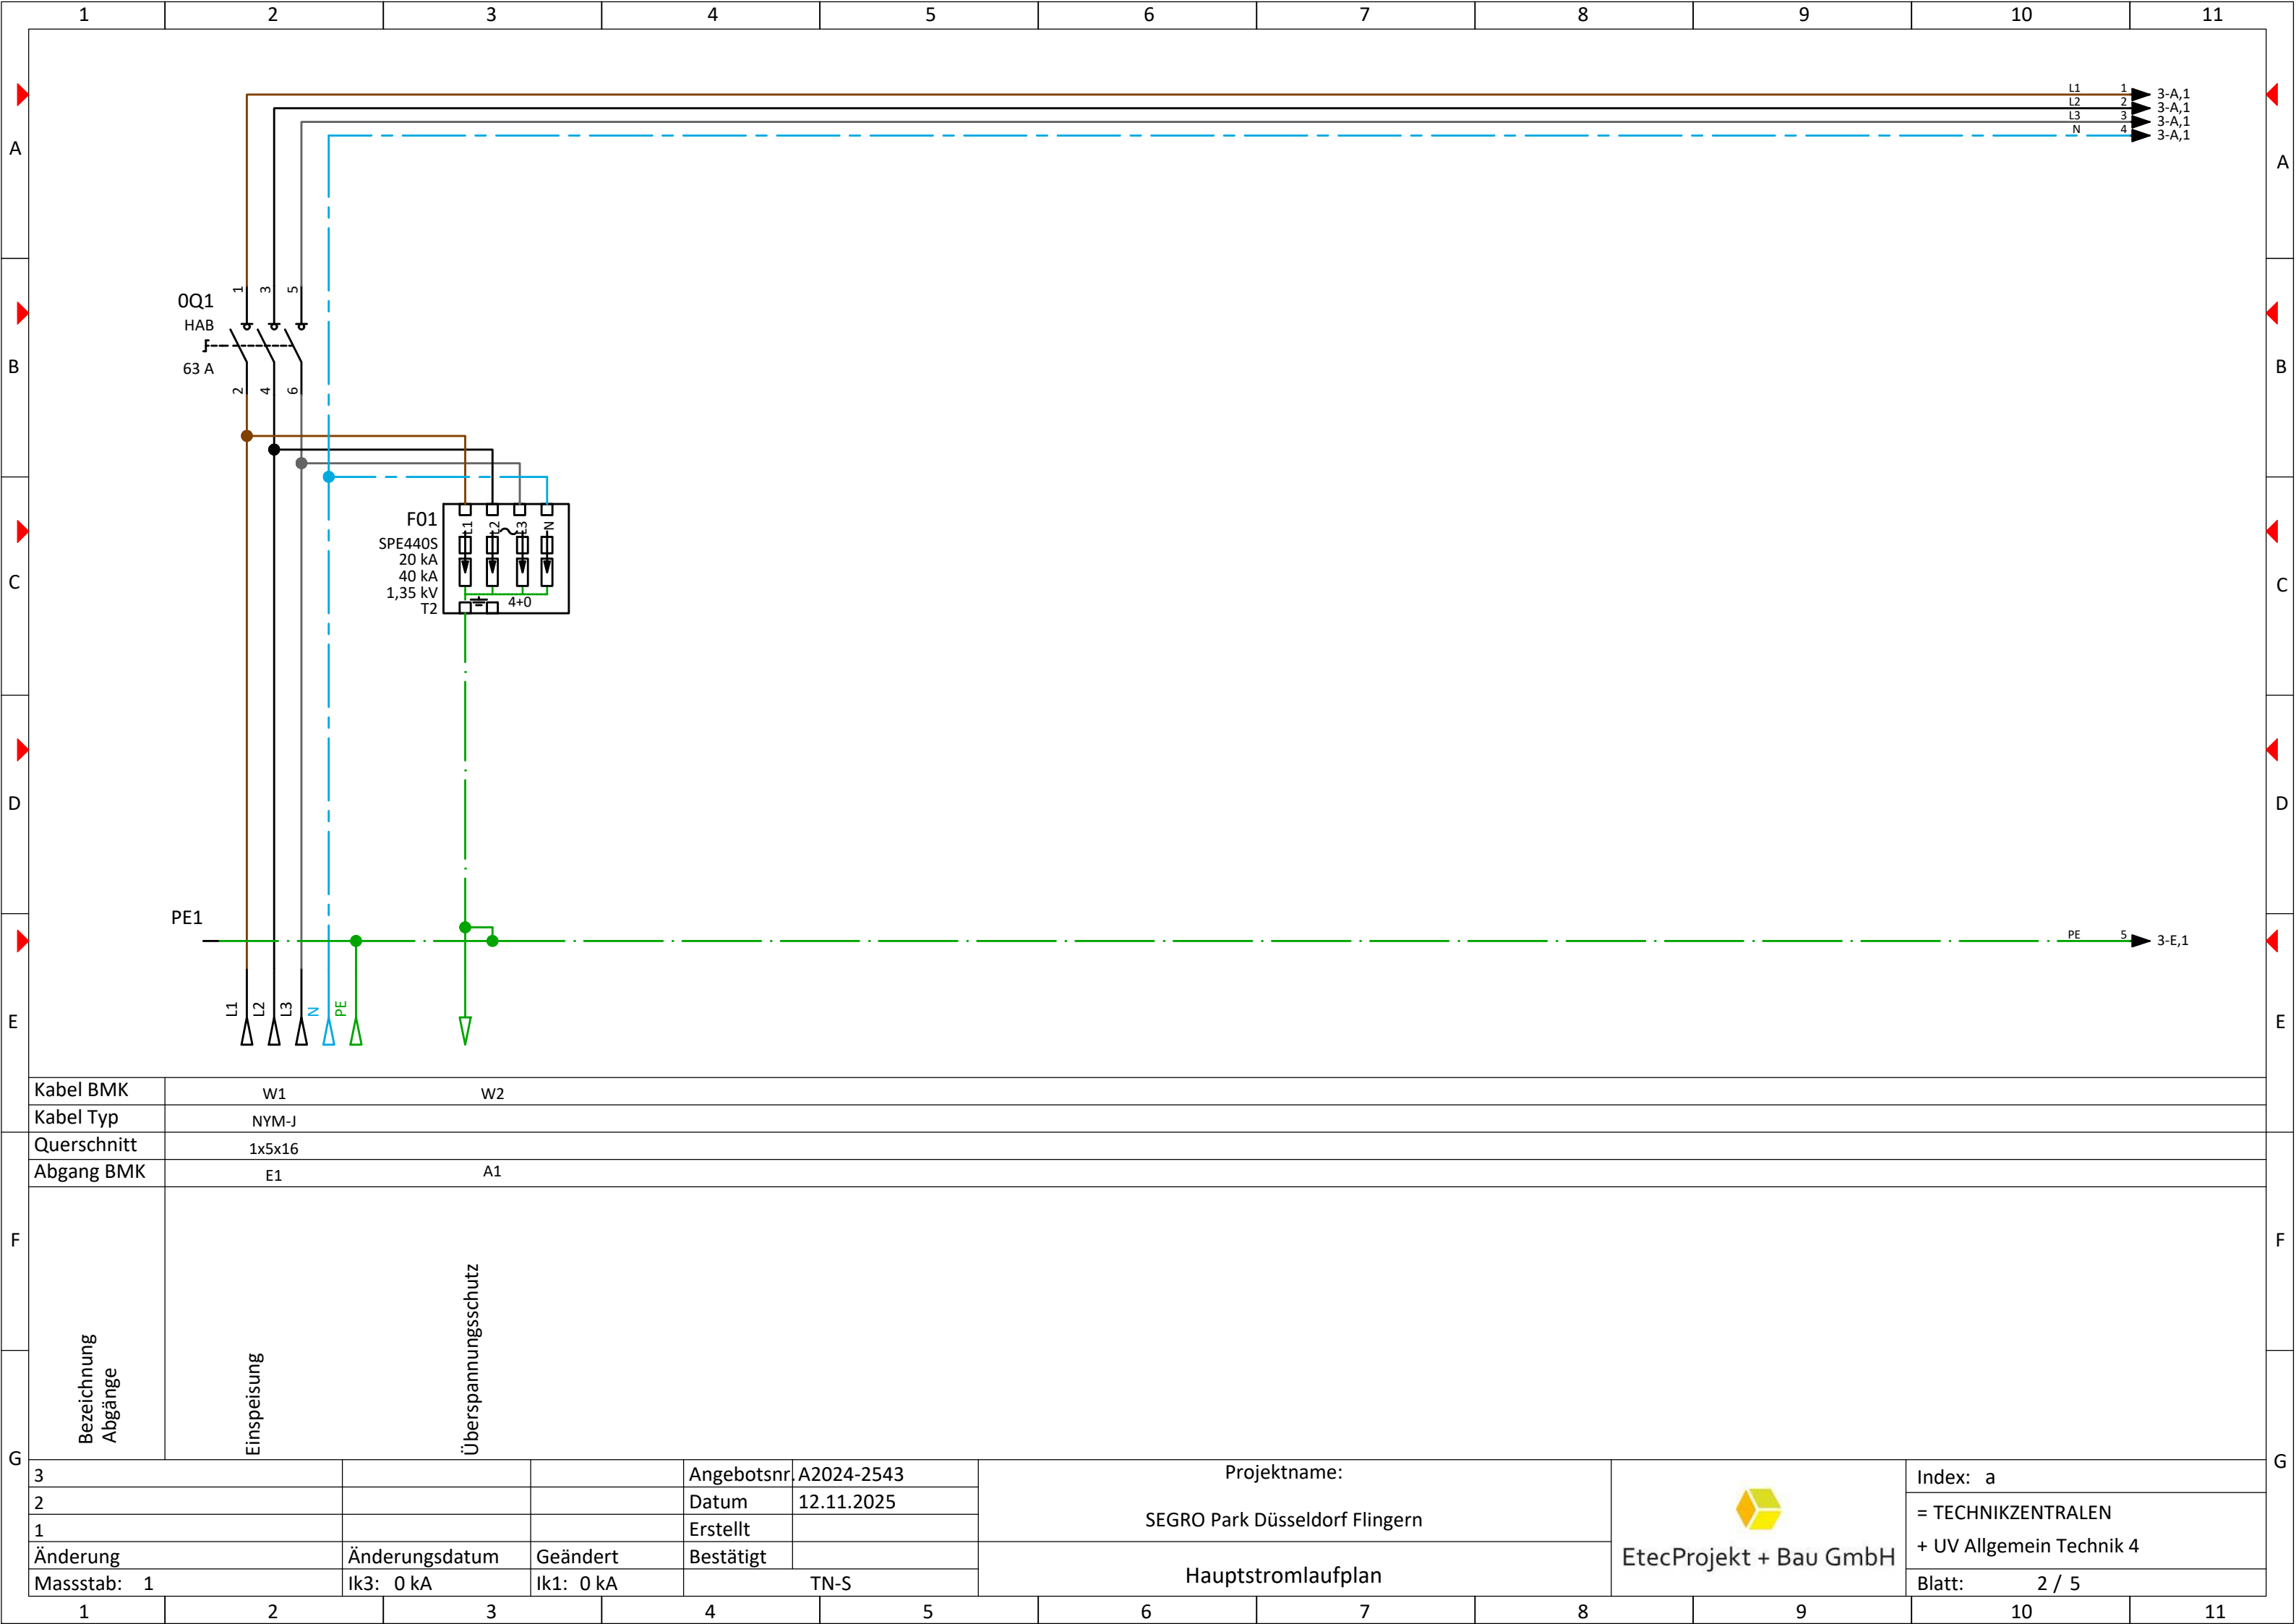


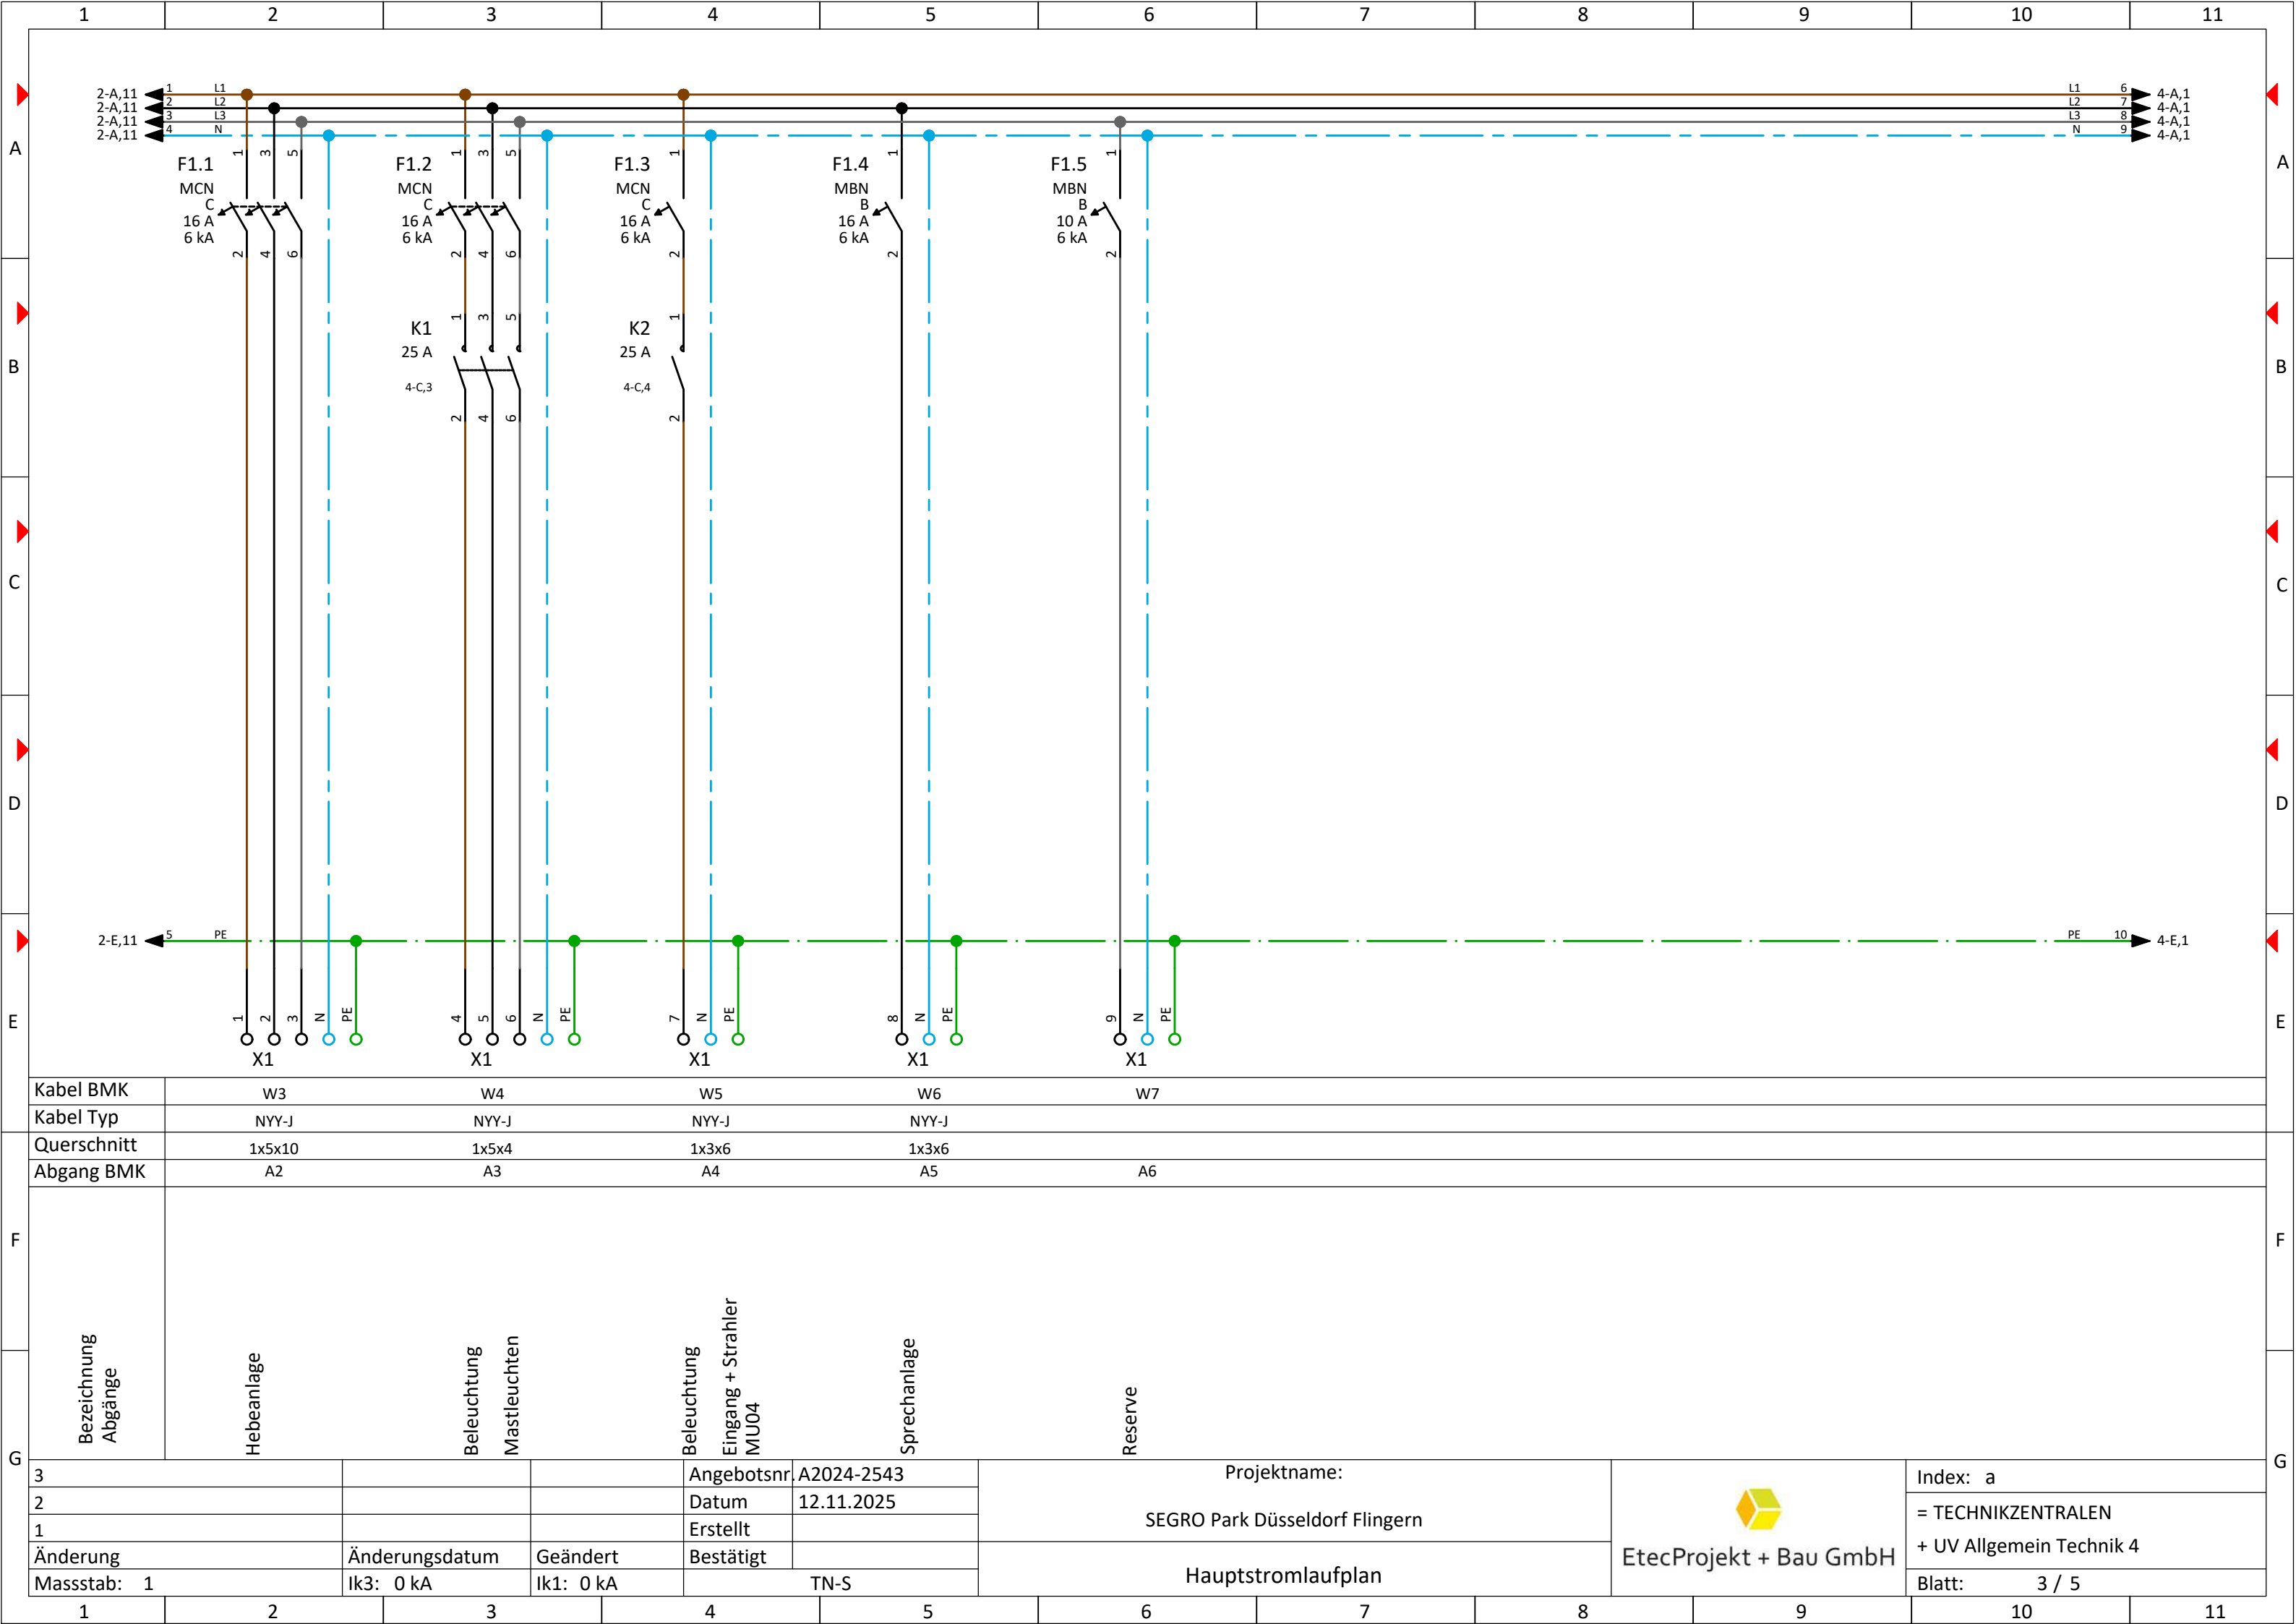

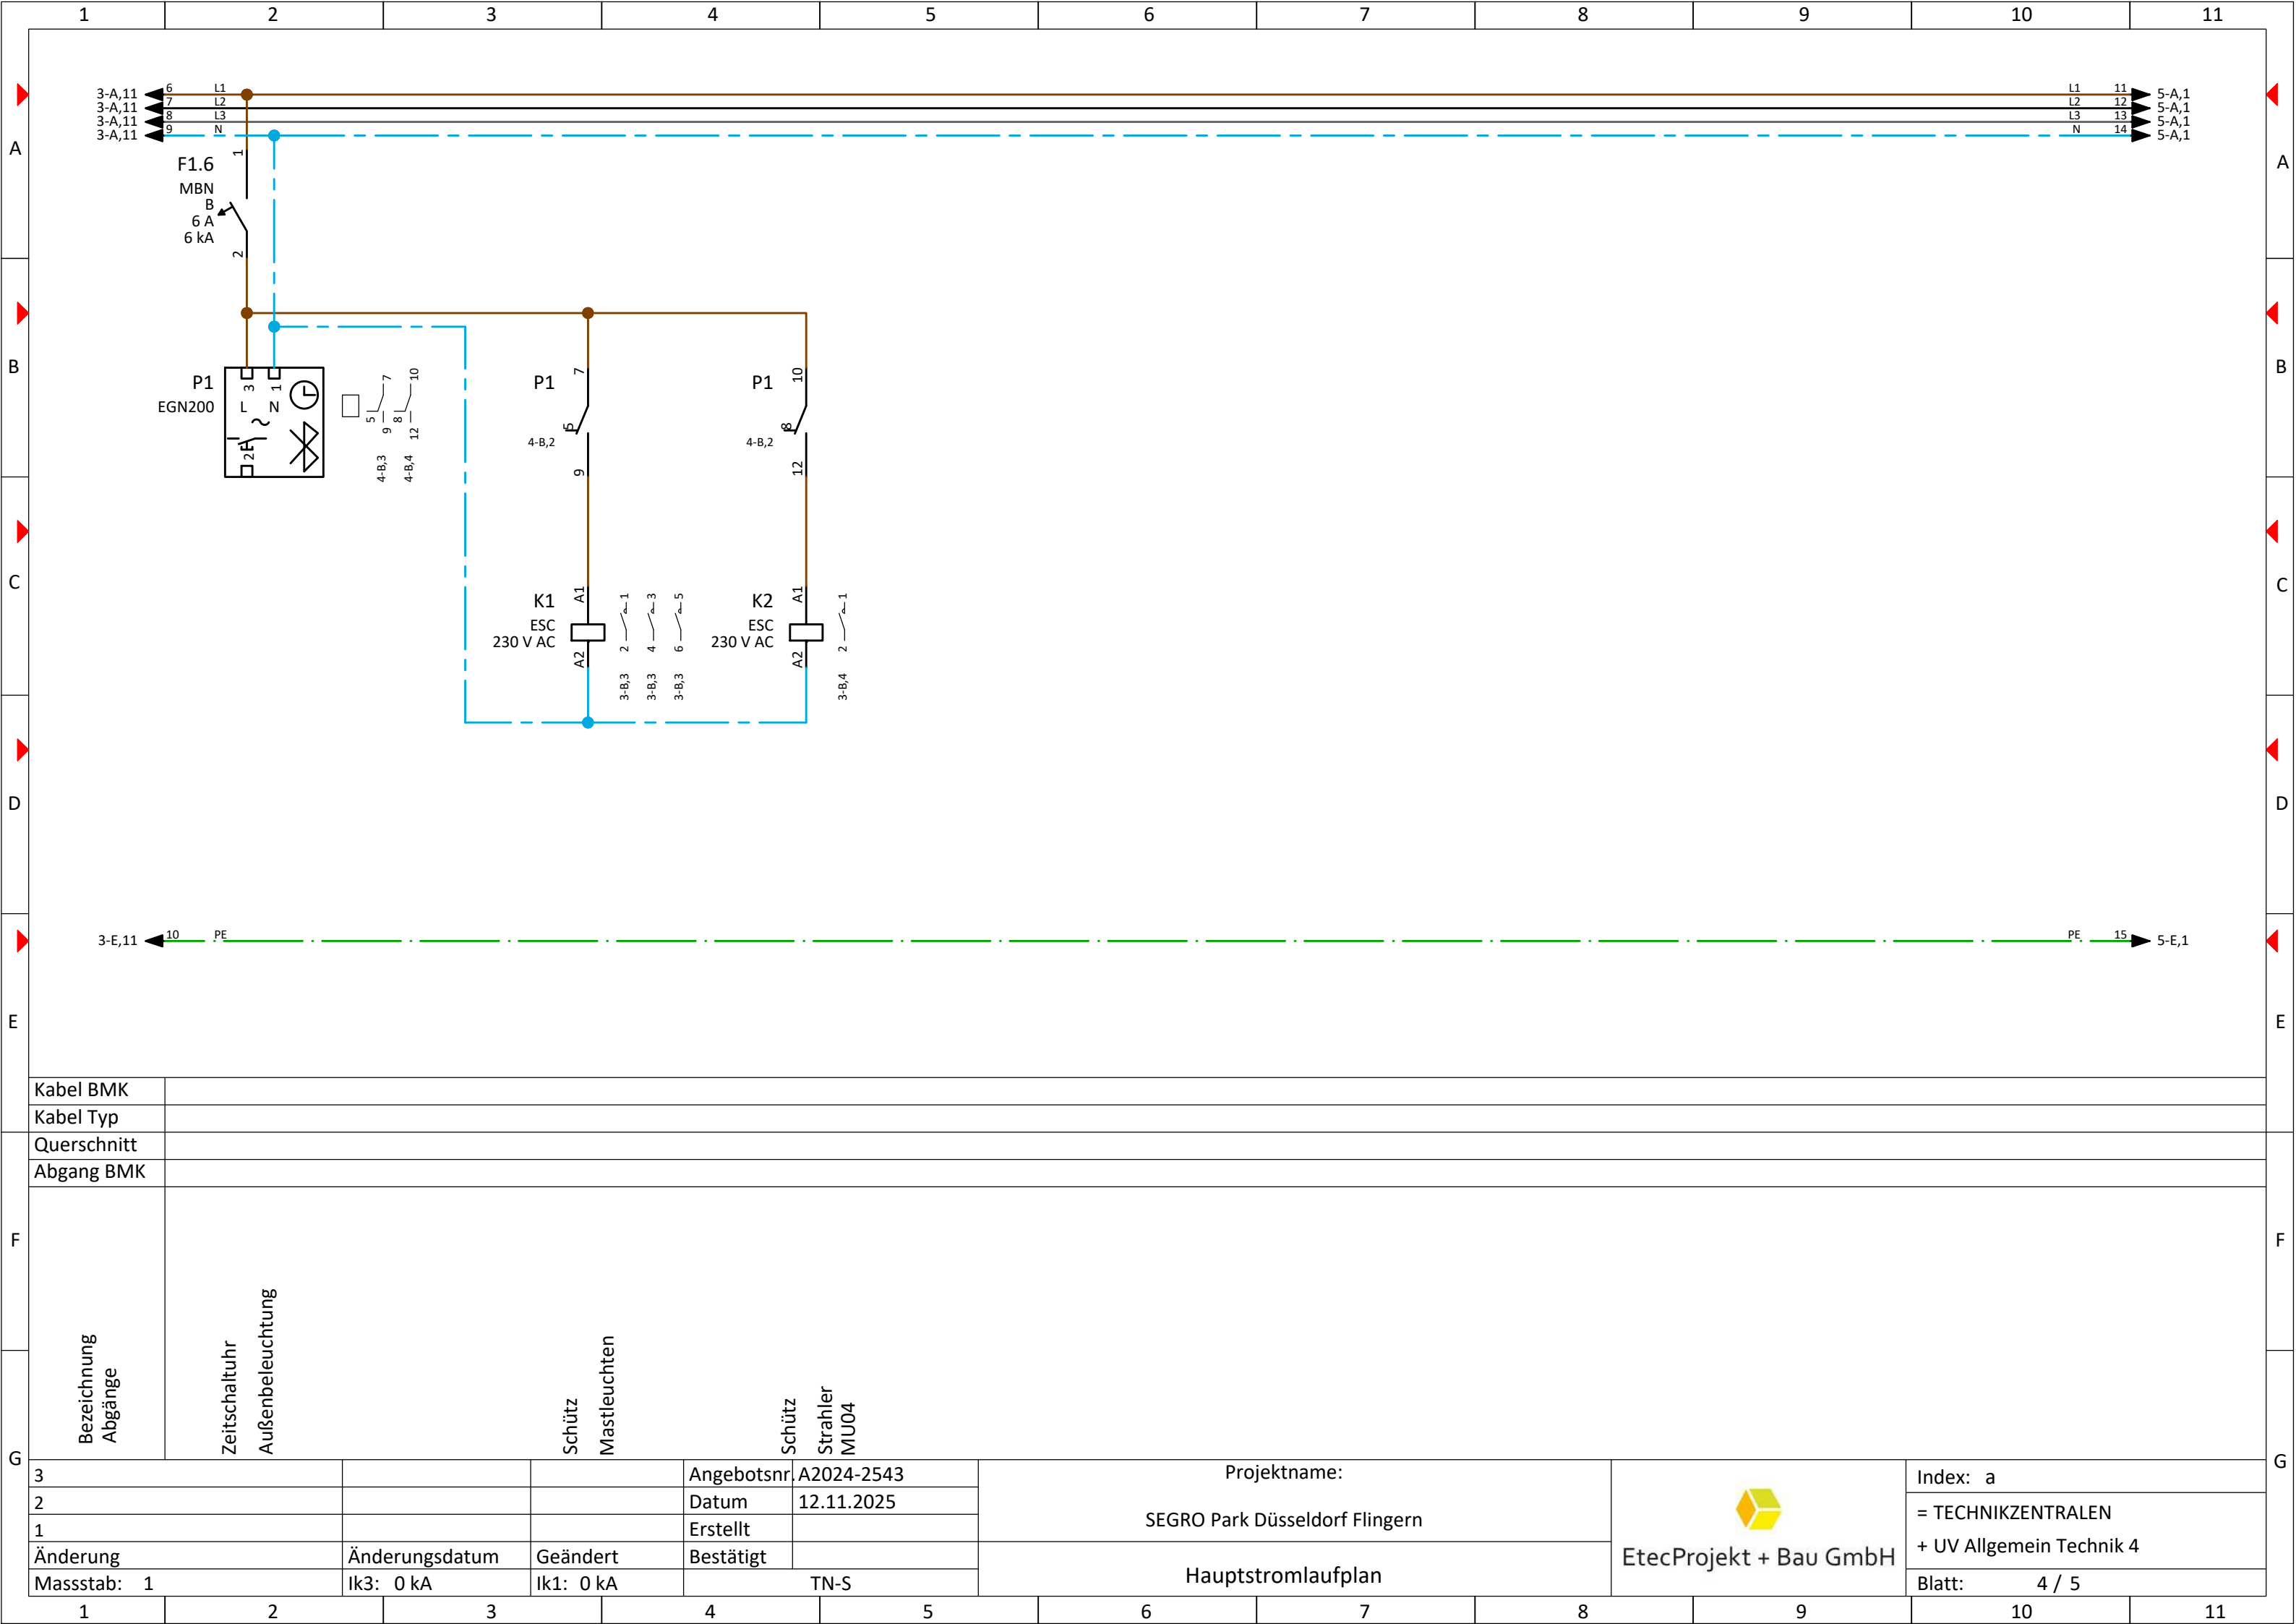

|                        |                                   |                |                        |                            |            |           |  |  |  |                                                    |   |                          |       |
|------------------------|-----------------------------------|----------------|------------------------|----------------------------|------------|-----------|--|--|--|----------------------------------------------------|---|--------------------------|-------|
| Kabel BMK              |                                   |                |                        |                            |            |           |  |  |  |                                                    |   |                          |       |
| Kabel Typ              |                                   |                |                        |                            |            |           |  |  |  |                                                    |   |                          |       |
| Querschnitt            |                                   |                |                        |                            |            |           |  |  |  |                                                    |   |                          |       |
| Abgang BMK             |                                   |                |                        |                            |            |           |  |  |  |                                                    |   |                          |       |
| Bezeichnung<br>Abgänge | Zeitschaltuhr<br>Außenbeleuchtung |                | Schütz<br>Mastleuchten | Schütz<br>Strahler<br>MU04 |            |           |  |  |  | Projektname:<br><br>SEGRO Park Düsseldorf Flingern | <br>EtecProjekt + Bau GmbH | Index: a                 |       |
|                        |                                   |                |                        |                            |            |           |  |  |  |                                                    |   | = TECHNIKZENTRALEN       |       |
|                        |                                   |                |                        |                            |            |           |  |  |  |                                                    |   | + UV Allgemein Technik 4 |       |
|                        |                                   |                |                        |                            |            |           |  |  |  |                                                    |   | Blatt:                   | 4 / 5 |
|                        |                                   |                |                        |                            |            |           |  |  |  |                                                    |   |                          |       |
| 3                      |                                   |                |                        | Angebotsnr.                | A2024-2543 |           |  |  |  | Hauptstromlaufplan                                 |   |                          |       |
| 2                      |                                   |                |                        | Datum                      | 12.11.2025 |           |  |  |  |                                                    |   |                          |       |
| 1                      |                                   |                |                        | Erstellt                   |            |           |  |  |  |                                                    |   |                          |       |
| Änderung               |                                   | Änderungsdatum |                        | Geändert                   |            | Bestätigt |  |  |  |                                                    |   |                          |       |
| Massstab: 1            |                                   | Ik3: 0 kA      |                        | Ik1: 0 kA                  |            | TN-S      |  |  |  |                                                    |   |                          |       |

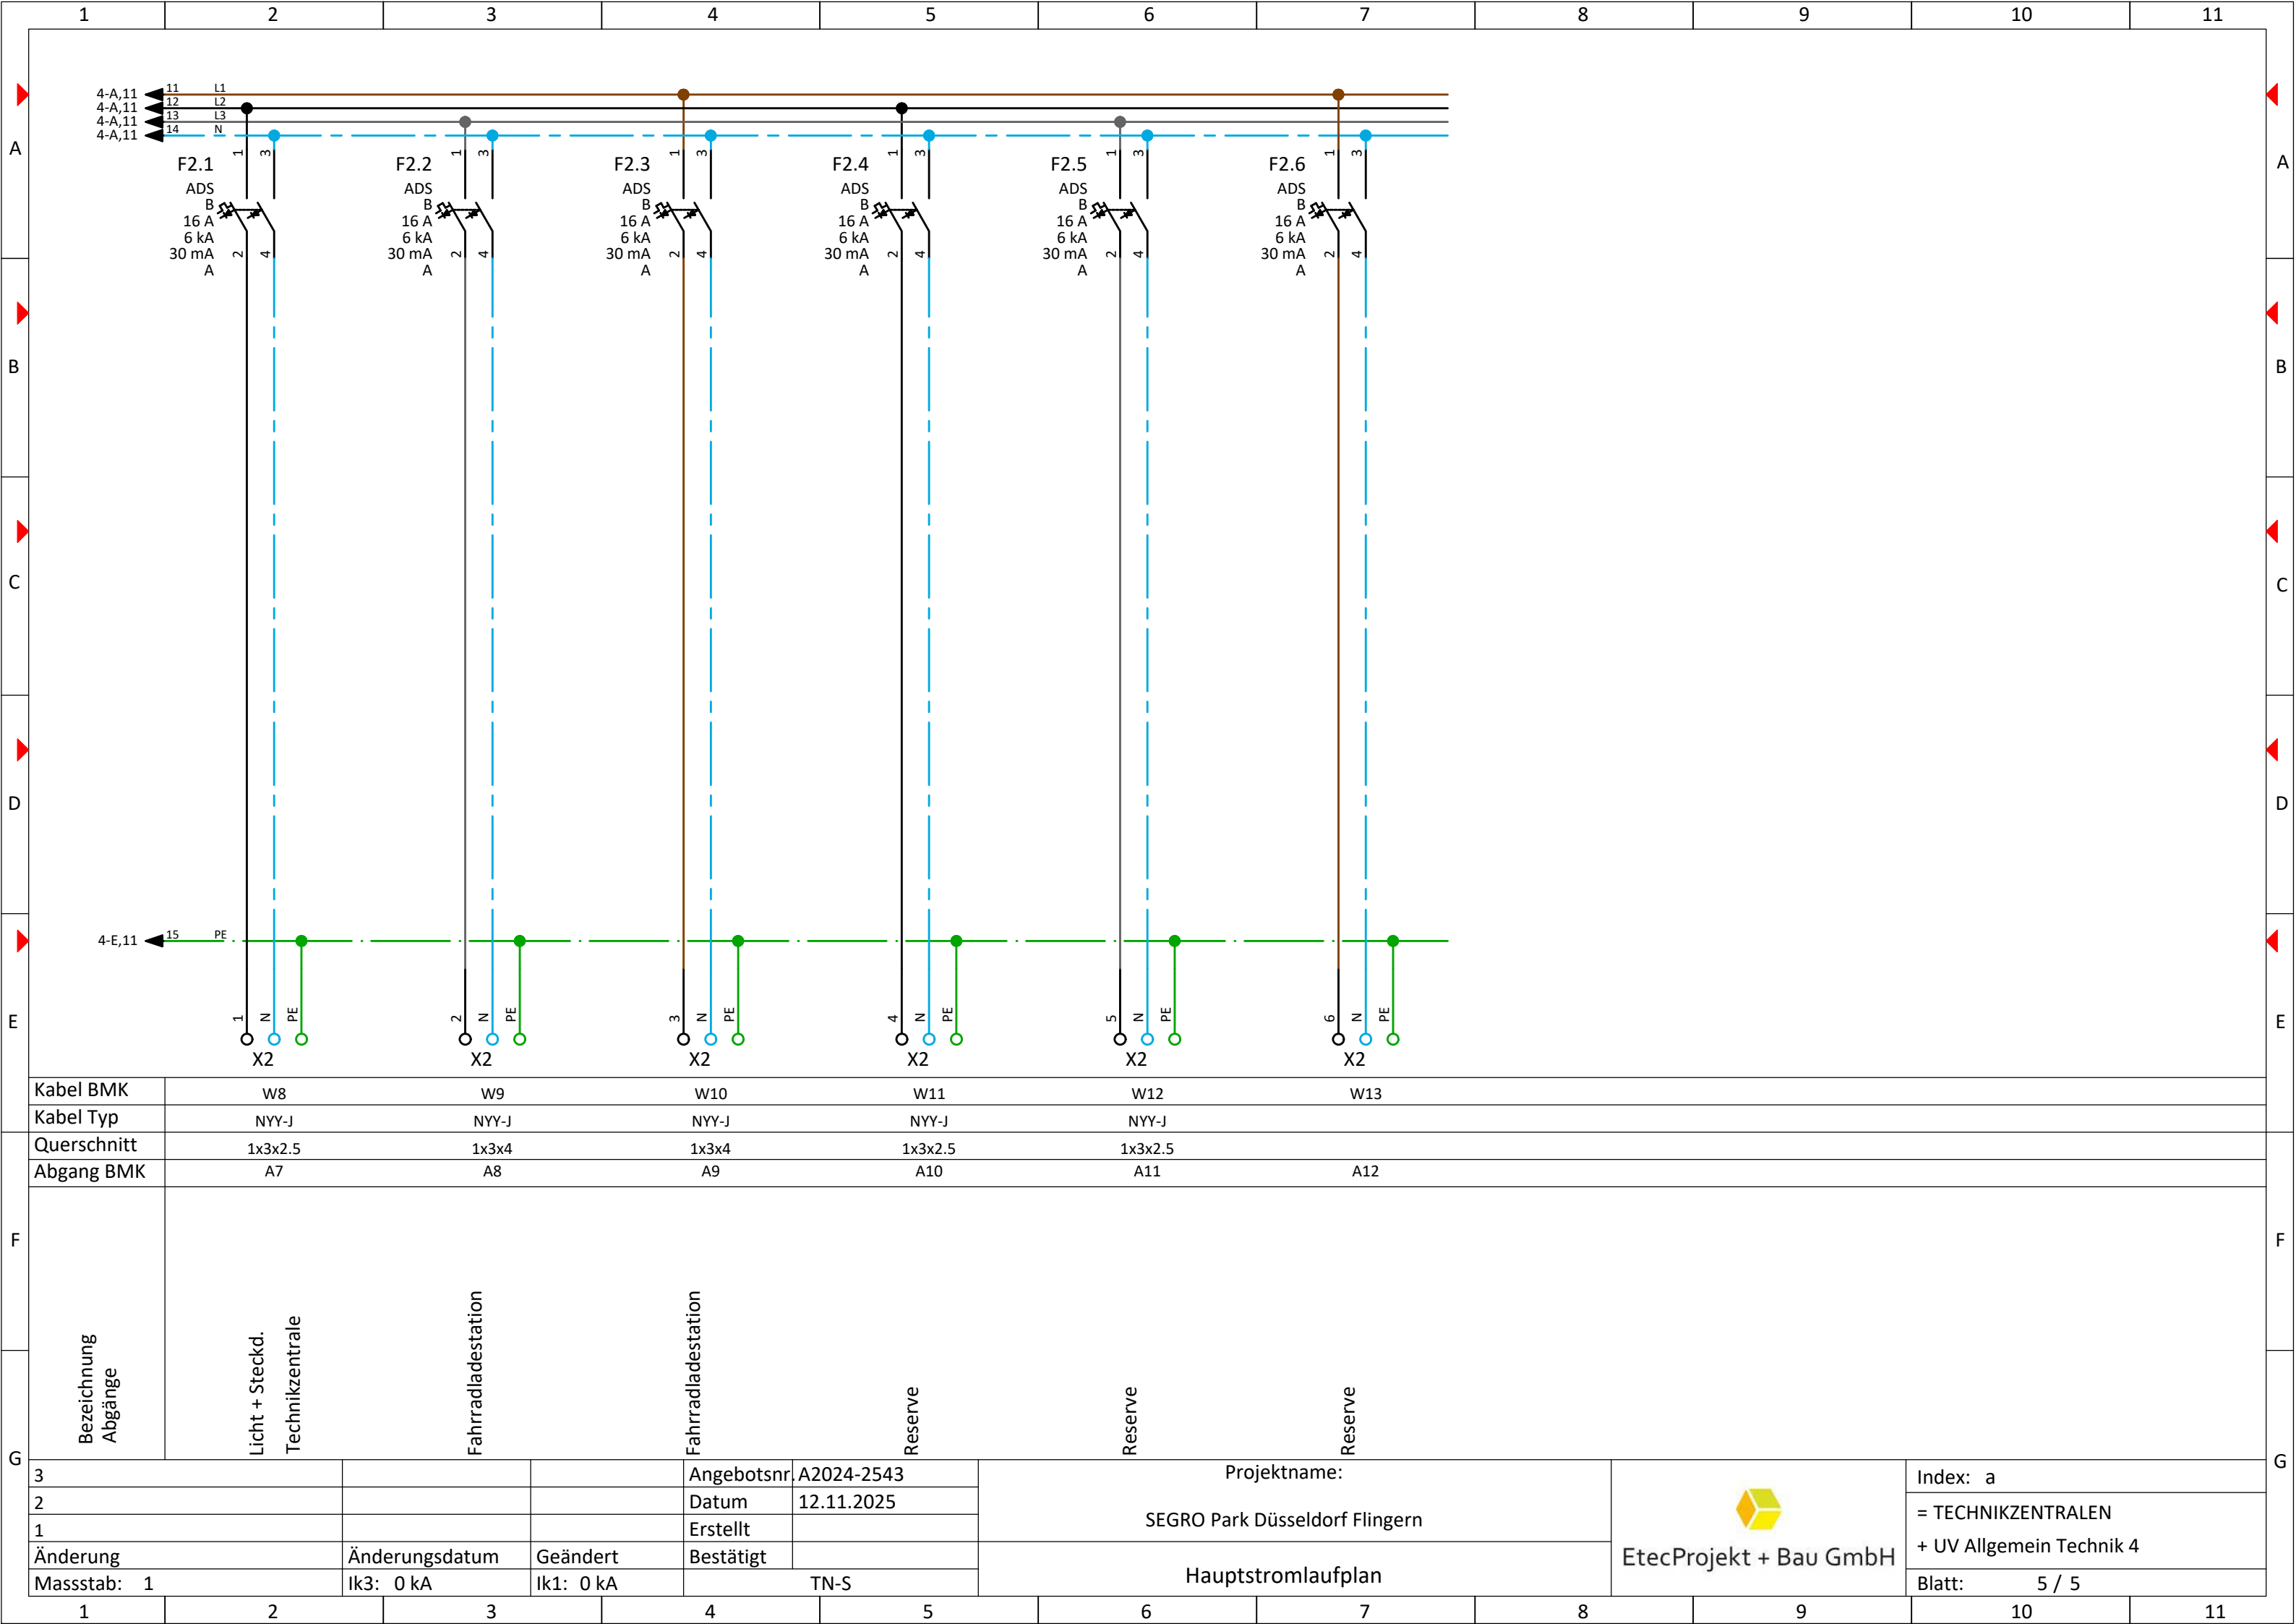

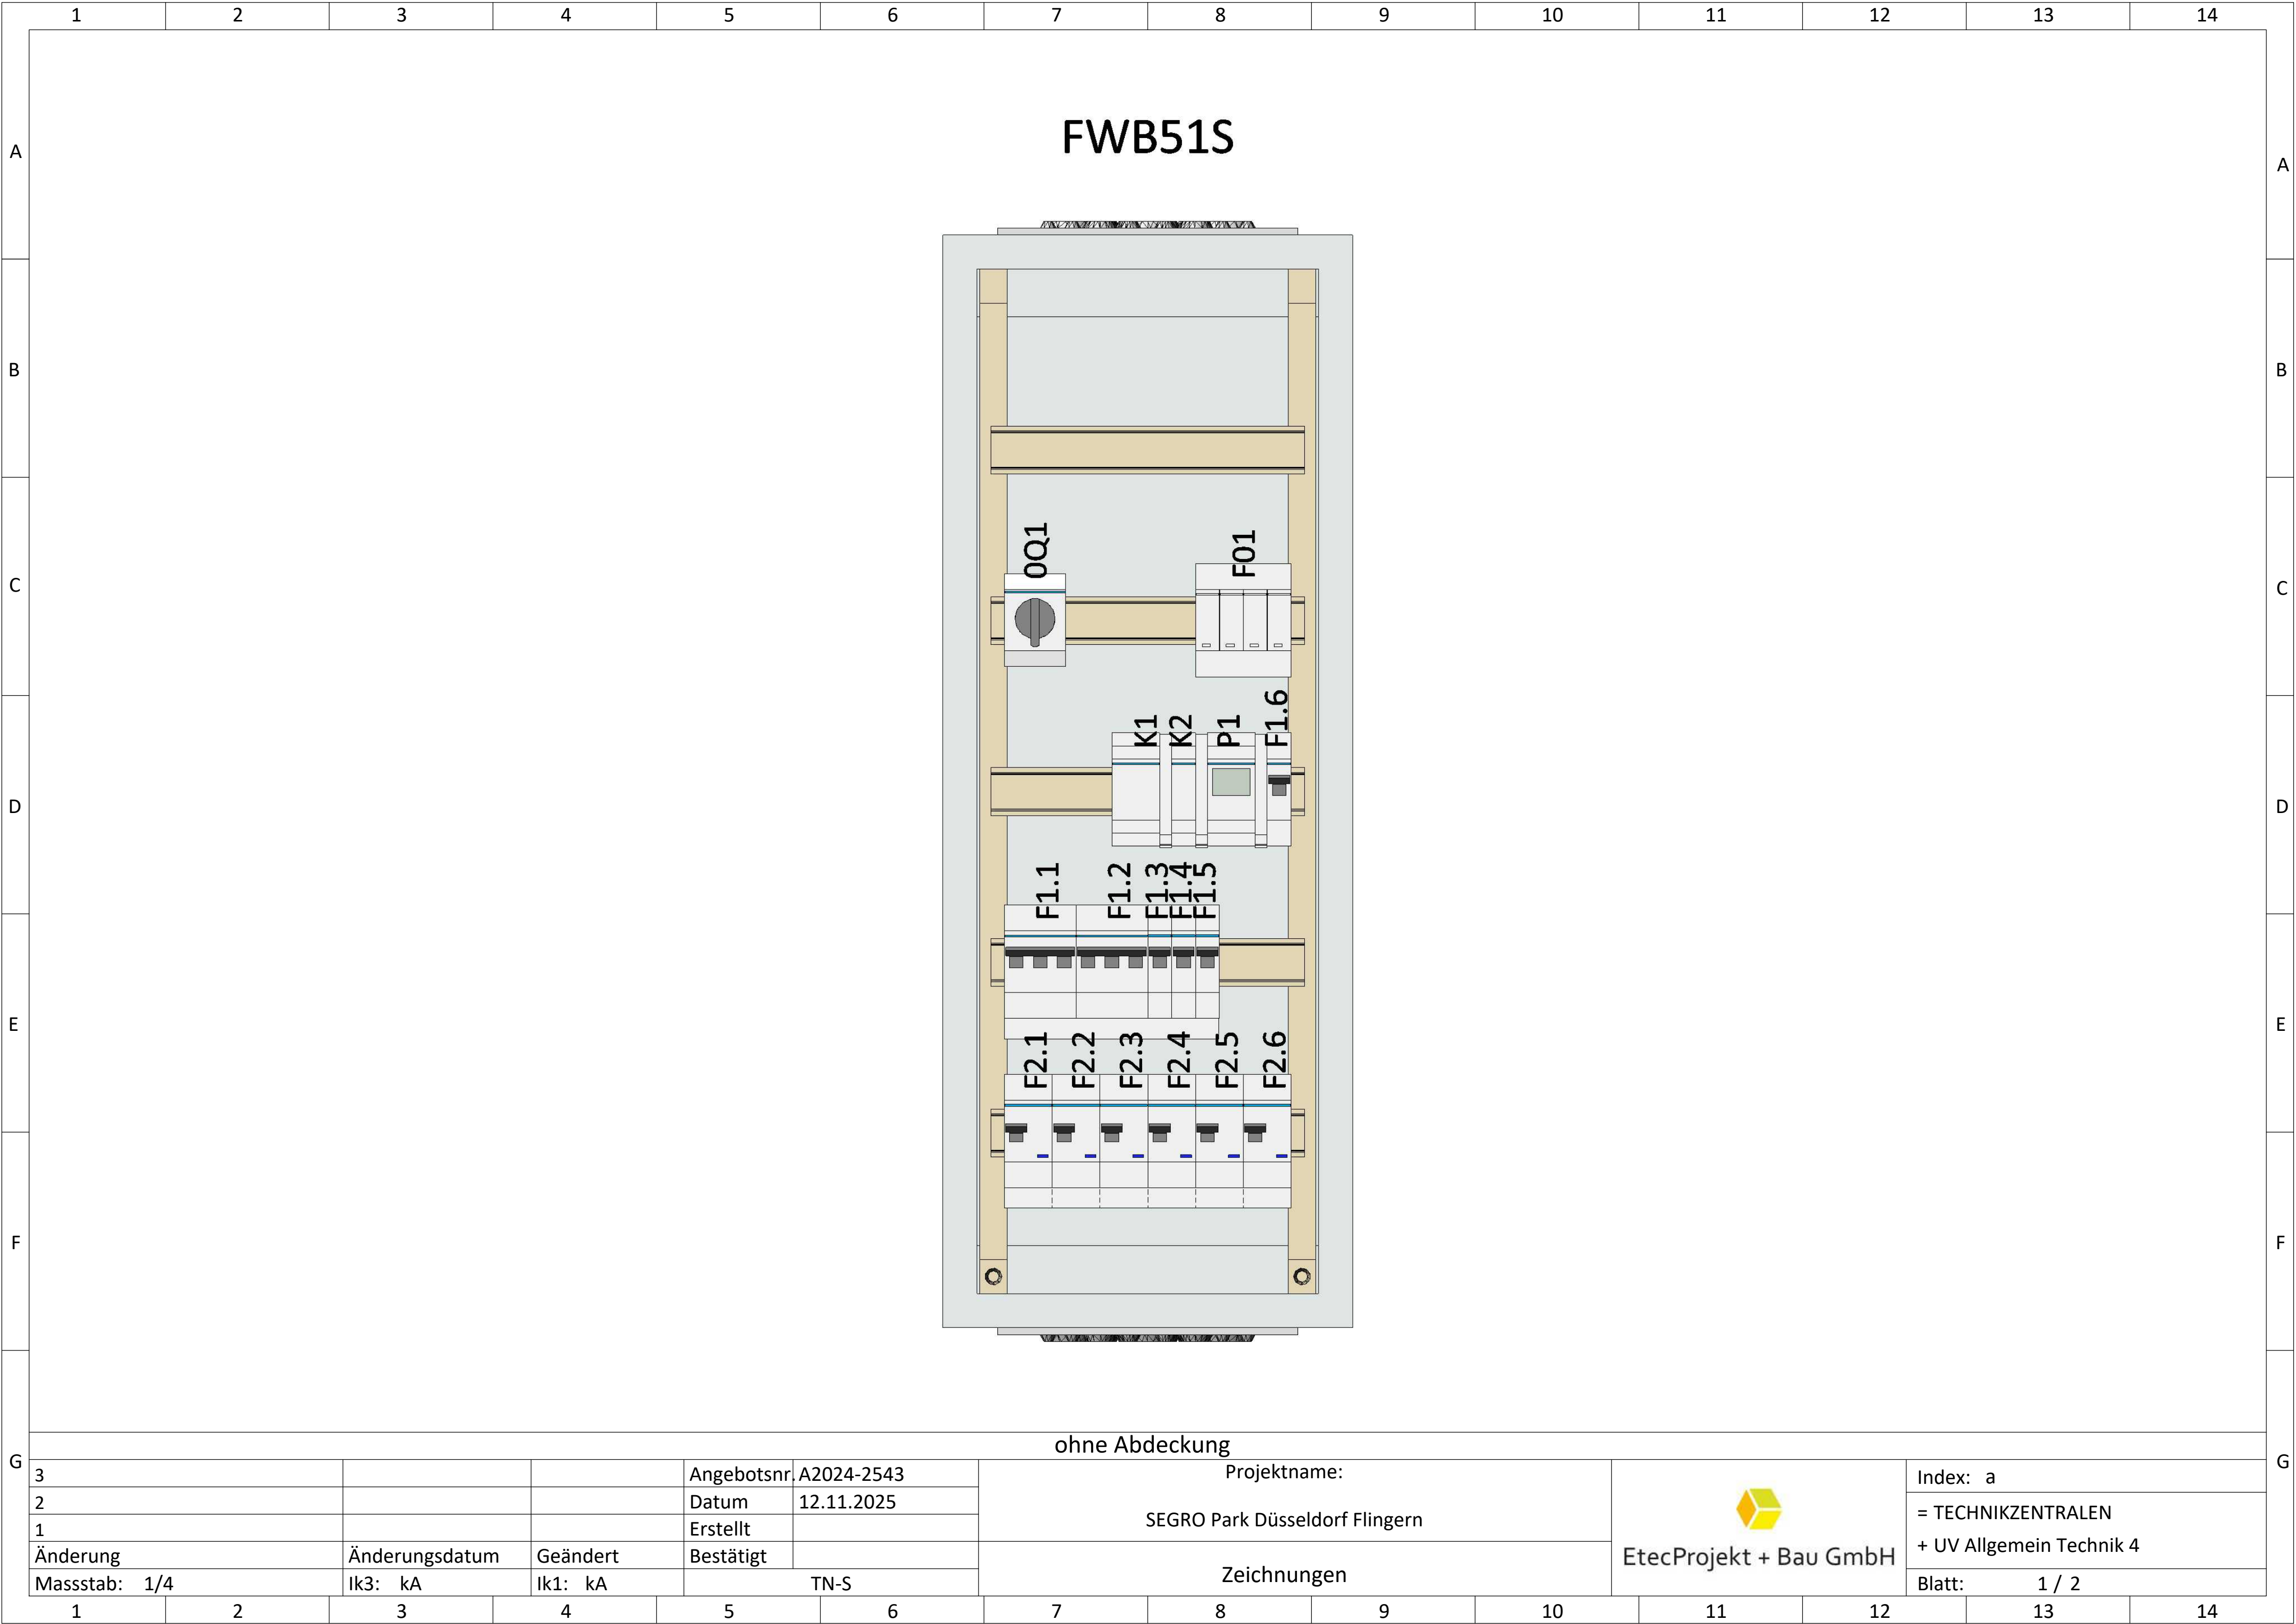

A

A

B

B

C

C

D

D

E

E


F

F

G

G

## FWB51S

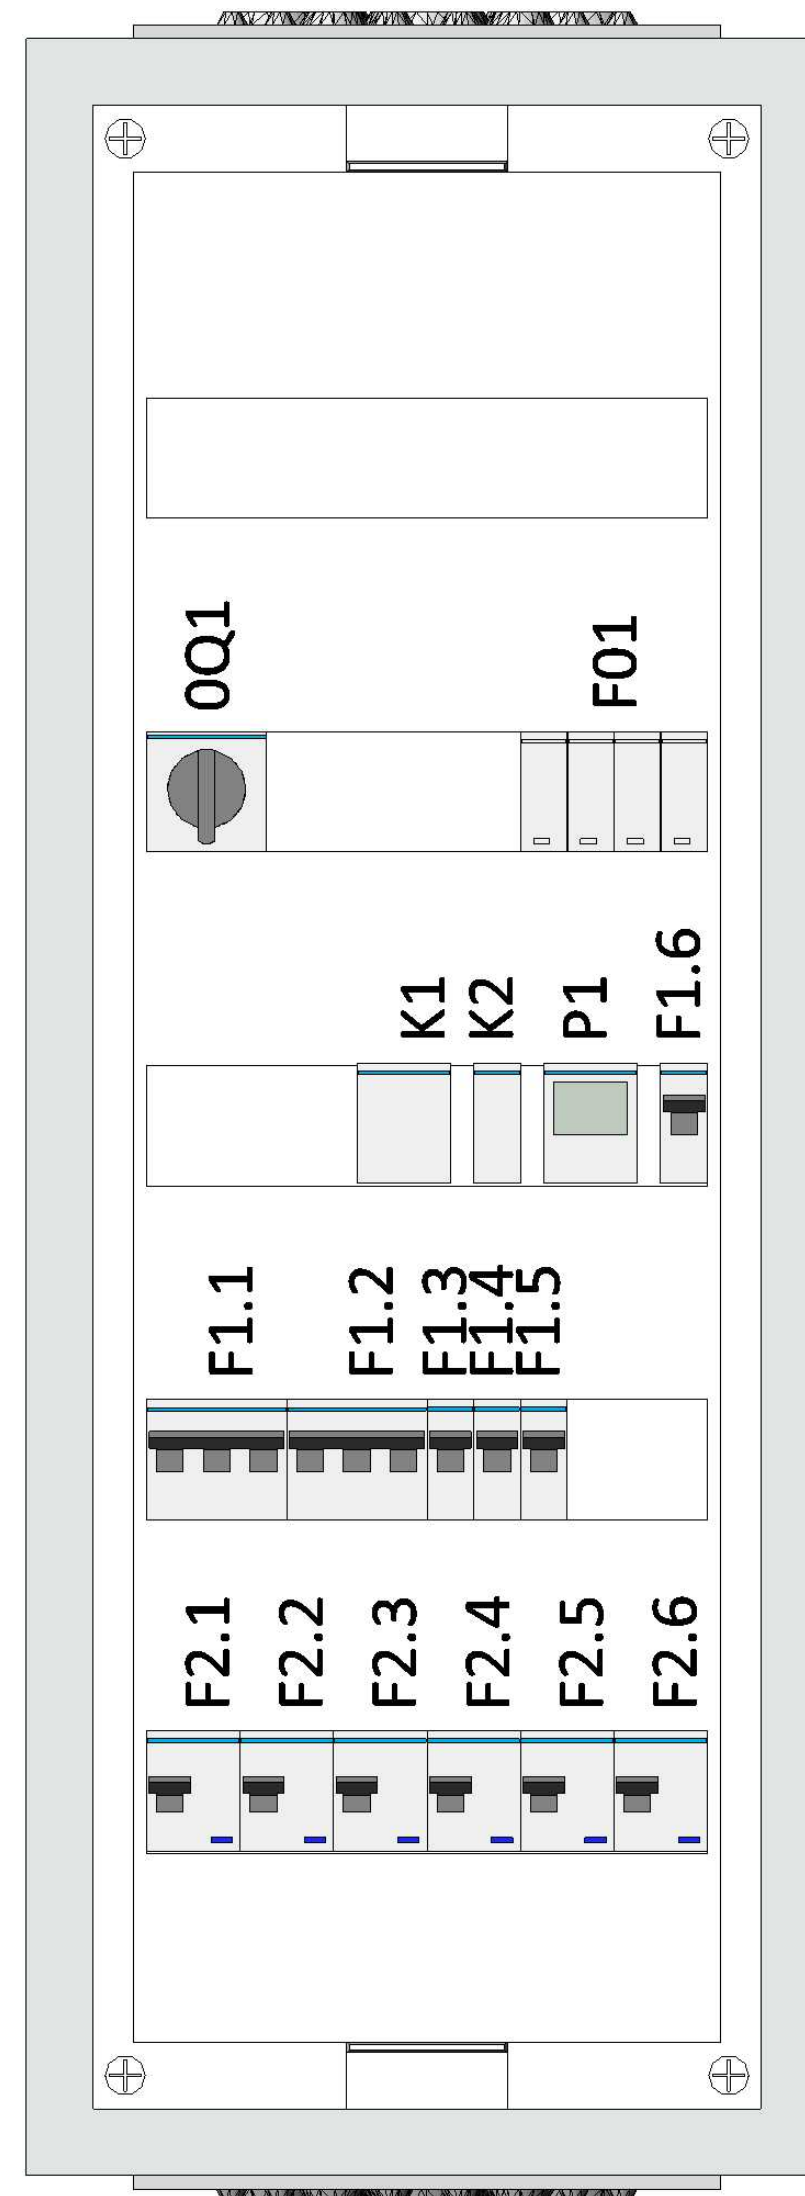

mit Abdeckung

|               |                |          |             |            |                                                    |   |                          |
|---------------|----------------|----------|-------------|------------|----------------------------------------------------|---|--------------------------|
| 3             |                |          | Angebotsnr. | A2024-2543 | Projektname:<br><br>SEGRO Park Düsseldorf Flöngern | <br><b>EtecProjekt + Bau GmbH</b> | Index: a                 |
| 2             |                |          | Datum       | 12.11.2025 |                                                    |   | = TECHNIKZENTRALEN       |
| 1             |                |          | Erstellt    |            |                                                    |   | + UV Allgemein Technik 4 |
| Änderung      | Änderungsdatum | Geändert | Bestätigt   |            | Zeichnungen                                        |   |                          |
| Massstab: 1/4 | lk3: kA        | lk1: kA  | TN-S        |            |                                                    |   | Blatt: 2 / 2             |