

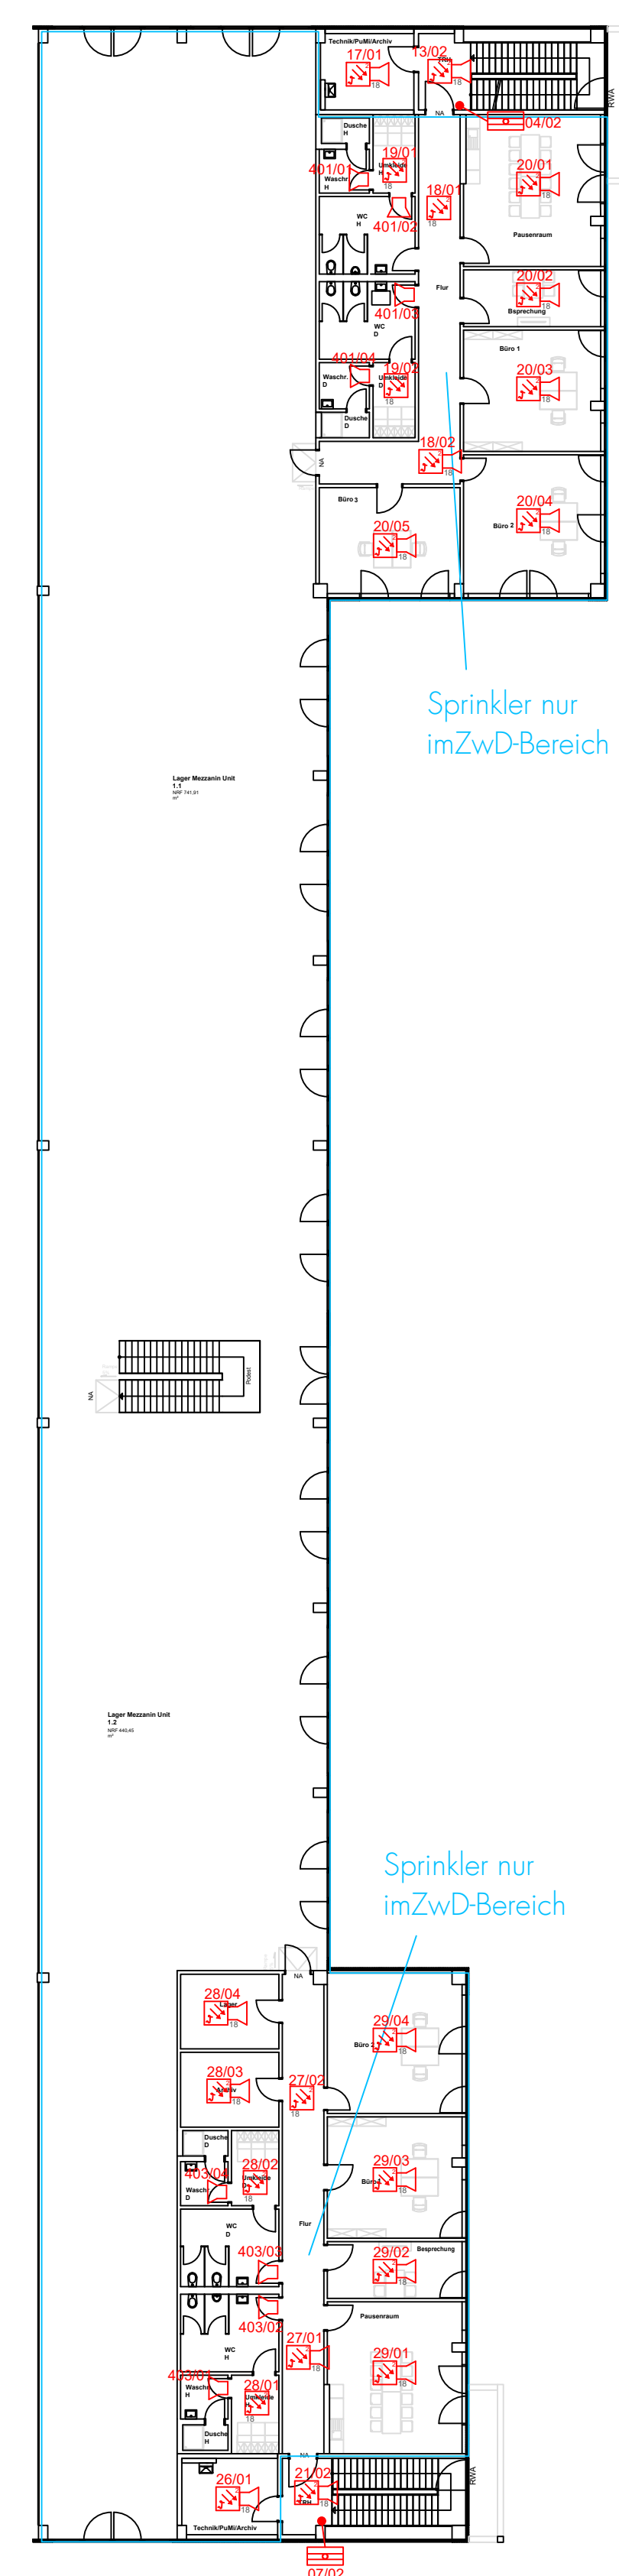


Hallen

Mezzanine

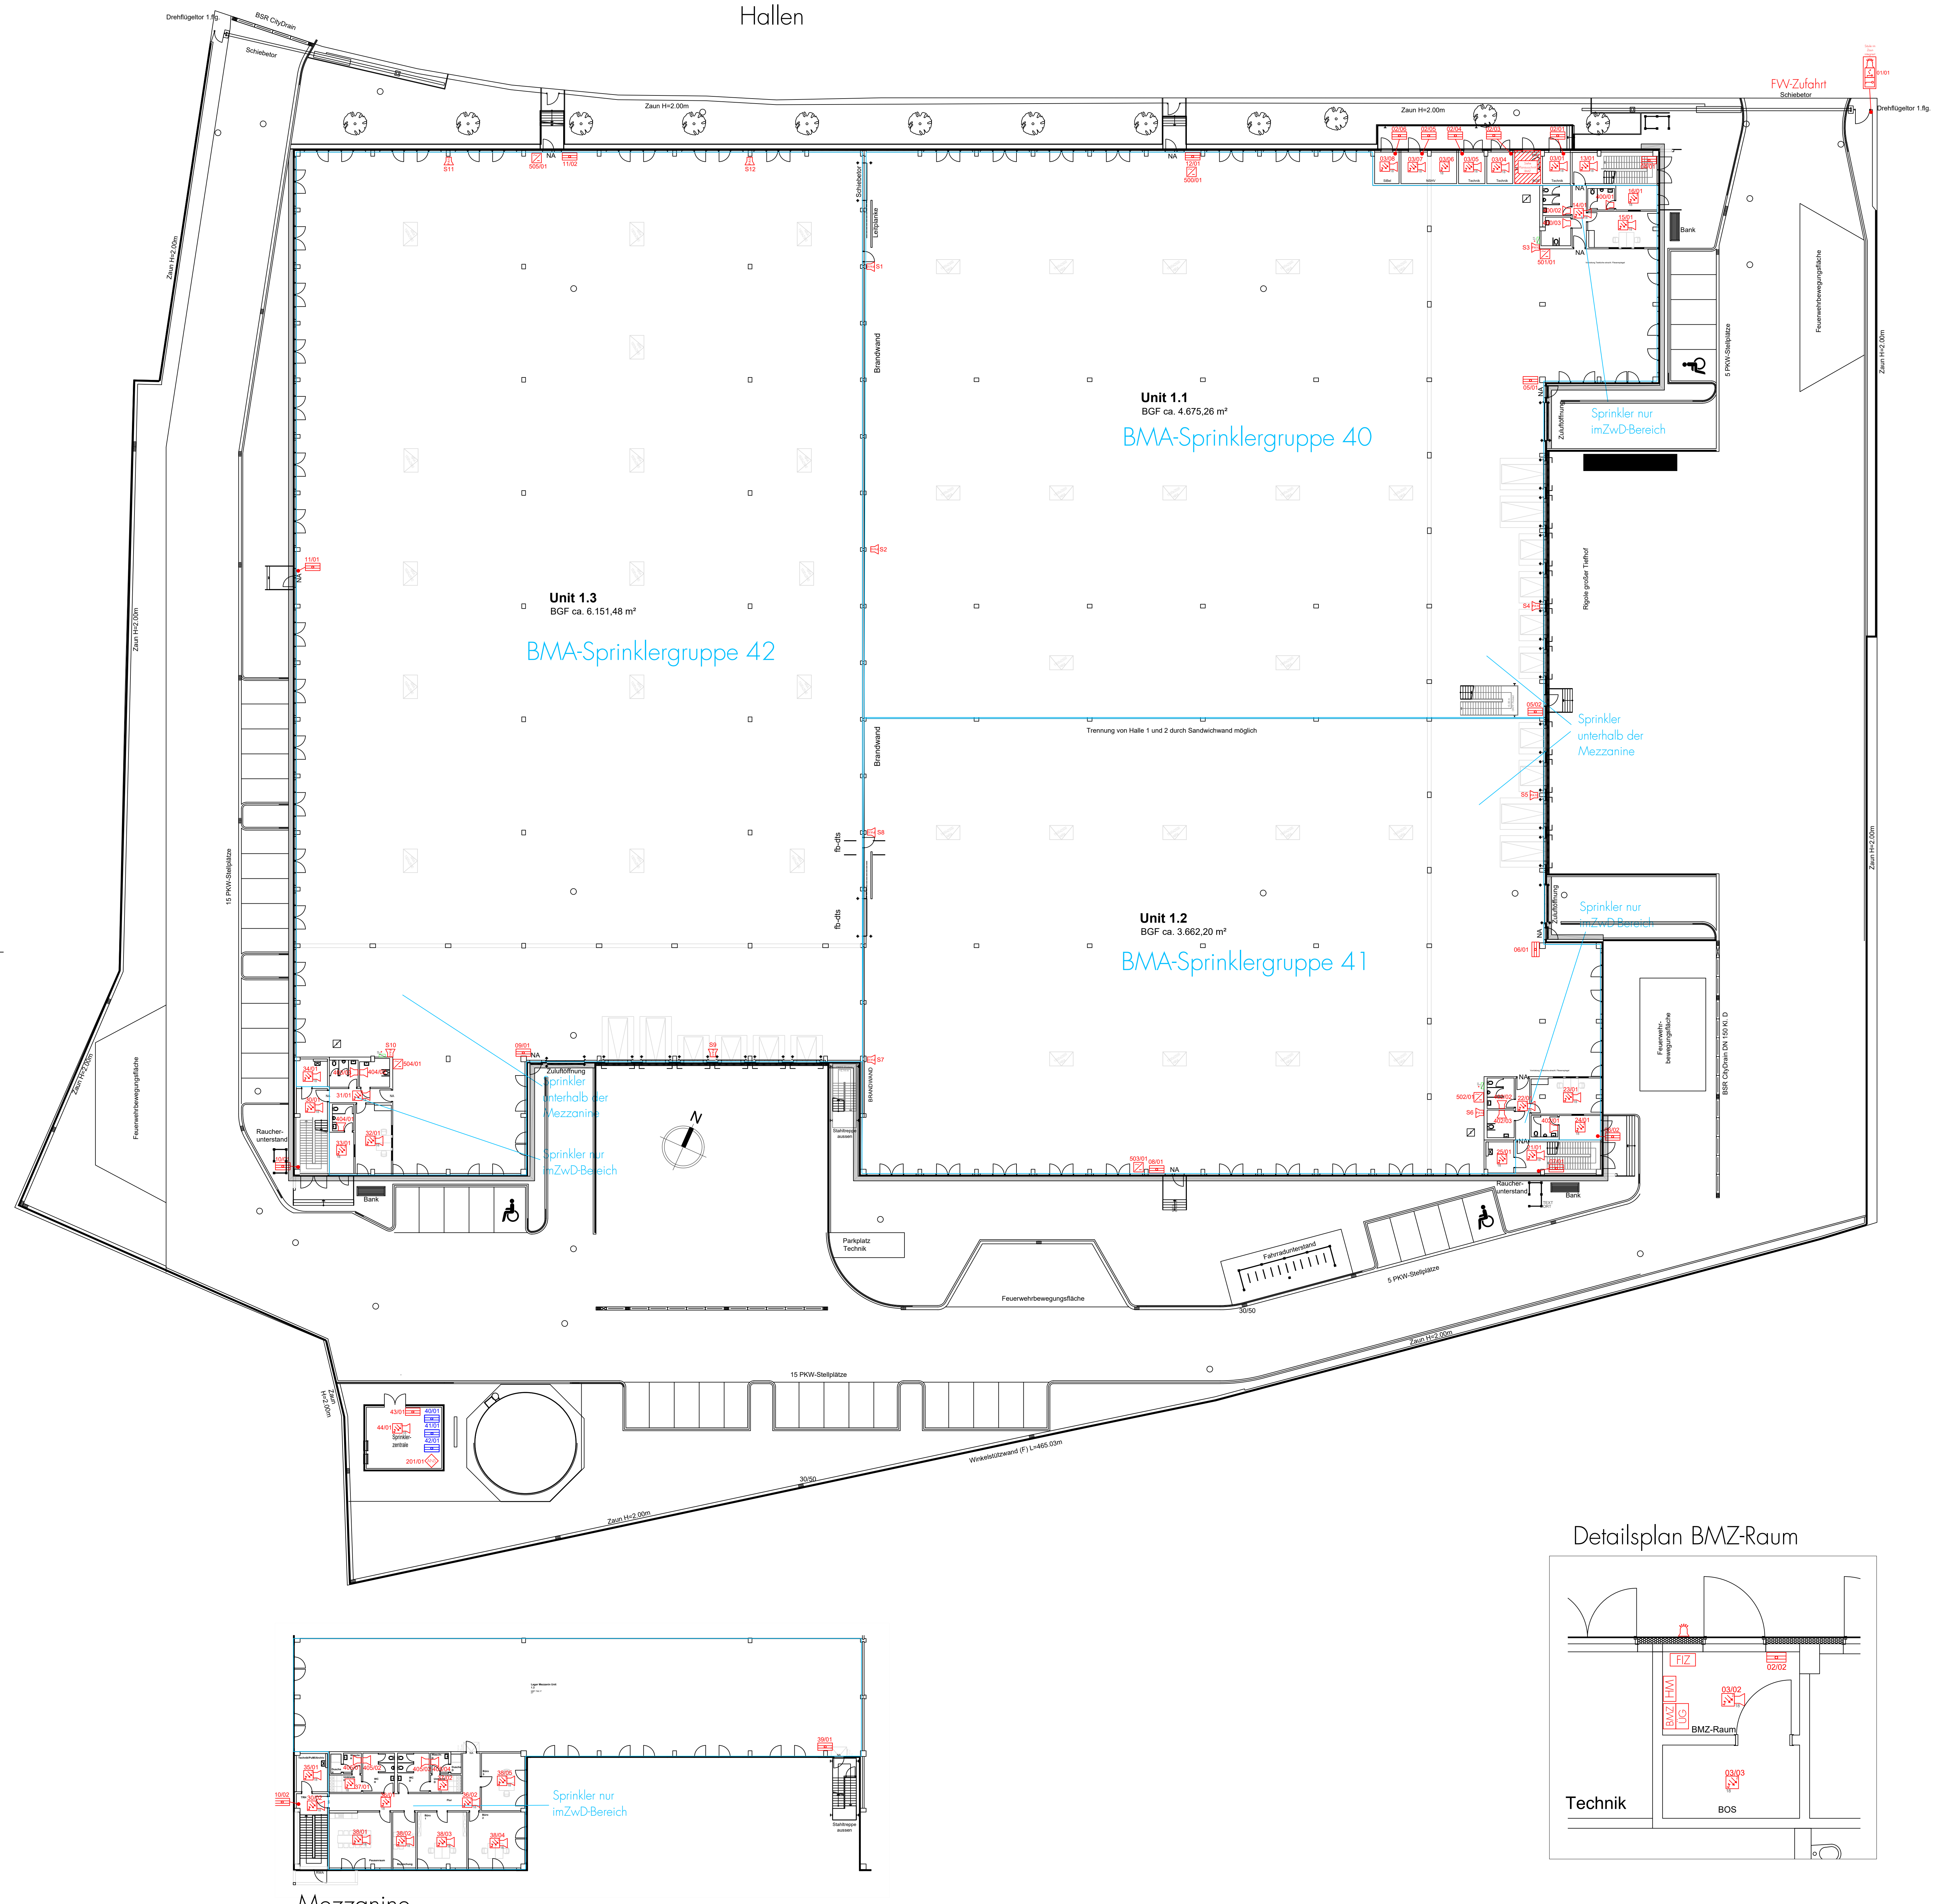

Detailsplan BMZ-Raum

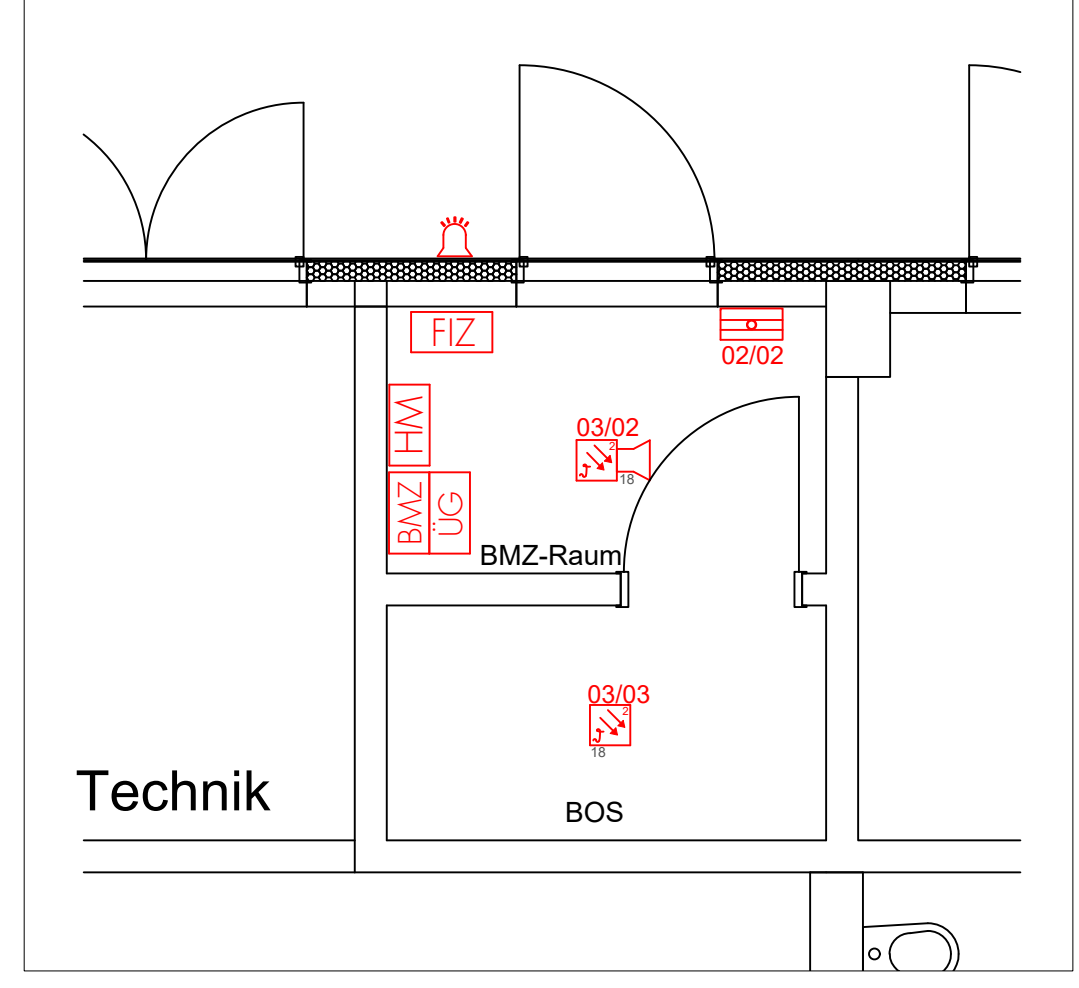

Legende			
Symbol	Bezeichnung	Anzahl	
	Anschließmodul	1	
	Blitzlampe	3	
	Brandmelderzentrale	1	
	Druckknopfmelder	23	
	Feuerwehr Informationszentrale	1	
	Freischallelement	2	
	Hauptmelder	1	
	Multisensormelder O2T	15	
	Netzgeraet	6	
	Prüfmelder	3	
	Schlüsseldepot	2	
	Sirene	21	
	Sirene PA10	13	
	Übertragungsgerät	1	

Gezeichnet		Gezeichnet	Gezeichnet	Gezeichnet	Gezeichnet
Brandmeldeanlage		Brandmeldeanlage	Brandmeldeanlage	Brandmeldeanlage	Brandmeldeanlage
Auftrag		Auftrag	Auftrag	Auftrag	Auftrag
000000		000000	000000	000000	000000
Datum		Datum	Datum	Datum	Datum
22.04.2026		22.04.2026	22.04.2026	22.04.2026	22.04.2026
Entwurf und Genehmigung		Entwurf und Genehmigung	Entwurf und Genehmigung	Entwurf und Genehmigung	Entwurf und Genehmigung
Jümpertz		Jümpertz	Jümpertz	Jümpertz	Jümpertz
Menge		Menge	Menge	Menge	Menge
1/250		1/250	1/250	1/250	1/250
Blatt		Blatt	Blatt	Blatt	Blatt
1/1		1/1	1/1	1/1	1/1