

EtecProjekt+Bau GmbH
Heinrich-Hertz-Straße 22a
40699 Erkrath

021121023300 info@etecprojekt.de

SCHALTSCHRANKBAU CE
NICHT REVIDIERT!

Projektname: SEGRO Park Düsseldorf Flingern
Kom-Nr./Angebots-NR.: A2024-2543 Ausführungsplan
Bezeichnung Ort: UV OG Unit (LI03)
Auftragsnummer: AB2024-1049 Klemmenfabrikat:
Baujahr: 04 / 2025 WAGO / HAGER

Farbkennzeichnung der Leiter (in Anlehnung an VDE0113 Teil1):	
Außenleiter:	schwarz
Neutralleiter:	hellblau
Steuerspannung 230V AC:	rot
Steuerspannung 24V DC:	dunkelblau
Steuerspannung 24V AC:	braun
Fremdspannung:	orange
Messung:	weiss
Sensorleitung:	violett

Technische Daten der Schaltgerätekombination:


Bemessungsbetriebsspannung / -Frequenz:	Un: 400V / 50Hz	Netzform:	TN-S
Bemessungsstrom der Schaltgerätekombination:	InA: 50A		
Bemessungsstoßspannungsfestigkeit:	Uimp: 4kV	Schutzklasse:	1 geerdet
Bemessungsisolationsspannung:	Ui: 230V	Schutzart:	IP44
Bemessungsbelastungsfaktor:	RDF: 0.6	Schranks-tiefe:	205mm
Bemessungsstoßstromfestigkeit:	Ipk: 7,56 kA	Farbe:	RAL7035
Bemessungskurzzeitstromfestigkeit:	Icw: 3,44 kA	Umgebungs-temperatur:	25°C
Bedingte Bemessungskurzschlußstromfestigkeit: (Ik3 nur bei Kurzschlußschutzeinrichtung (SCPD) in Einspeisung)	Icc: 0 kA		
Bemessungsschaltvermögen Leitungsschutzschalter:	6 kA		

Installationsverteiler, nach DIN EN 61439-1/-3




Für dieses Dokument und den darin dargestellten Inhalt behalten wir uns alle Rechte vor. Die Vervielfältigung des Inhaltes ist ohne unsere ausdrückliche Zustimmung nicht gestattet.


3			Angebotsnr.	A2024-2543	Projektname: SEGRO Park Düsseldorf Flingern	 EtecProjekt + Bau GmbH	Index: a
2			Datum	27.03.2025			= LI03
1			Erstellt	Schwarte Kevin			+ UV OG Unit (LI03)
Änderung	Änderungsdatum	Geändert	Bestätigt	Thiele Christian	Deckblatt		Blatt: 1 / 6
Massstab: 1	Ik3: 0 kA	Ik1: 0 kA	TN-S				

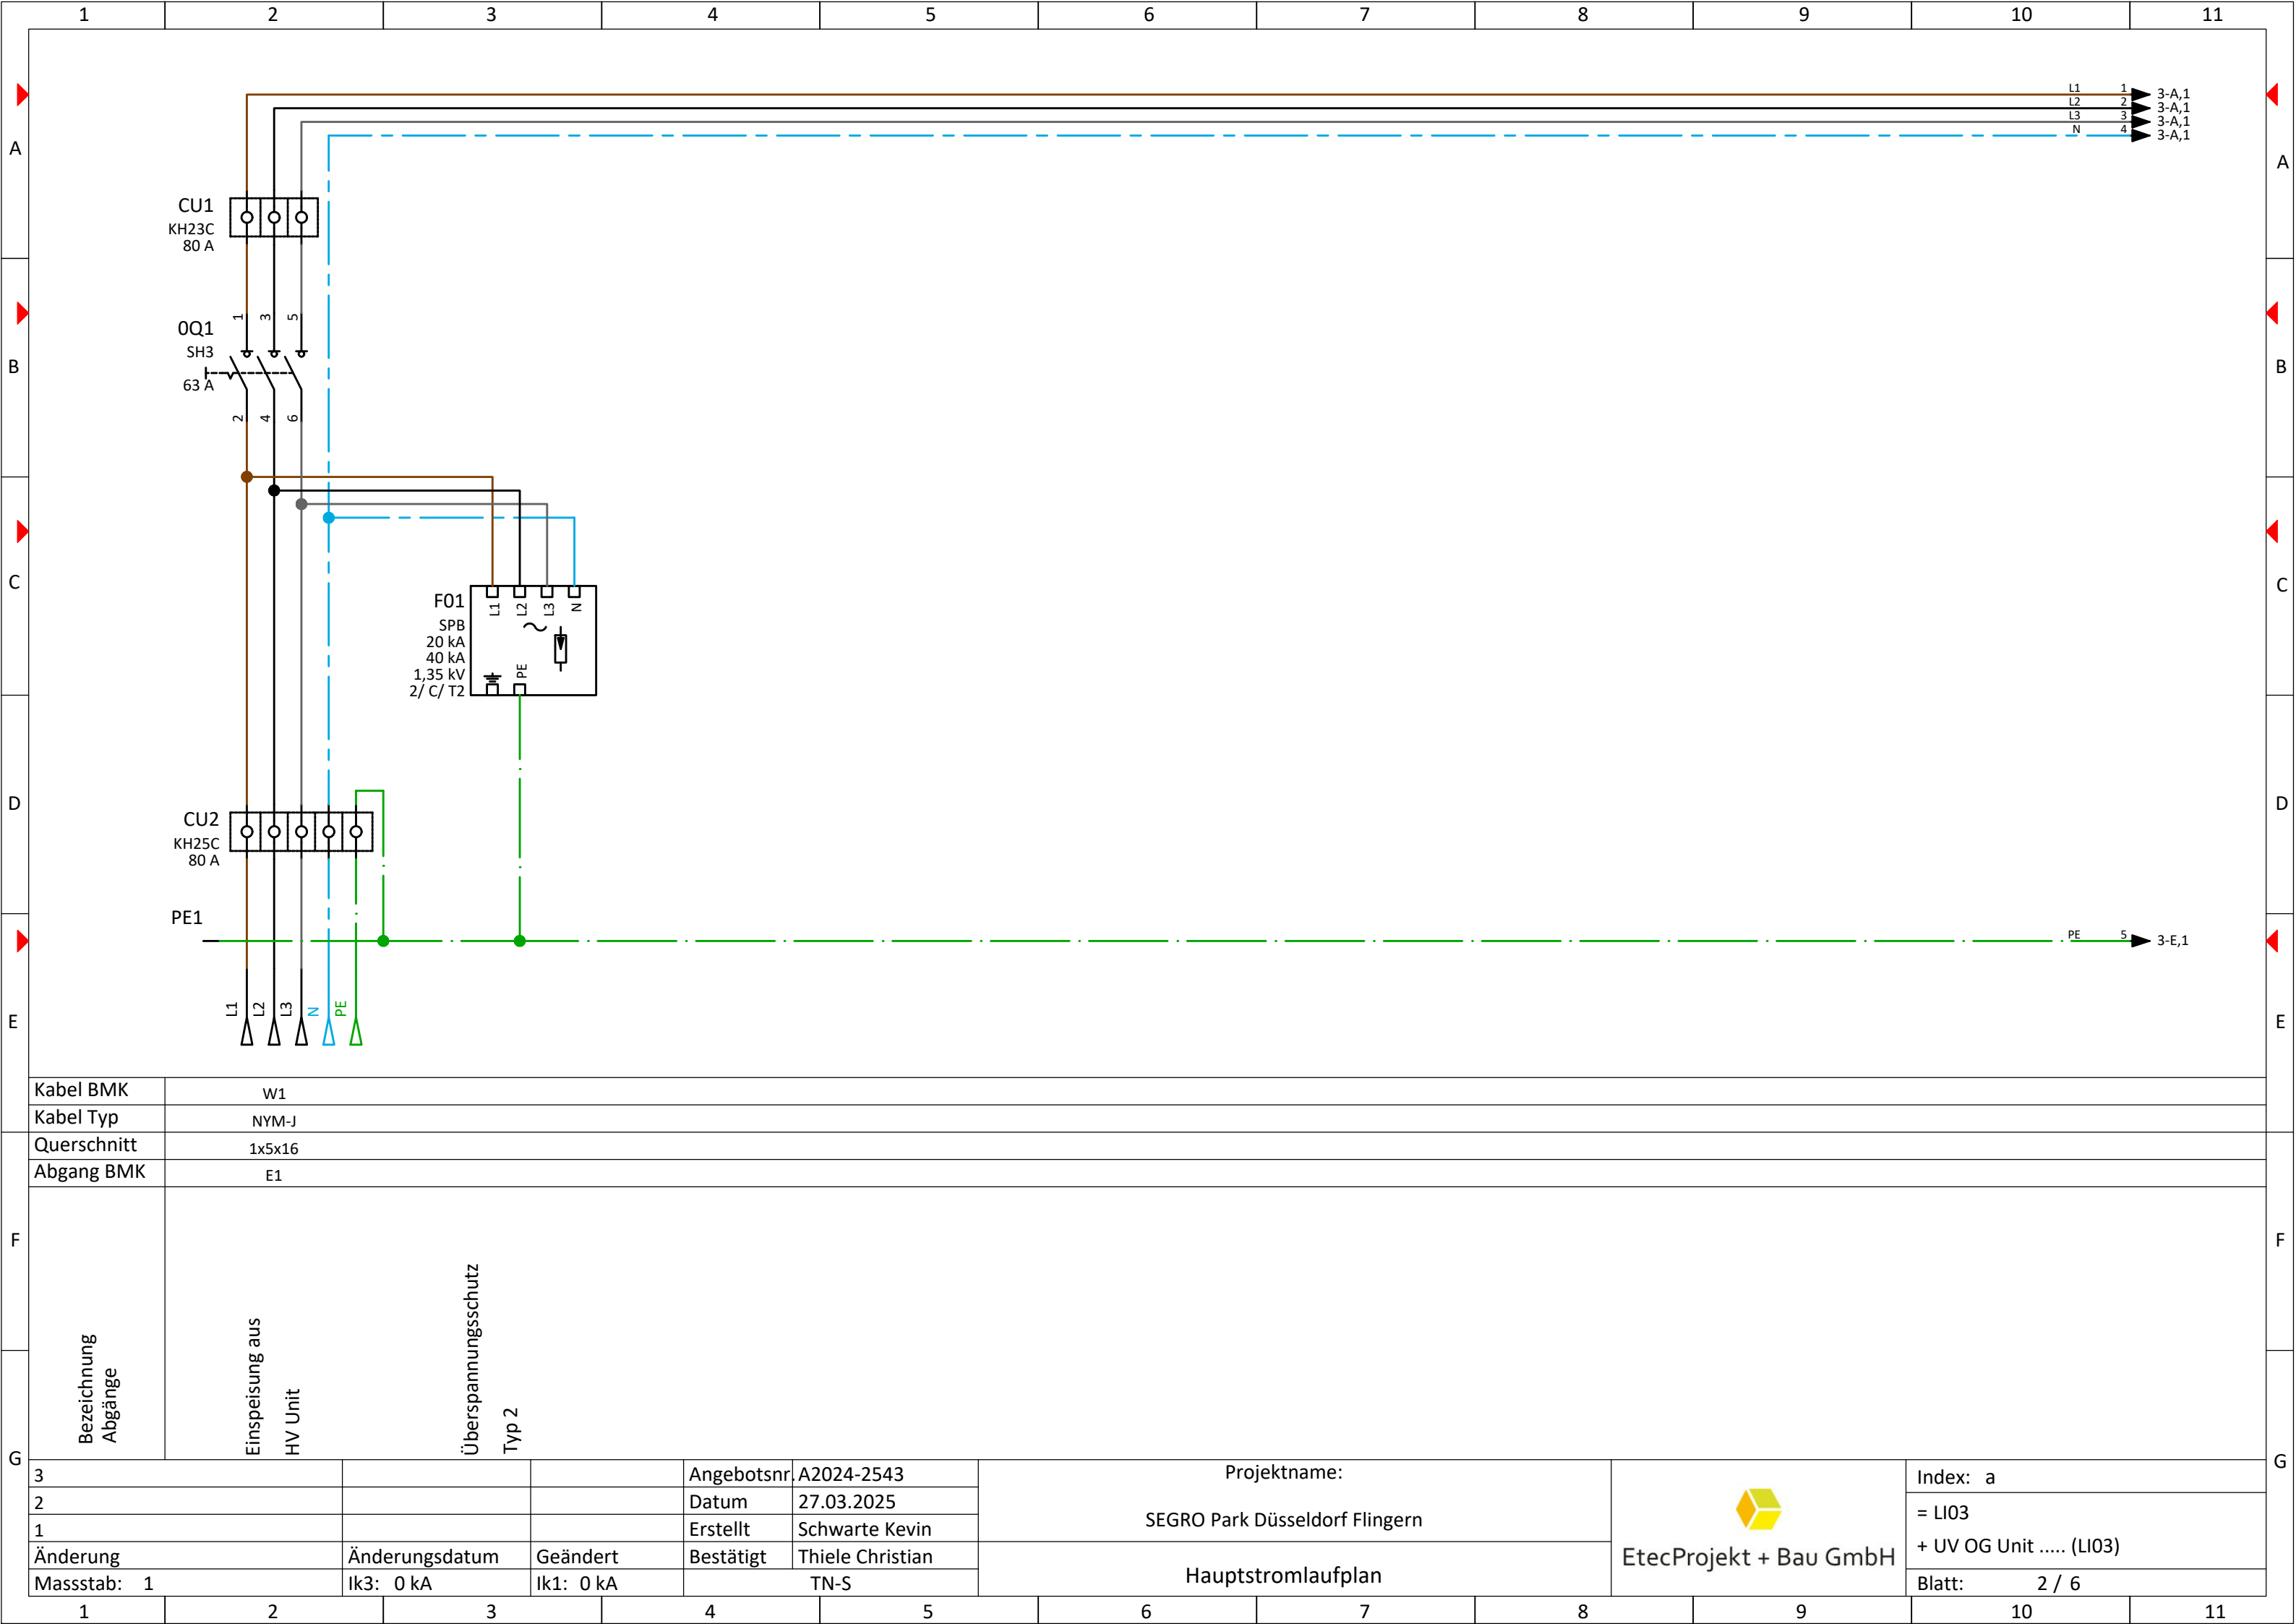

Kabel BMK		W1									
Kabel Typ		NYM-J									
Querschnitt		1x5x16									
Abgang BMK		E1									
Bezeichnung Abgänge		Einspeisung aus HV Unit Überspannungsschutz Typ 2									
3				Angebotsnr.	A2024-2543	Projektname: SEGRO Park Düsseldorf Flingern		 EtecProjekt + Bau GmbH	Index: a		
2				Datum	27.03.2025				= LI03		
1				Erstellt	Schwarte Kevin				+ UV OG Unit (LI03)		
Änderung		Änderungsdatum	Geändert	Bestätigt	Thiele Christian	Hauptstromlaufplan			Blatt: 2 / 6		
Massstab: 1		Ik3: 0 kA	Ik1: 0 kA	TN-S							



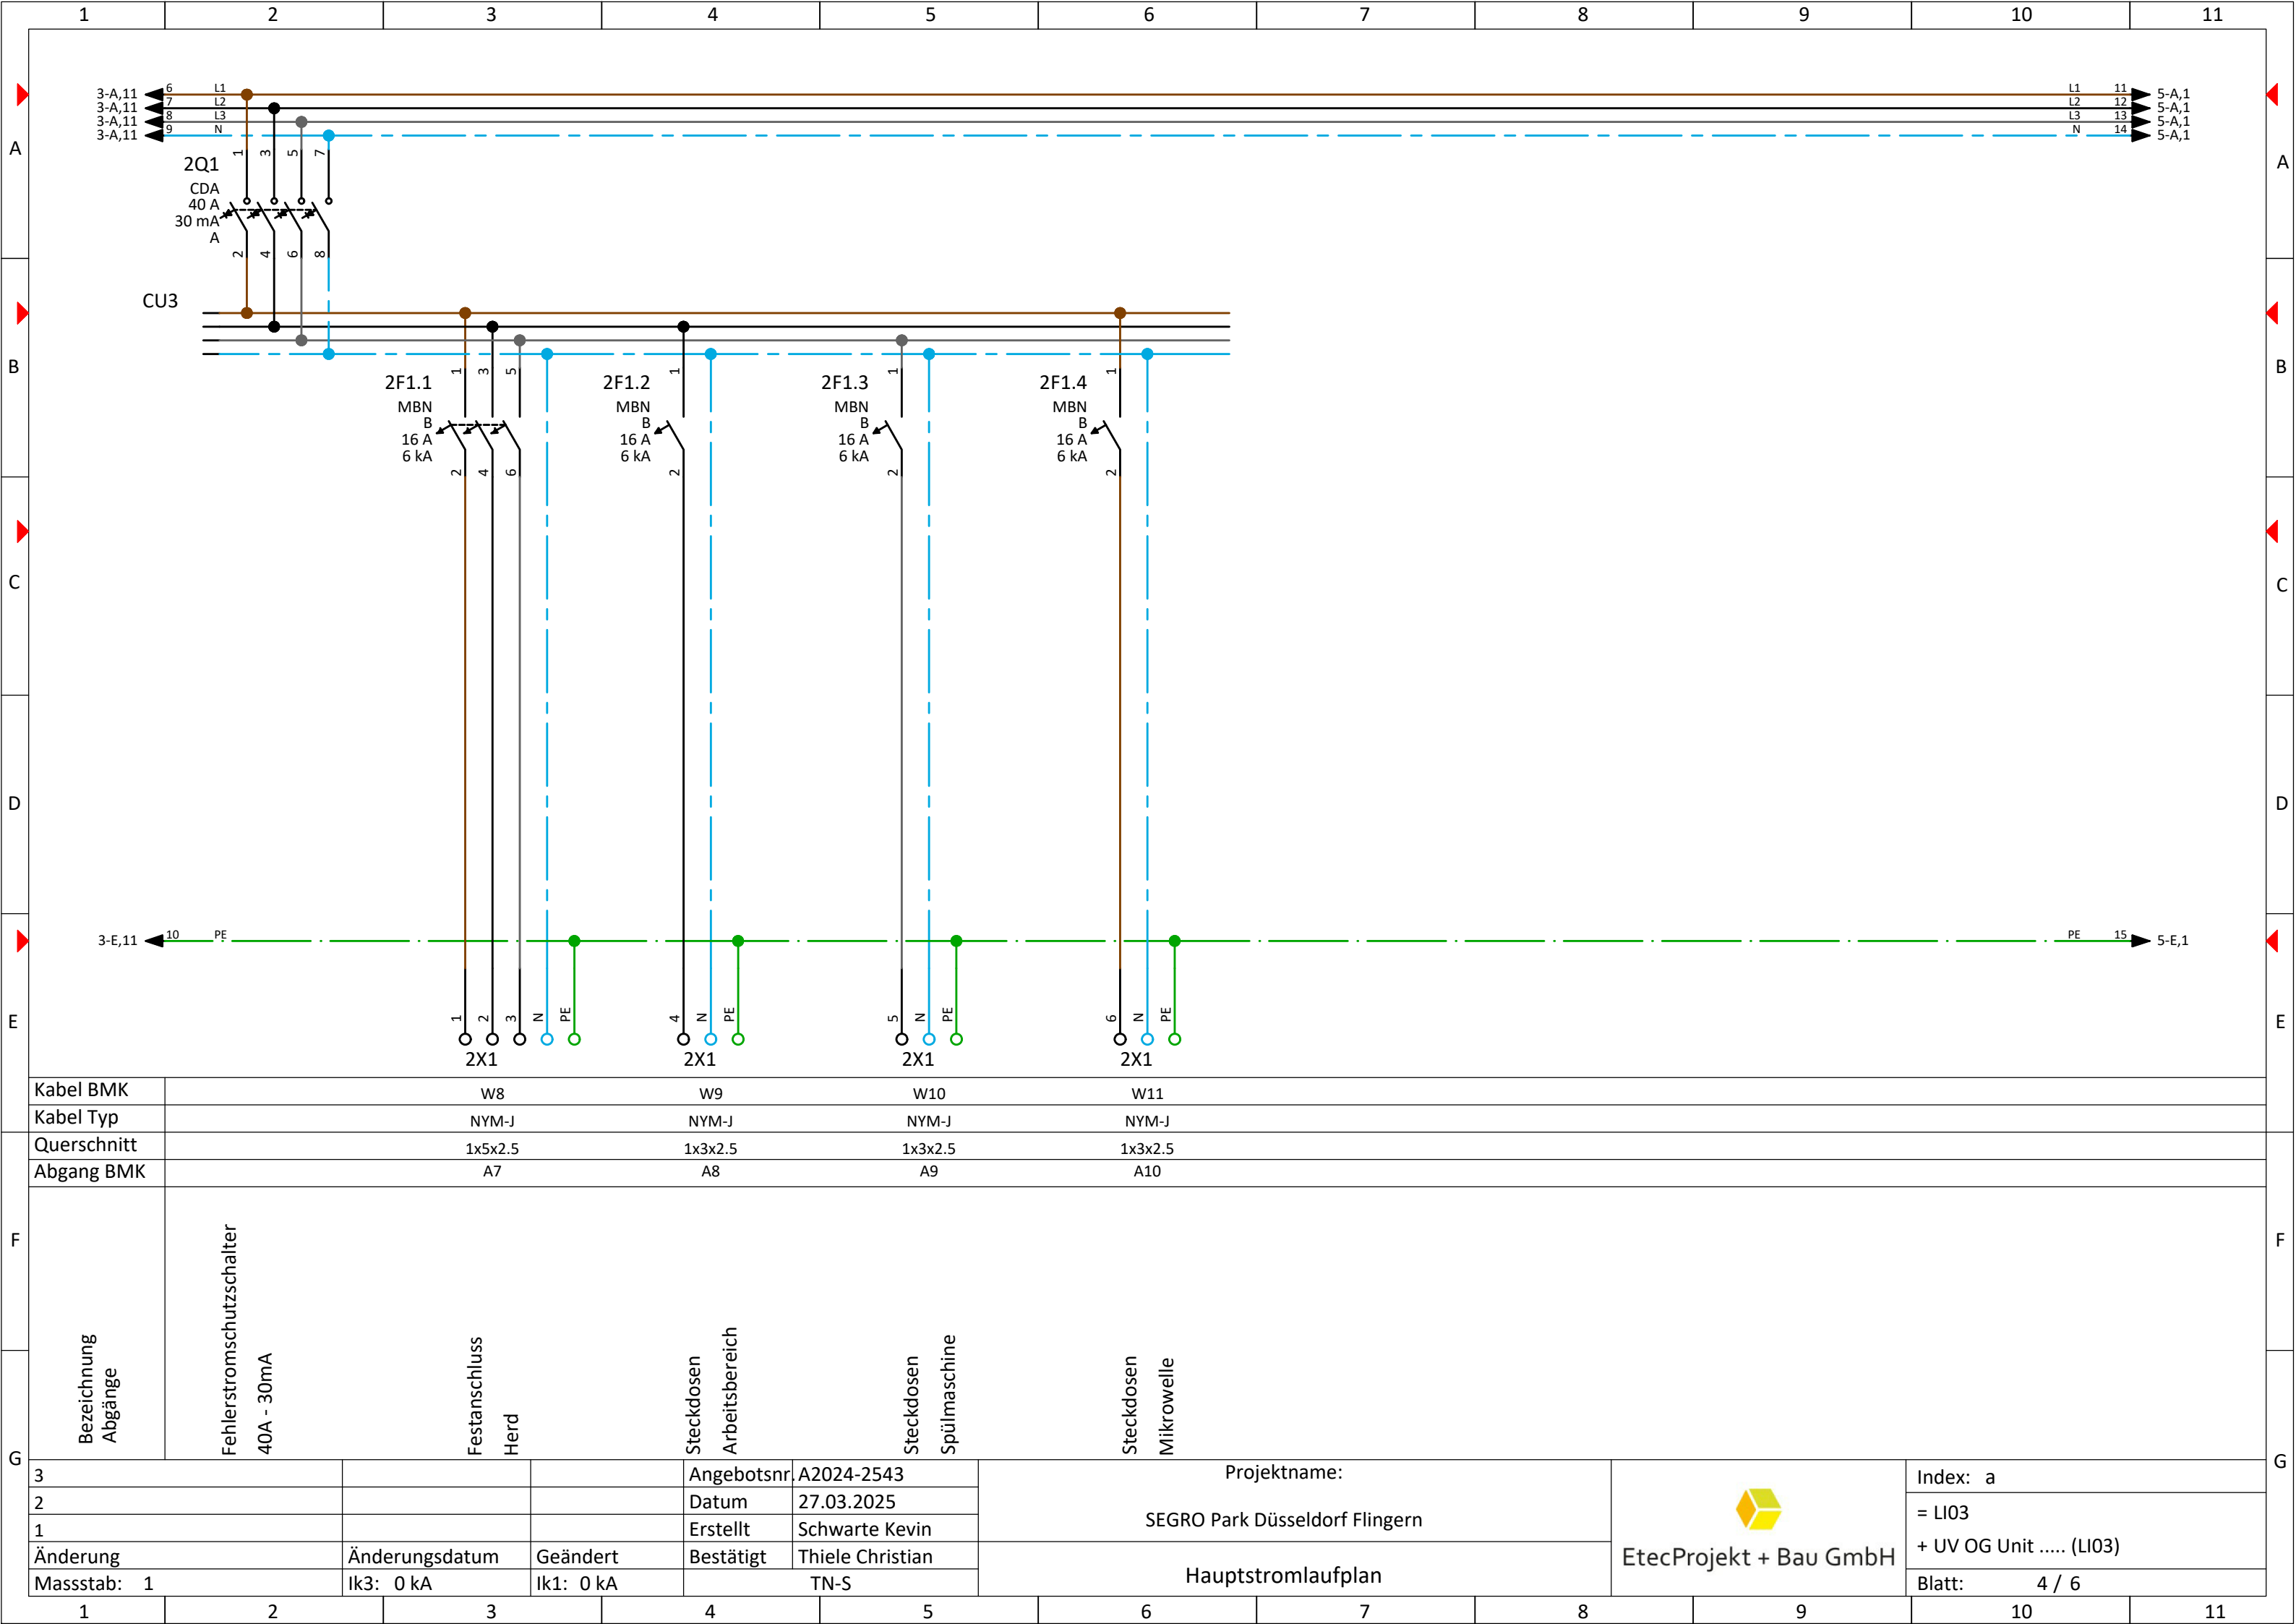


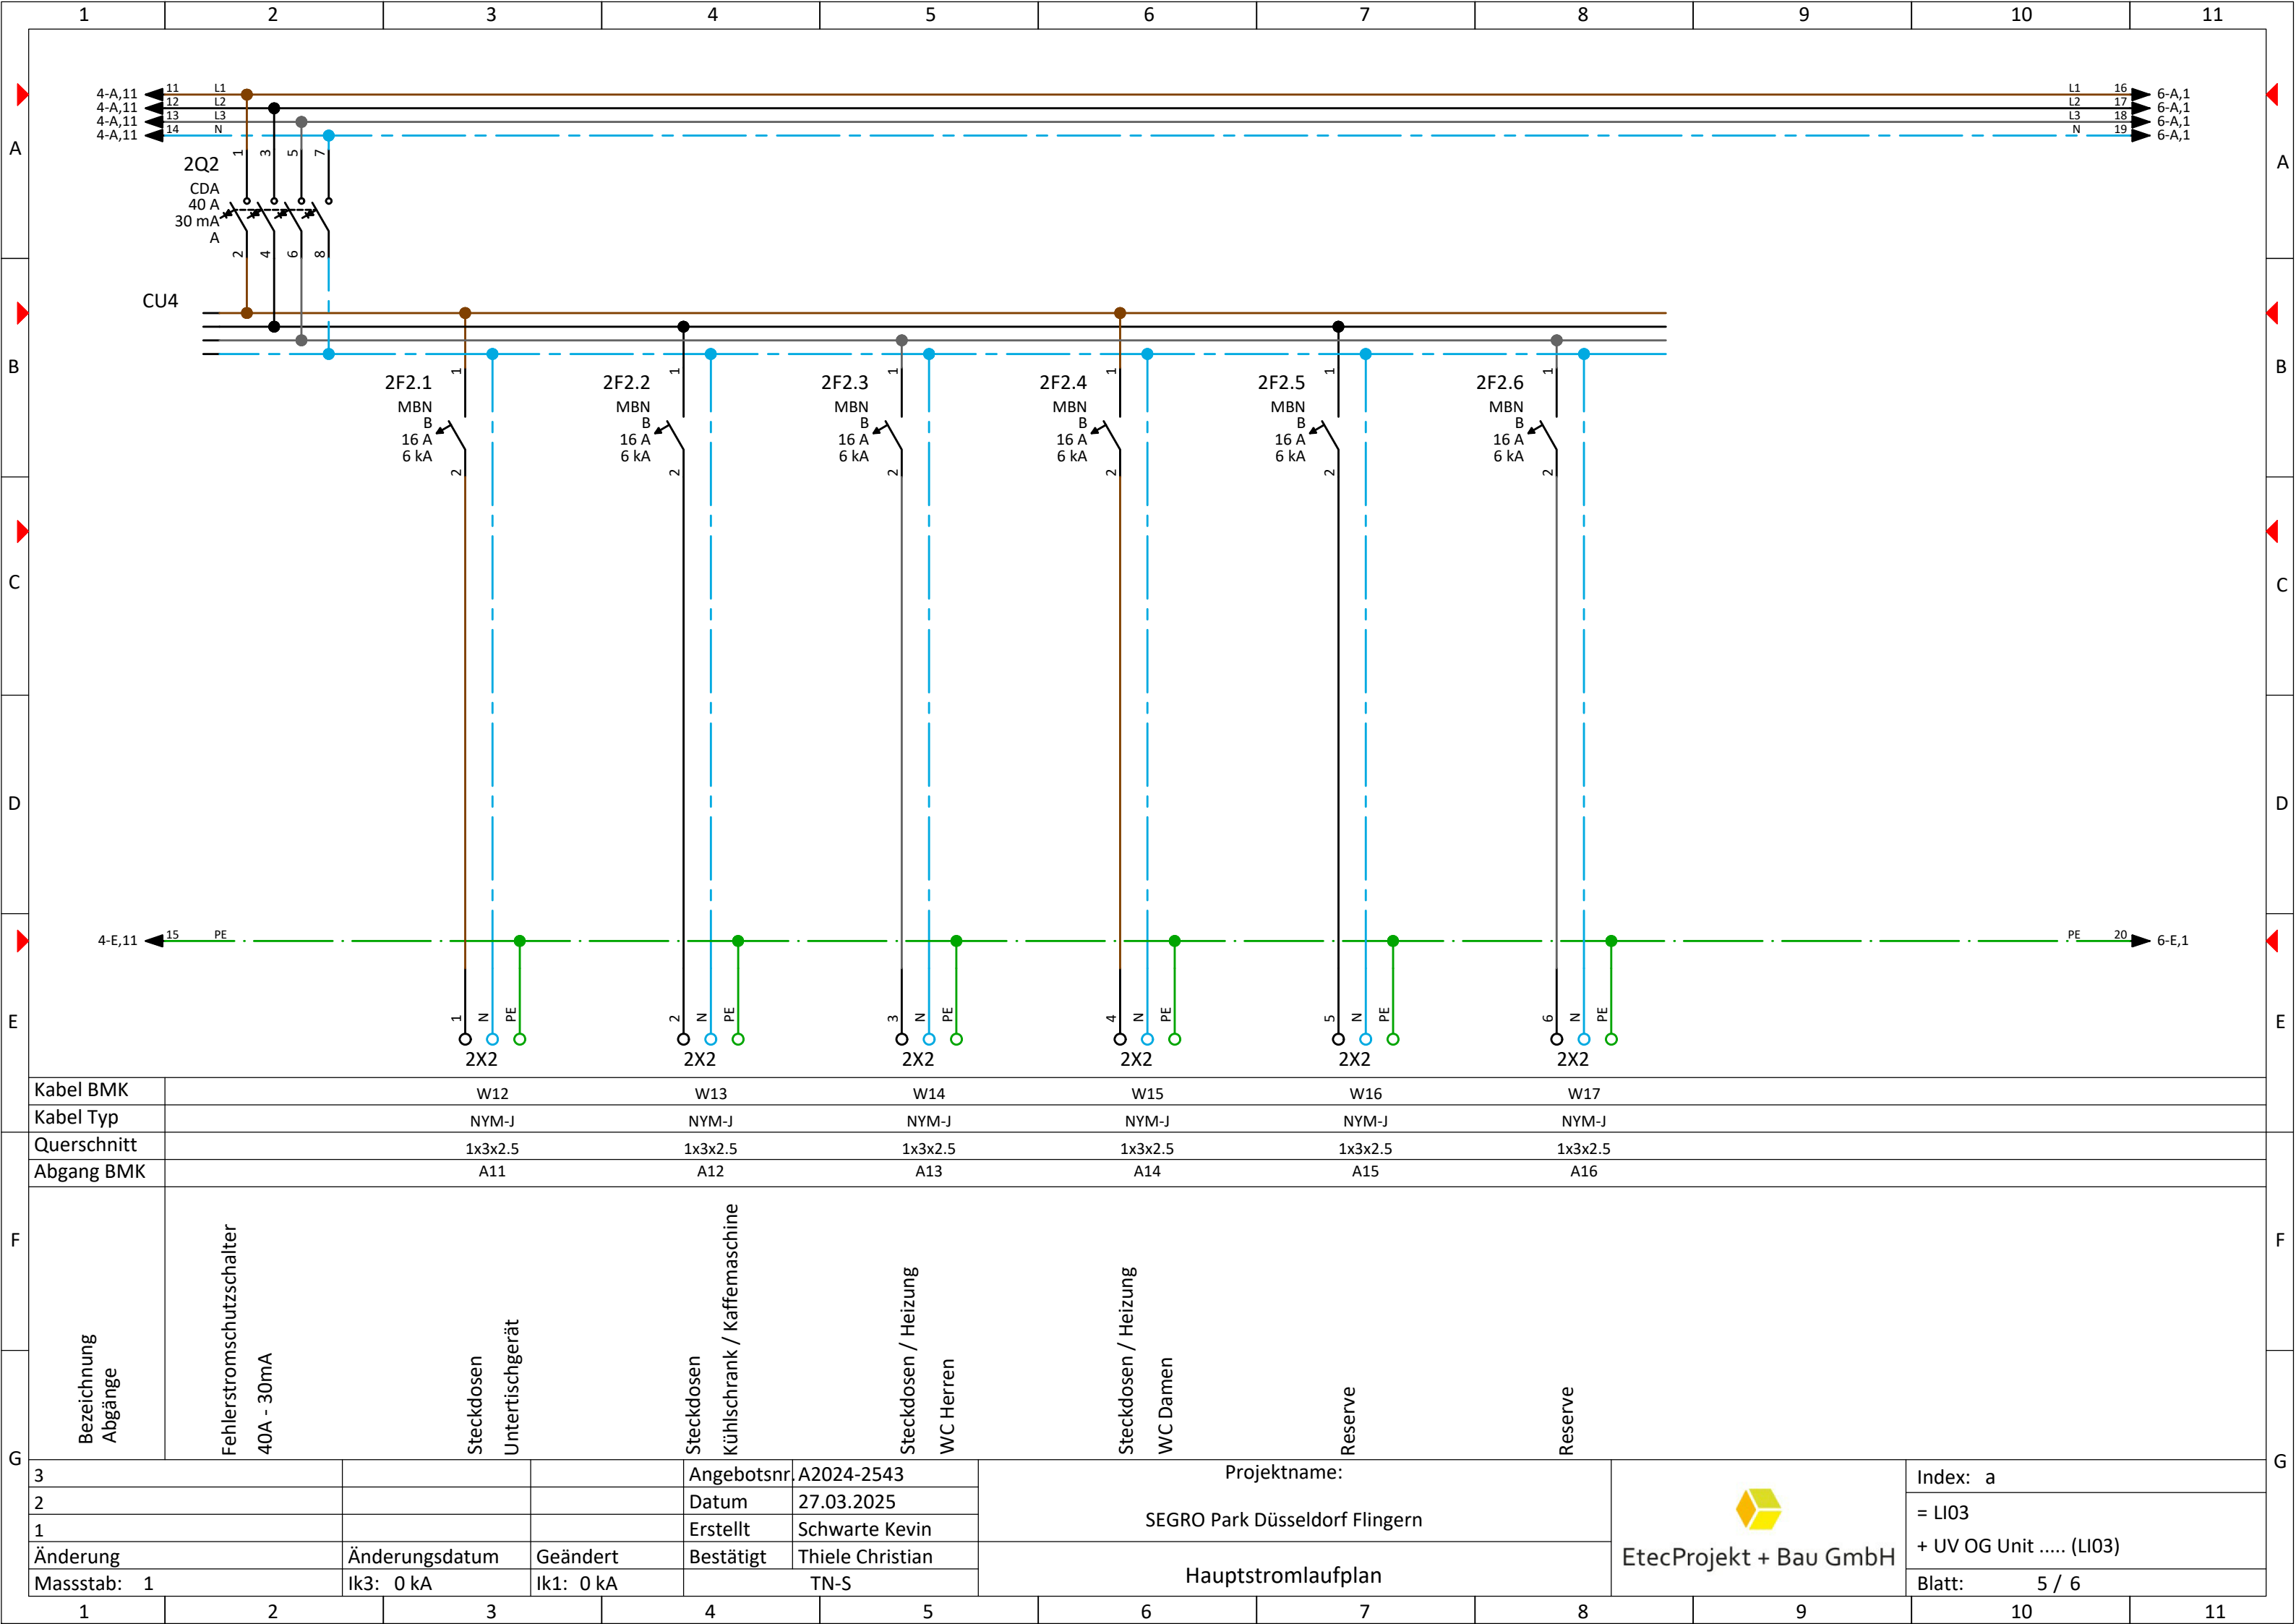



Kabel BMK	W12	W13	W14	W15	W16	W17
Kabel Typ	NYM-J	NYM-J	NYM-J	NYM-J	NYM-J	NYM-J
Querschnitt	1x3x2.5	1x3x2.5	1x3x2.5	1x3x2.5	1x3x2.5	1x3x2.5
Abgang BMK	A11	A12	A13	A14	A15	A16

Bezeichnung Abgänge	Fehlerstromschutzschalter 40A - 30mA	Steckdosen Untertischgerät	Steckdosen Kühlschrank / Kaffeemaschine	Steckdosen / Heizung WC Herren	Steckdosen / Heizung WC Damen	Reserve	Reserve
---------------------	--------------------------------------	----------------------------	---	--------------------------------	-------------------------------	---------	---------

3			Angebotsnr.	A2024-2543	Projektname: SEGRO Park Düsseldorf Flingern	 EtecProjekt + Bau GmbH	Index: a
2			Datum	27.03.2025			= LI03
1			Erstellt	Schwarte Kevin			+ UV OG Unit (LI03)
Änderung	Änderungsdatum	Geändert	Bestätigt	Thiele Christian	Hauptstromlaufplan		Blatt: 5 / 6
Massstab: 1	Ik3: 0 kA	Ik1: 0 kA	TN-S				

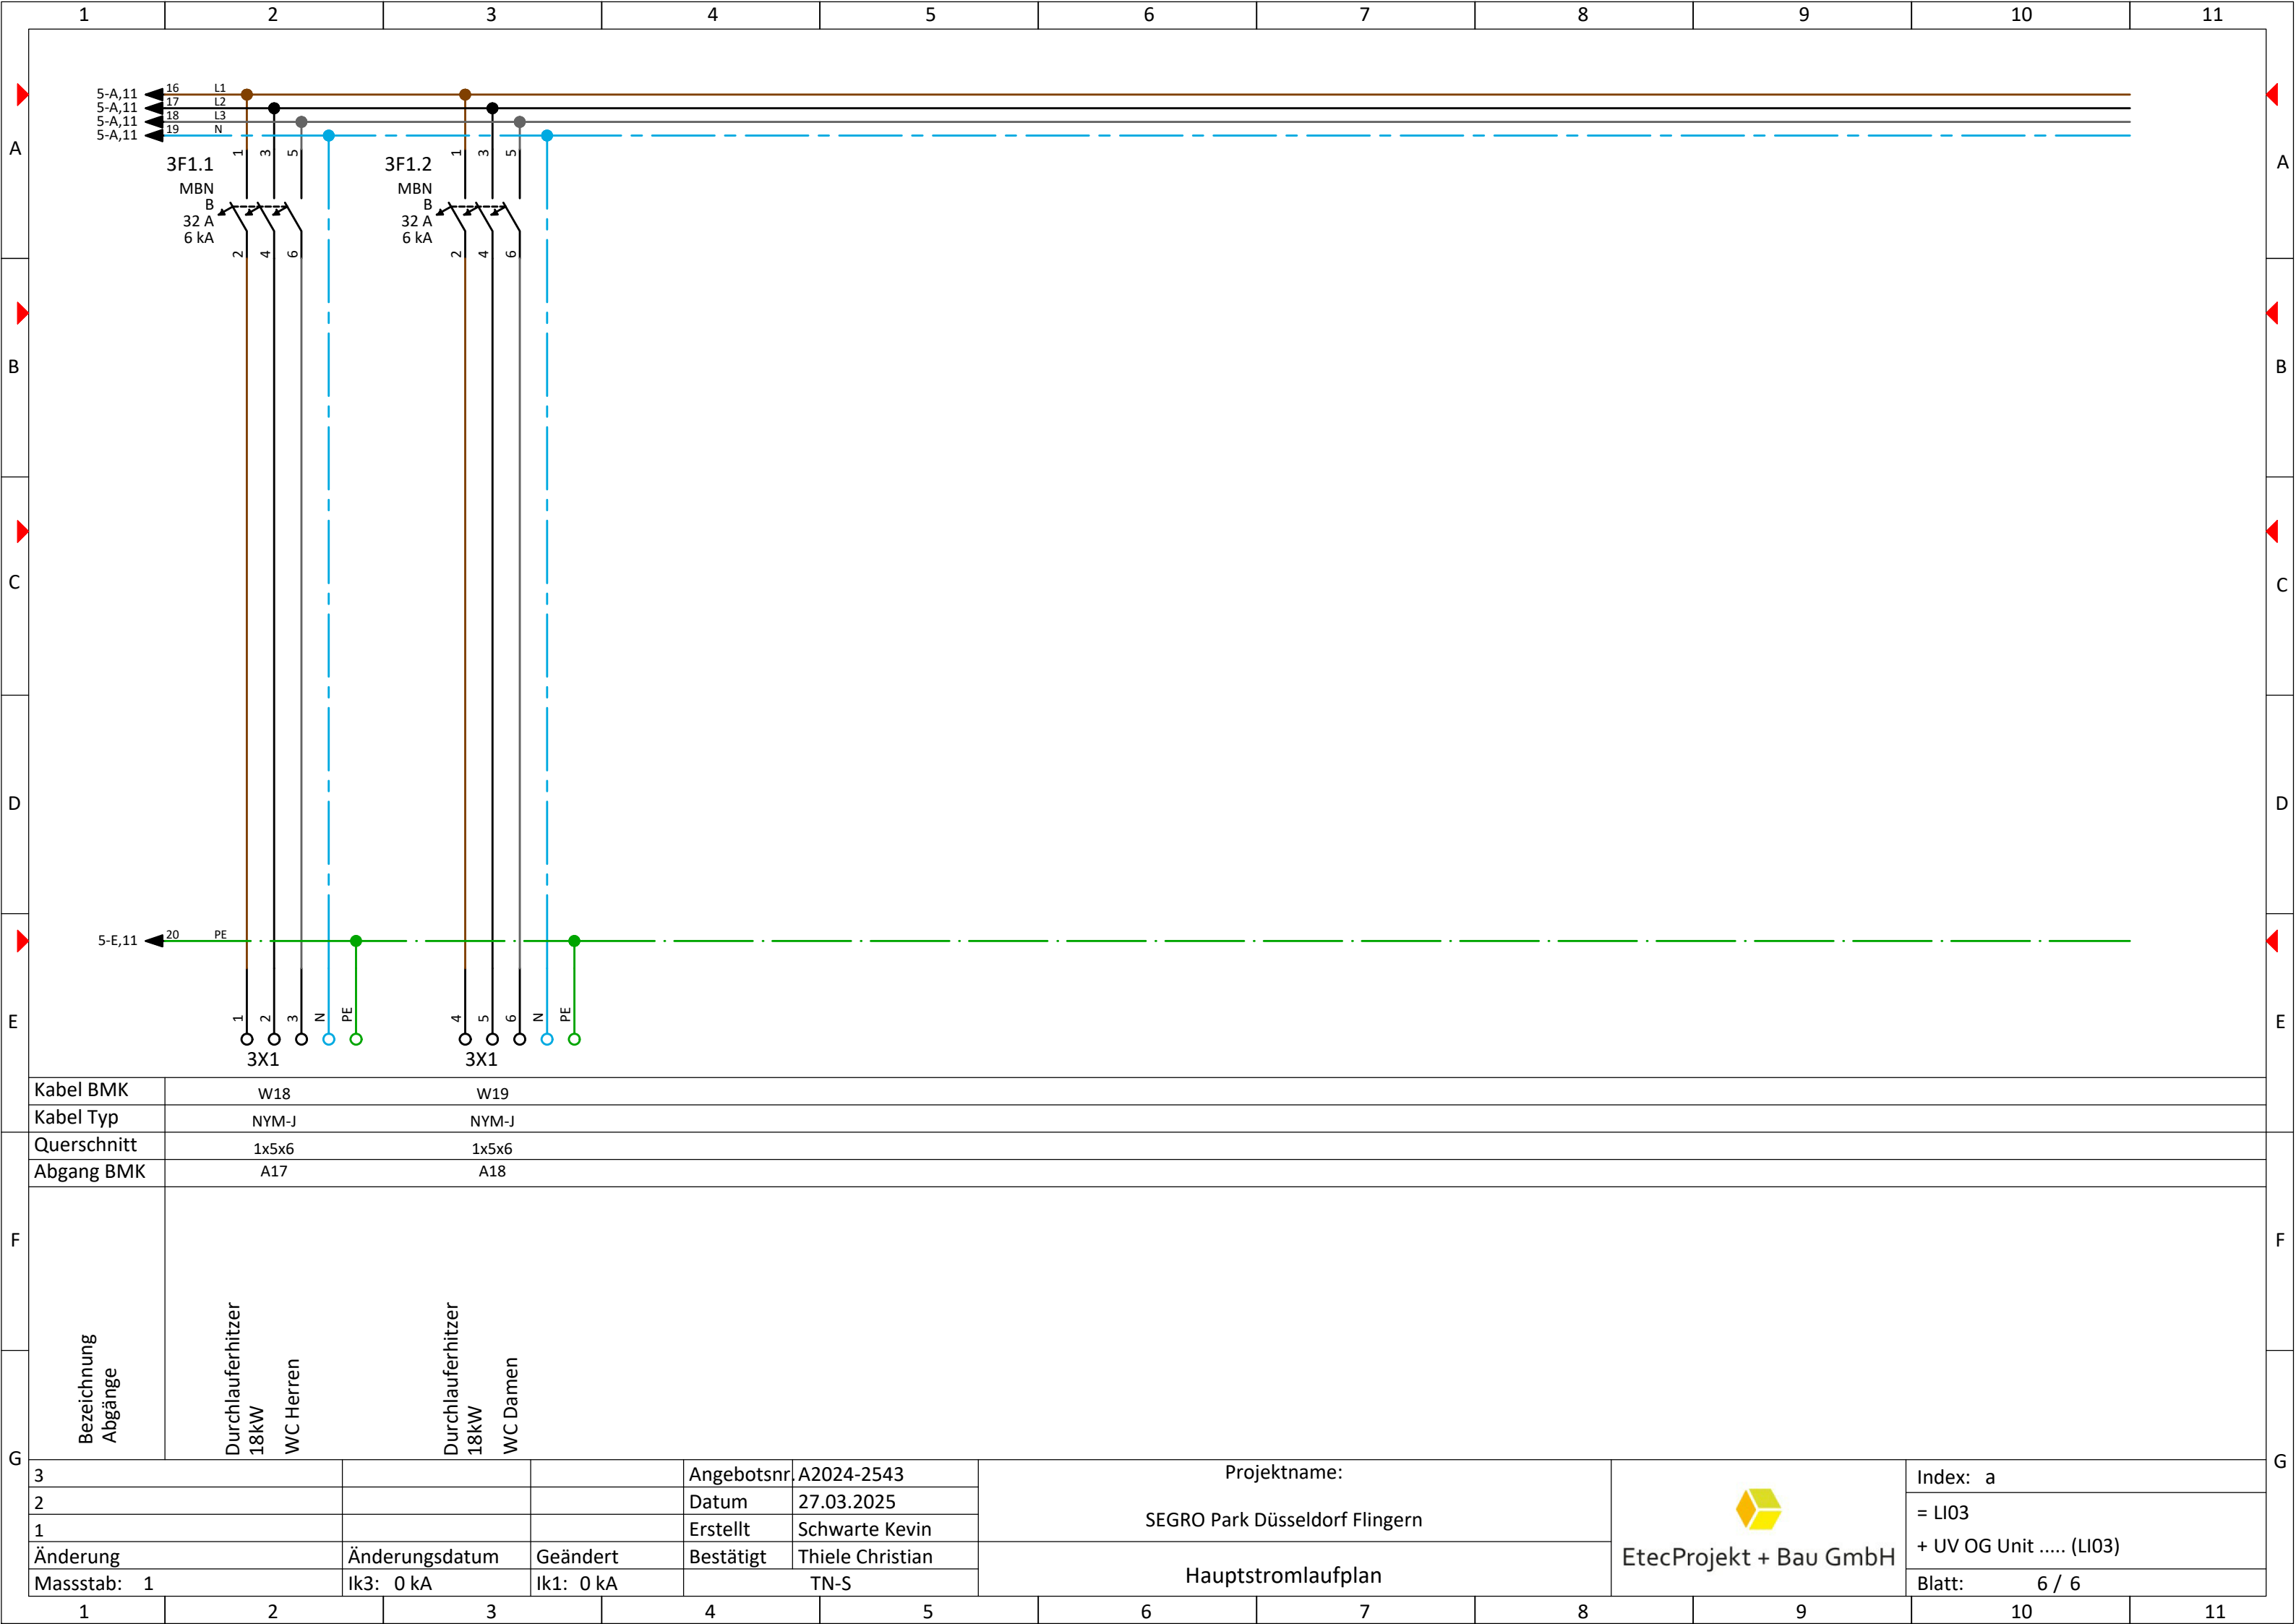

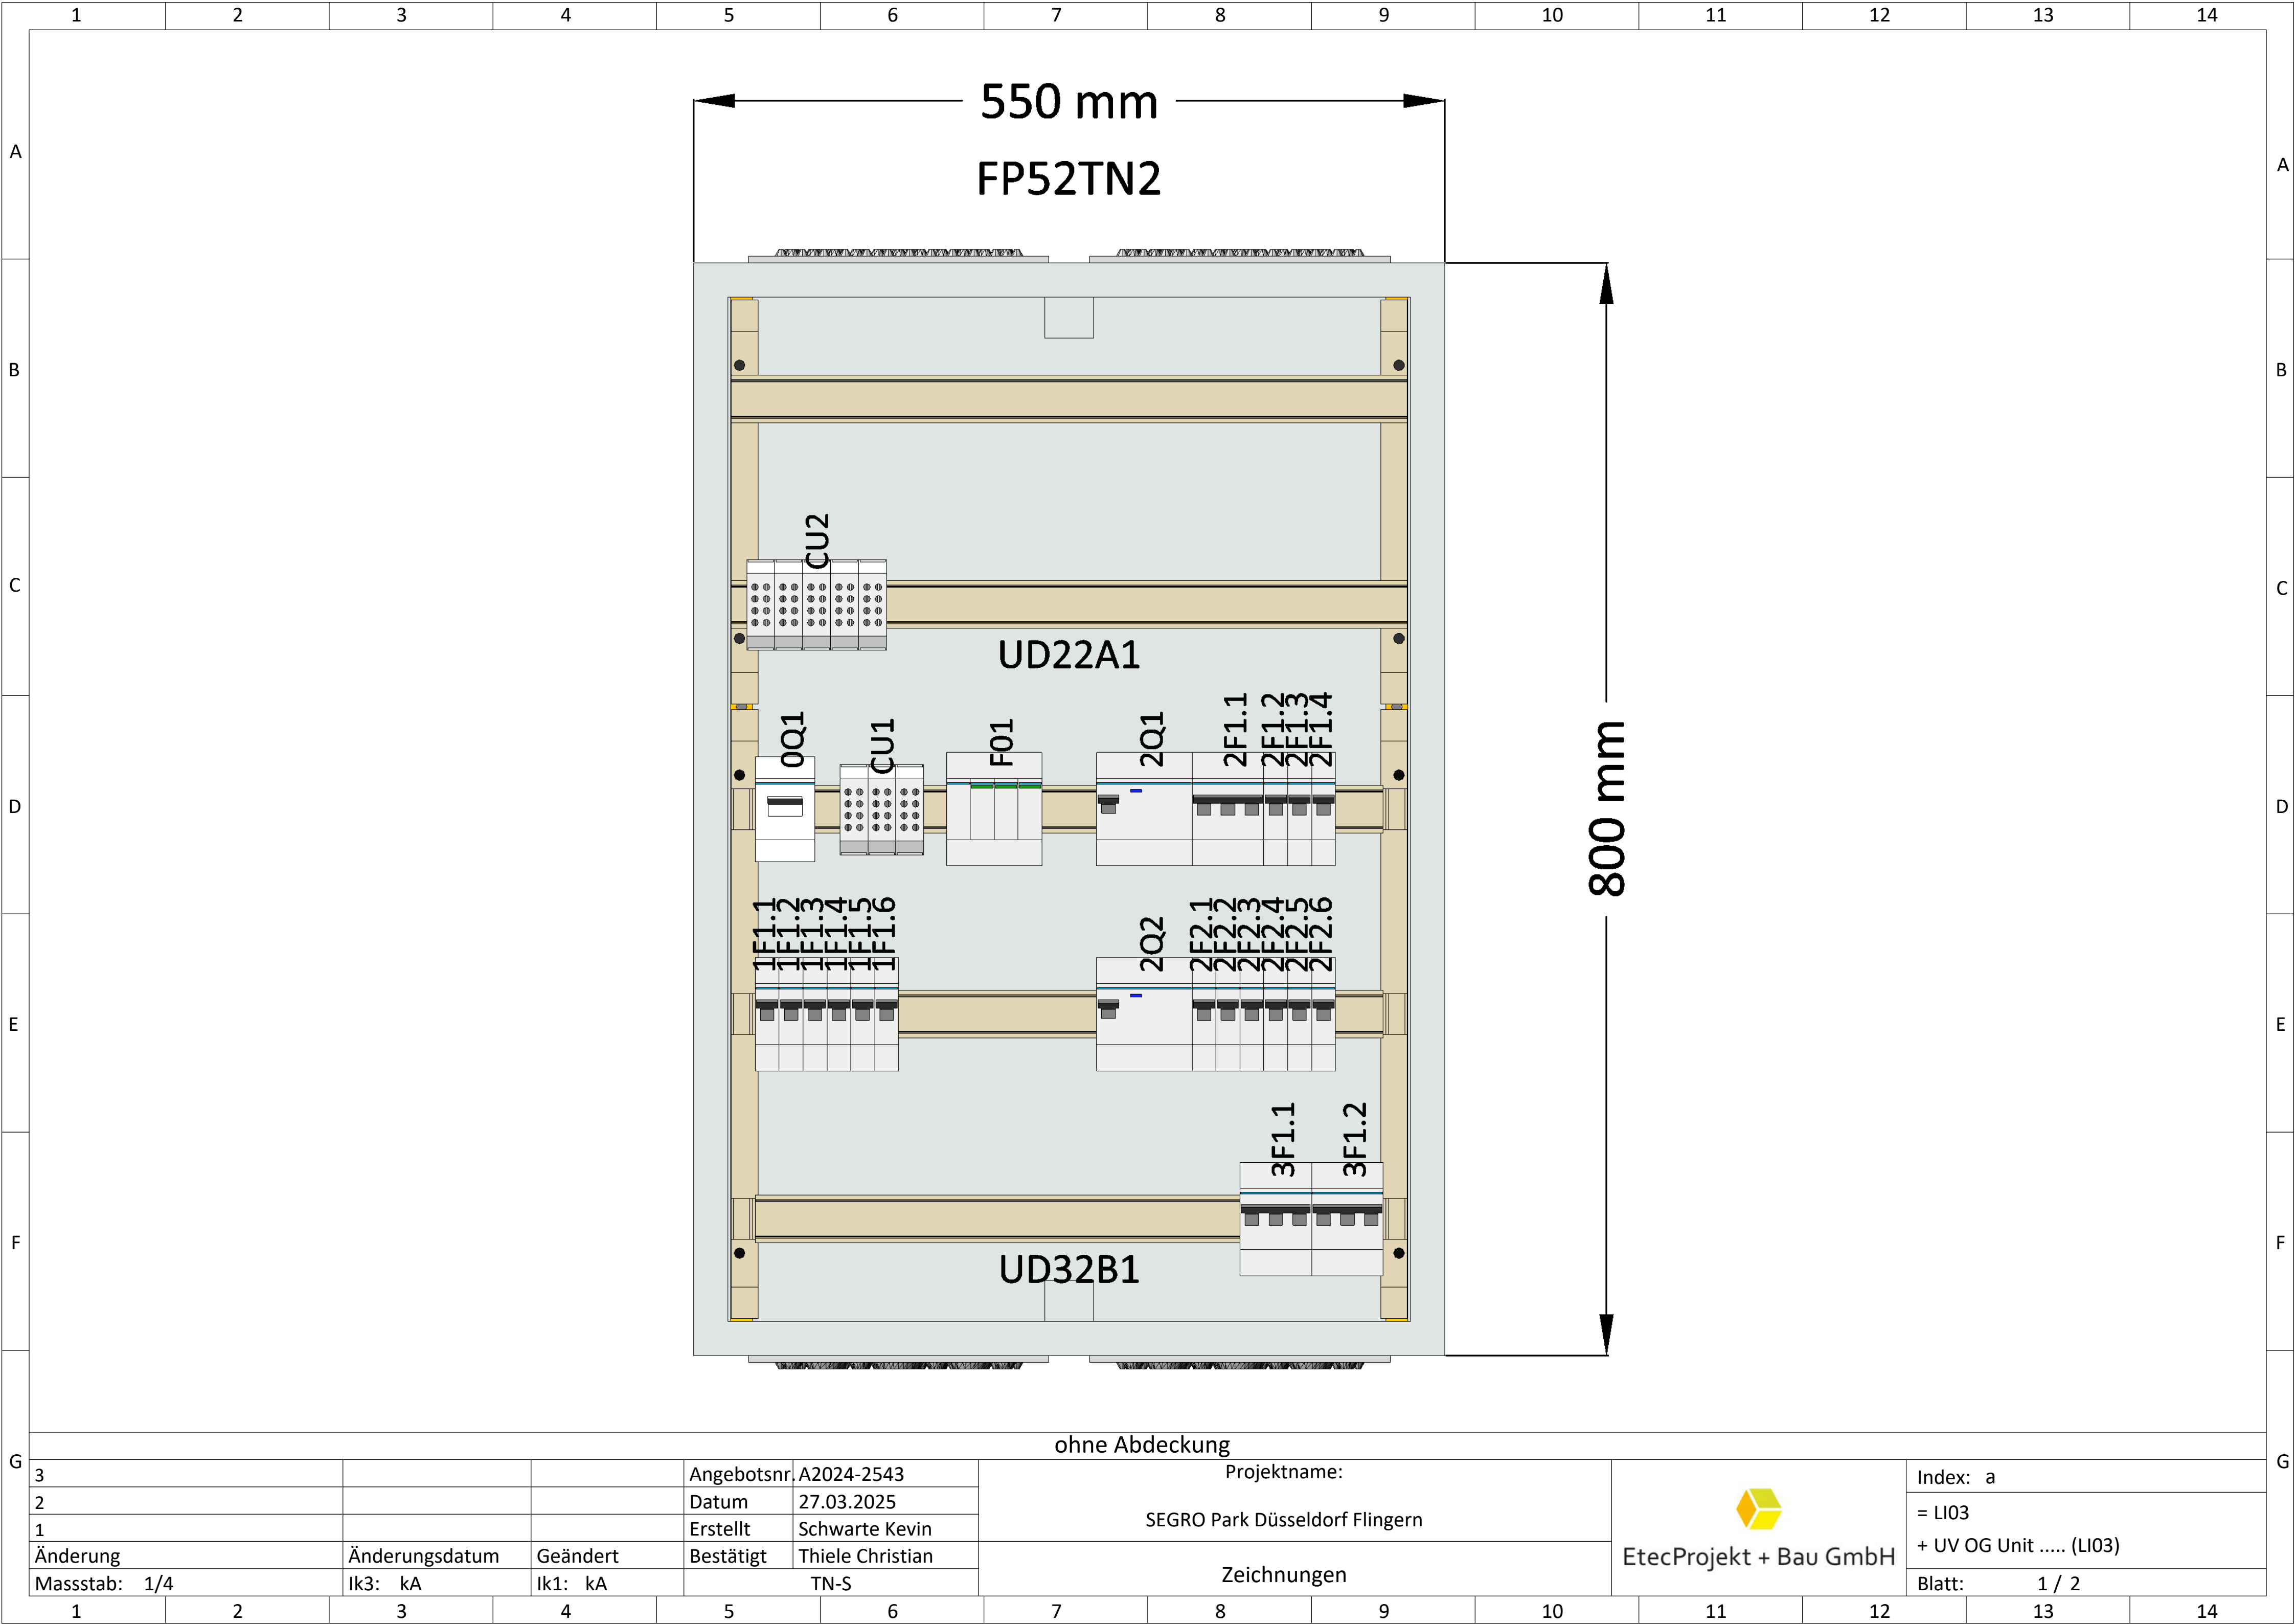

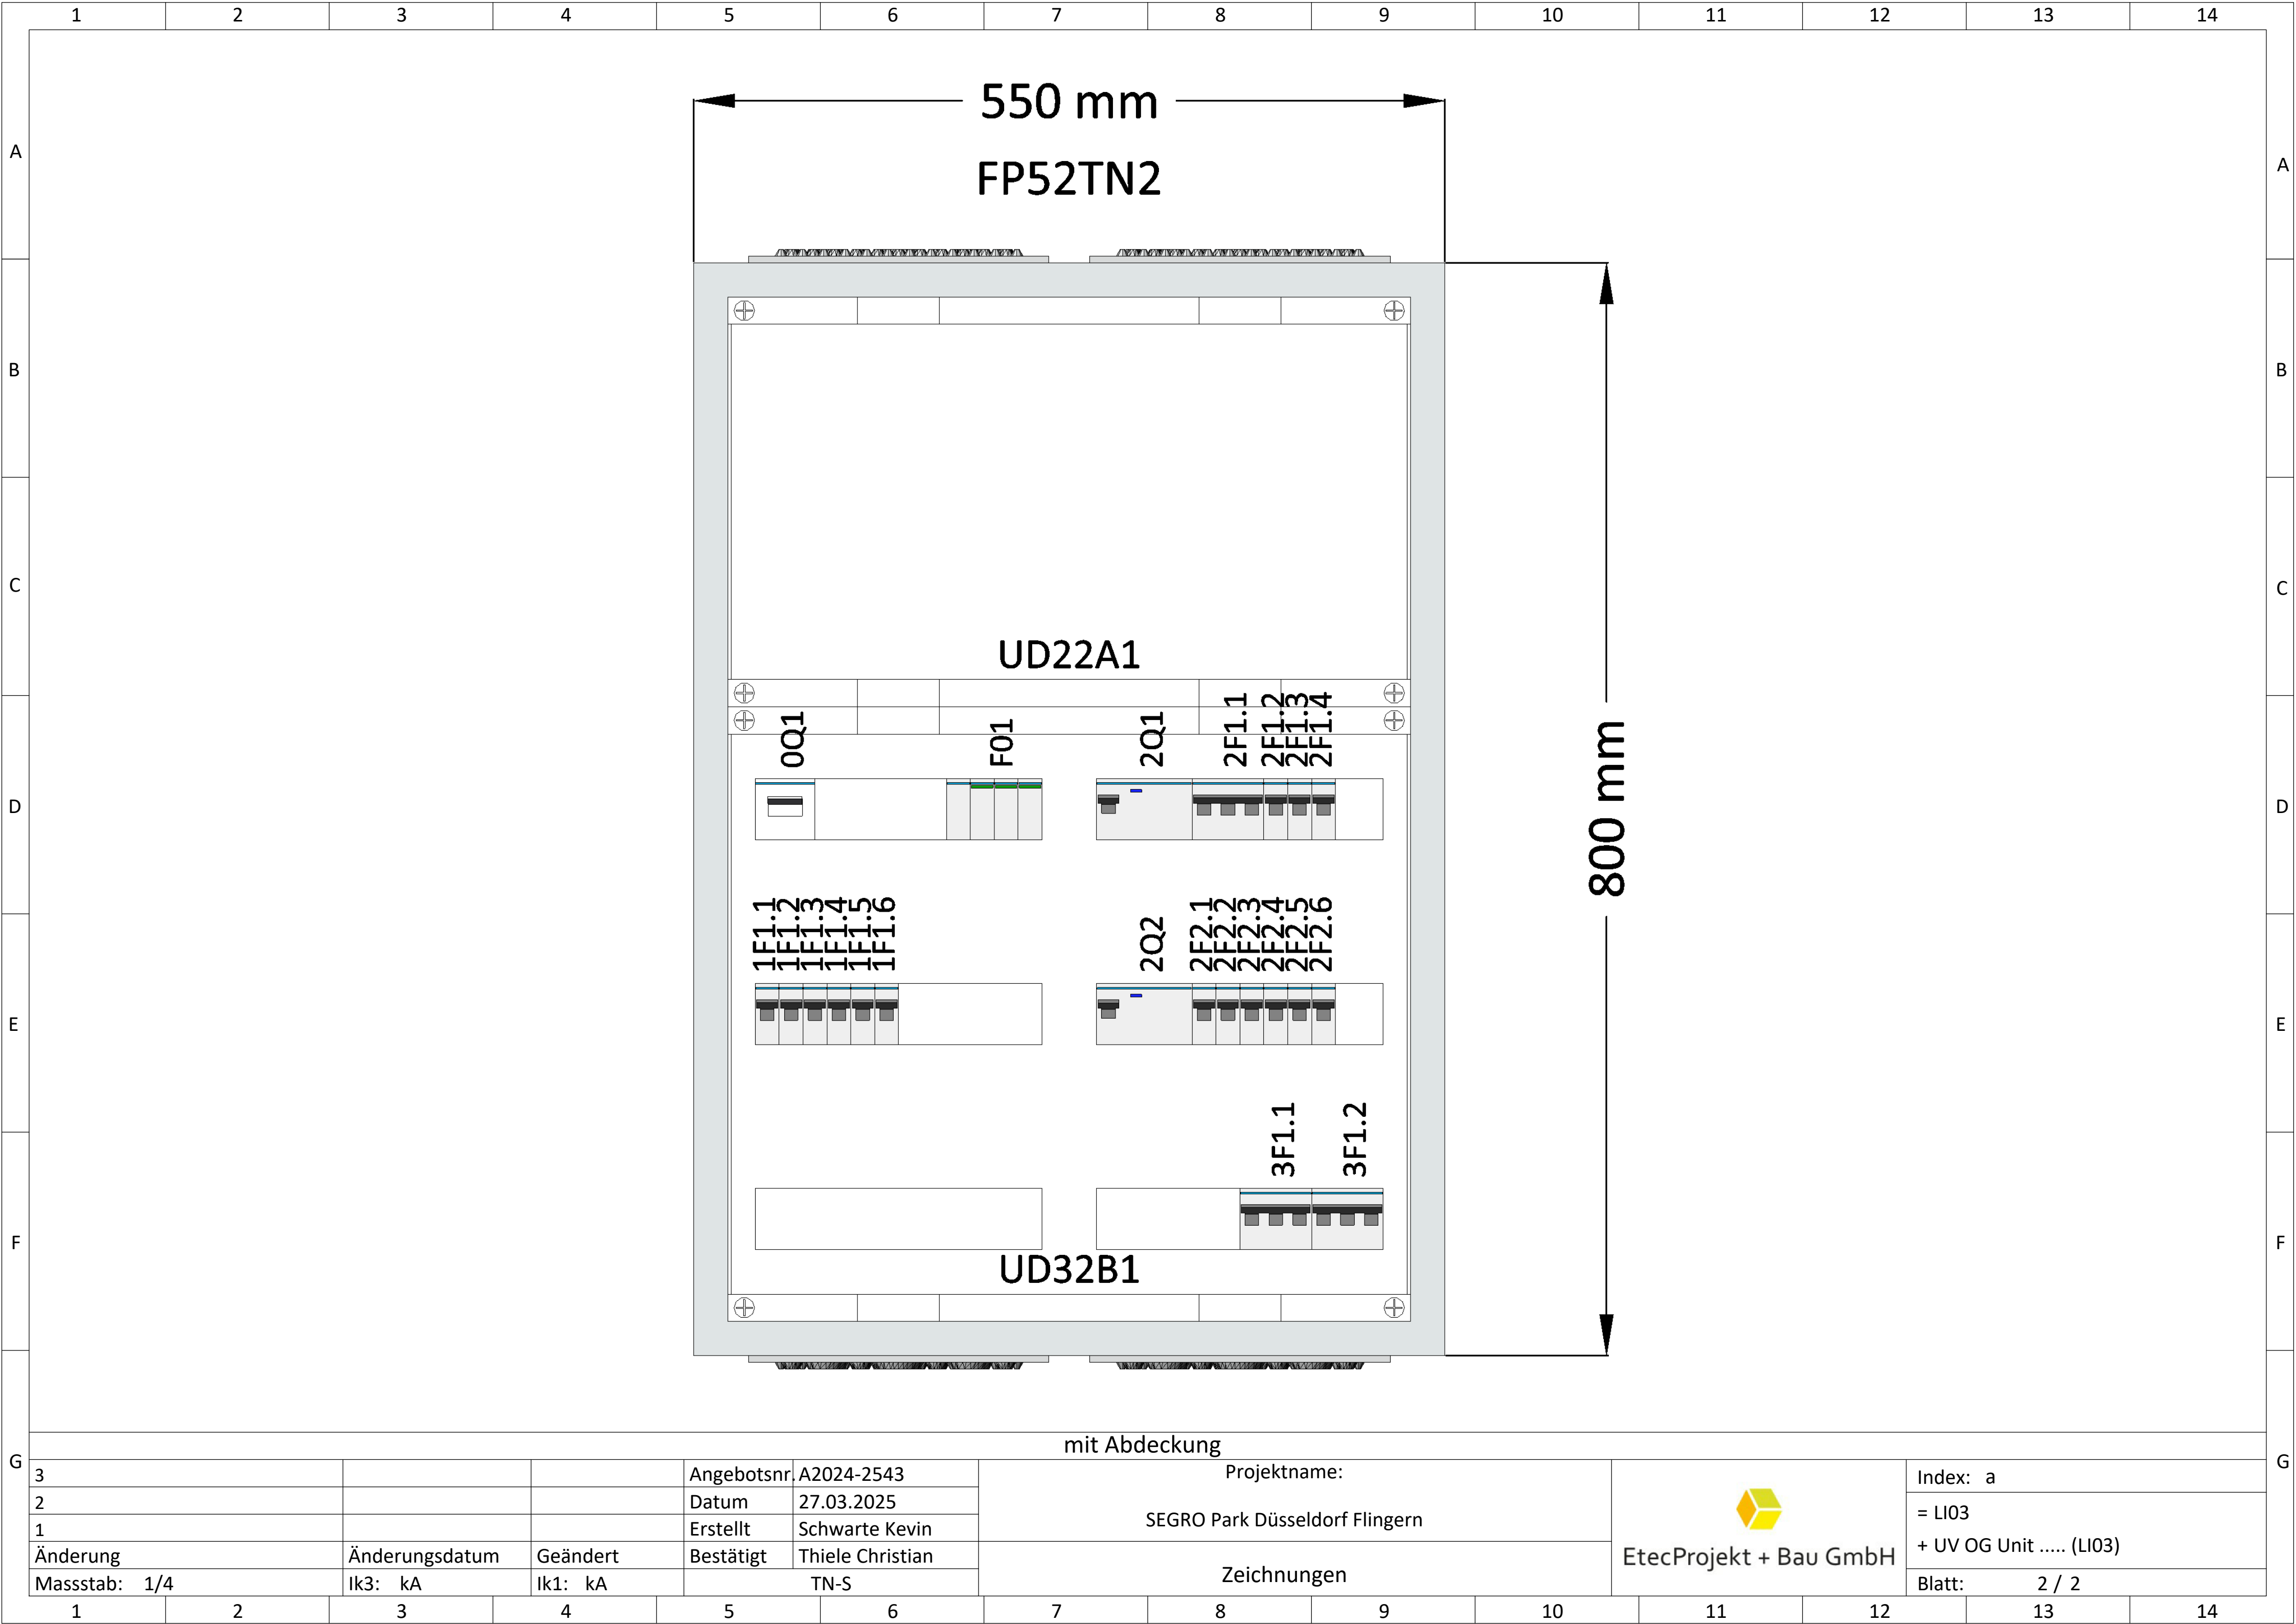

G	mit Abdeckung														G												
	3						Angebotsnr.	A2024-2543		Projektname: SEGRO Park Düsseldorf Flingern				 EtecProjekt + Bau GmbH		Index: a											
	2						Datum	27.03.2025								= LI03											
	1						Erstellt	Schwarte Kevin								+ UV OG Unit (LI03)											
	Änderung		Änderungsdatum		Geändert		Bestätigt	Thiele Christian		Zeichnungen						Blatt: 2 / 2											
	Massstab: 1/4		Ik3: kA		Ik1: kA		TN-S																				
1		2		3		4		5		6		7		8		9		10		11		12		13		14	