

EtecProjekt+Bau GmbH
Heinrich-Hertz-Straße 22a
40699 Erkrath

021121023300 info@etecprojekt.de

SCHALTSCHRANKBAU CE
NICHT REVIDIERT!

Projektname: SEGRO Park Düsseldorf Flingern
Kom-Nr./Angebots-NR.: A2024-2543 Ausführungsplan
Bezeichnung Ort: UV OG Unit (UL01)
Auftragsnummer: AB2024-1049 Klemmenfabrikat:
Baujahr: 05 / 2025 WAGO / HAGER

Farbkennzeichnung der Leiter (in Anlehnung an VDE0113 Teil1):	
Außenleiter:	schwarz
Neutralleiter:	hellblau
Steuerspannung 230V AC:	rot
Steuerspannung 24V DC:	dunkelblau
Steuerspannung 24V AC:	braun
Fremdspannung:	orange
Messung:	weiss
Sensorleitung:	violett

Technische Daten der Schaltgerätekombination:


Bemessungsbetriebsspannung / -Frequenz:	Un: 400V / 50Hz	Netzform:	TN-S
Bemessungsstrom der Schaltgerätekombination:	InA: 50A		
Bemessungsstoßspannungsfestigkeit:	Uimp: 4kV	Schutzklasse:	1 geerdet
Bemessungsisolationsspannung:	Ui: 230V	Schutzart:	IP44
Bemessungsbelastungsfaktor:	RDF: 0.6	Schranktiefe:	205mm
Bemessungsstoßstromfestigkeit:	Ipk: 7,56 kA	Farbe:	RAL7035
Bemessungskurzzeitstromfestigkeit:	Icw: 3,44 kA	Umgebungs- temperatur:	25°C
Bedingte Bemessungskurzschlußstromfestigkeit: (Ik3 nur bei Kurzschlußschutzeinrichtung (SCPD) in Einspeisung)	Icc:		
Bemessungsschaltvermögen Leitungsschutzschalter:	6 kA		

Installationsverteiler, nach DIN EN 61439-1/-3





Für dieses Dokument und den darin dargestellten Inhalt behalten wir uns alle Rechte vor. Die Vervielfältigung des Inhaltes ist ohne unsere ausdrückliche Zustimmung nicht gestattet.


3			Angebotsnr.	A2024-2543	Projektname: SEGRO Park Düsseldorf Flingern	 EtecProjekt + Bau GmbH	Index: a
2			Datum	30.04.2025			= UL01
1			Erstellt	Schwarte Kevin			+ UV OG Unit (UL01)
Änderung	Änderungsdatum	Geändert	Bestätigt	Thiele Christian	Deckblatt		Blatt: 1 / 6
Massstab: 1	Ik3:	Ik1:	TN-S				

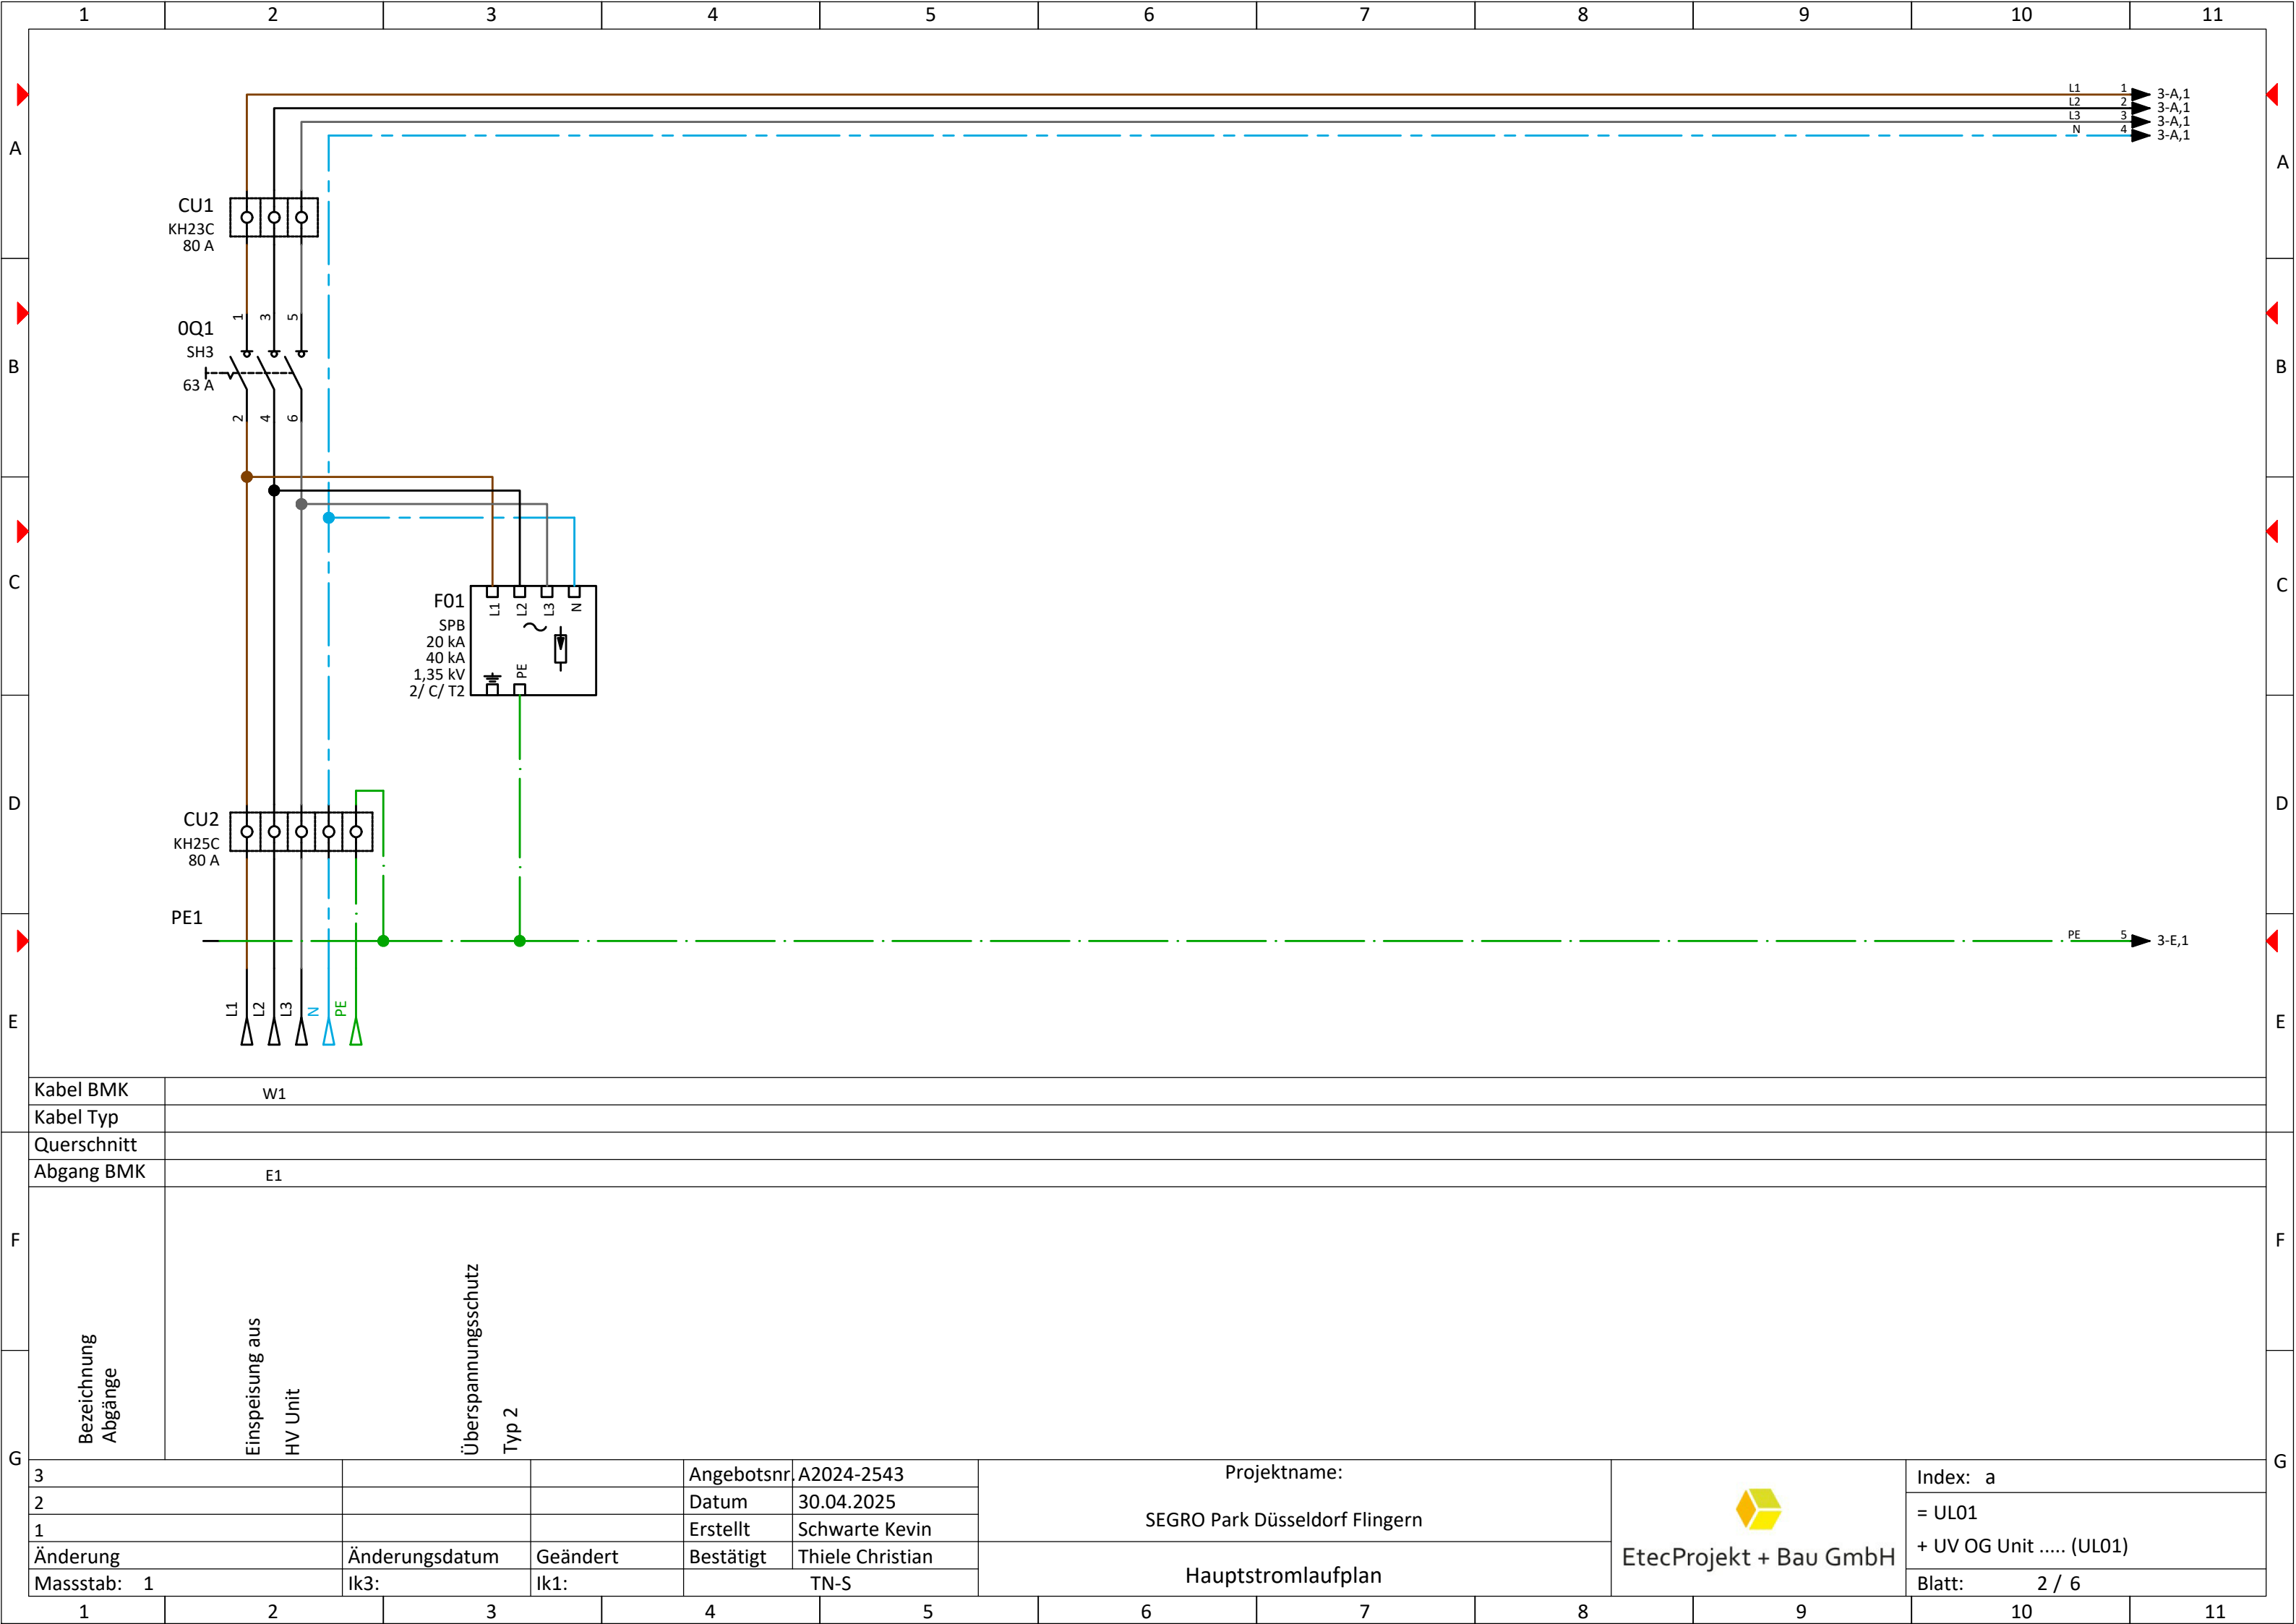




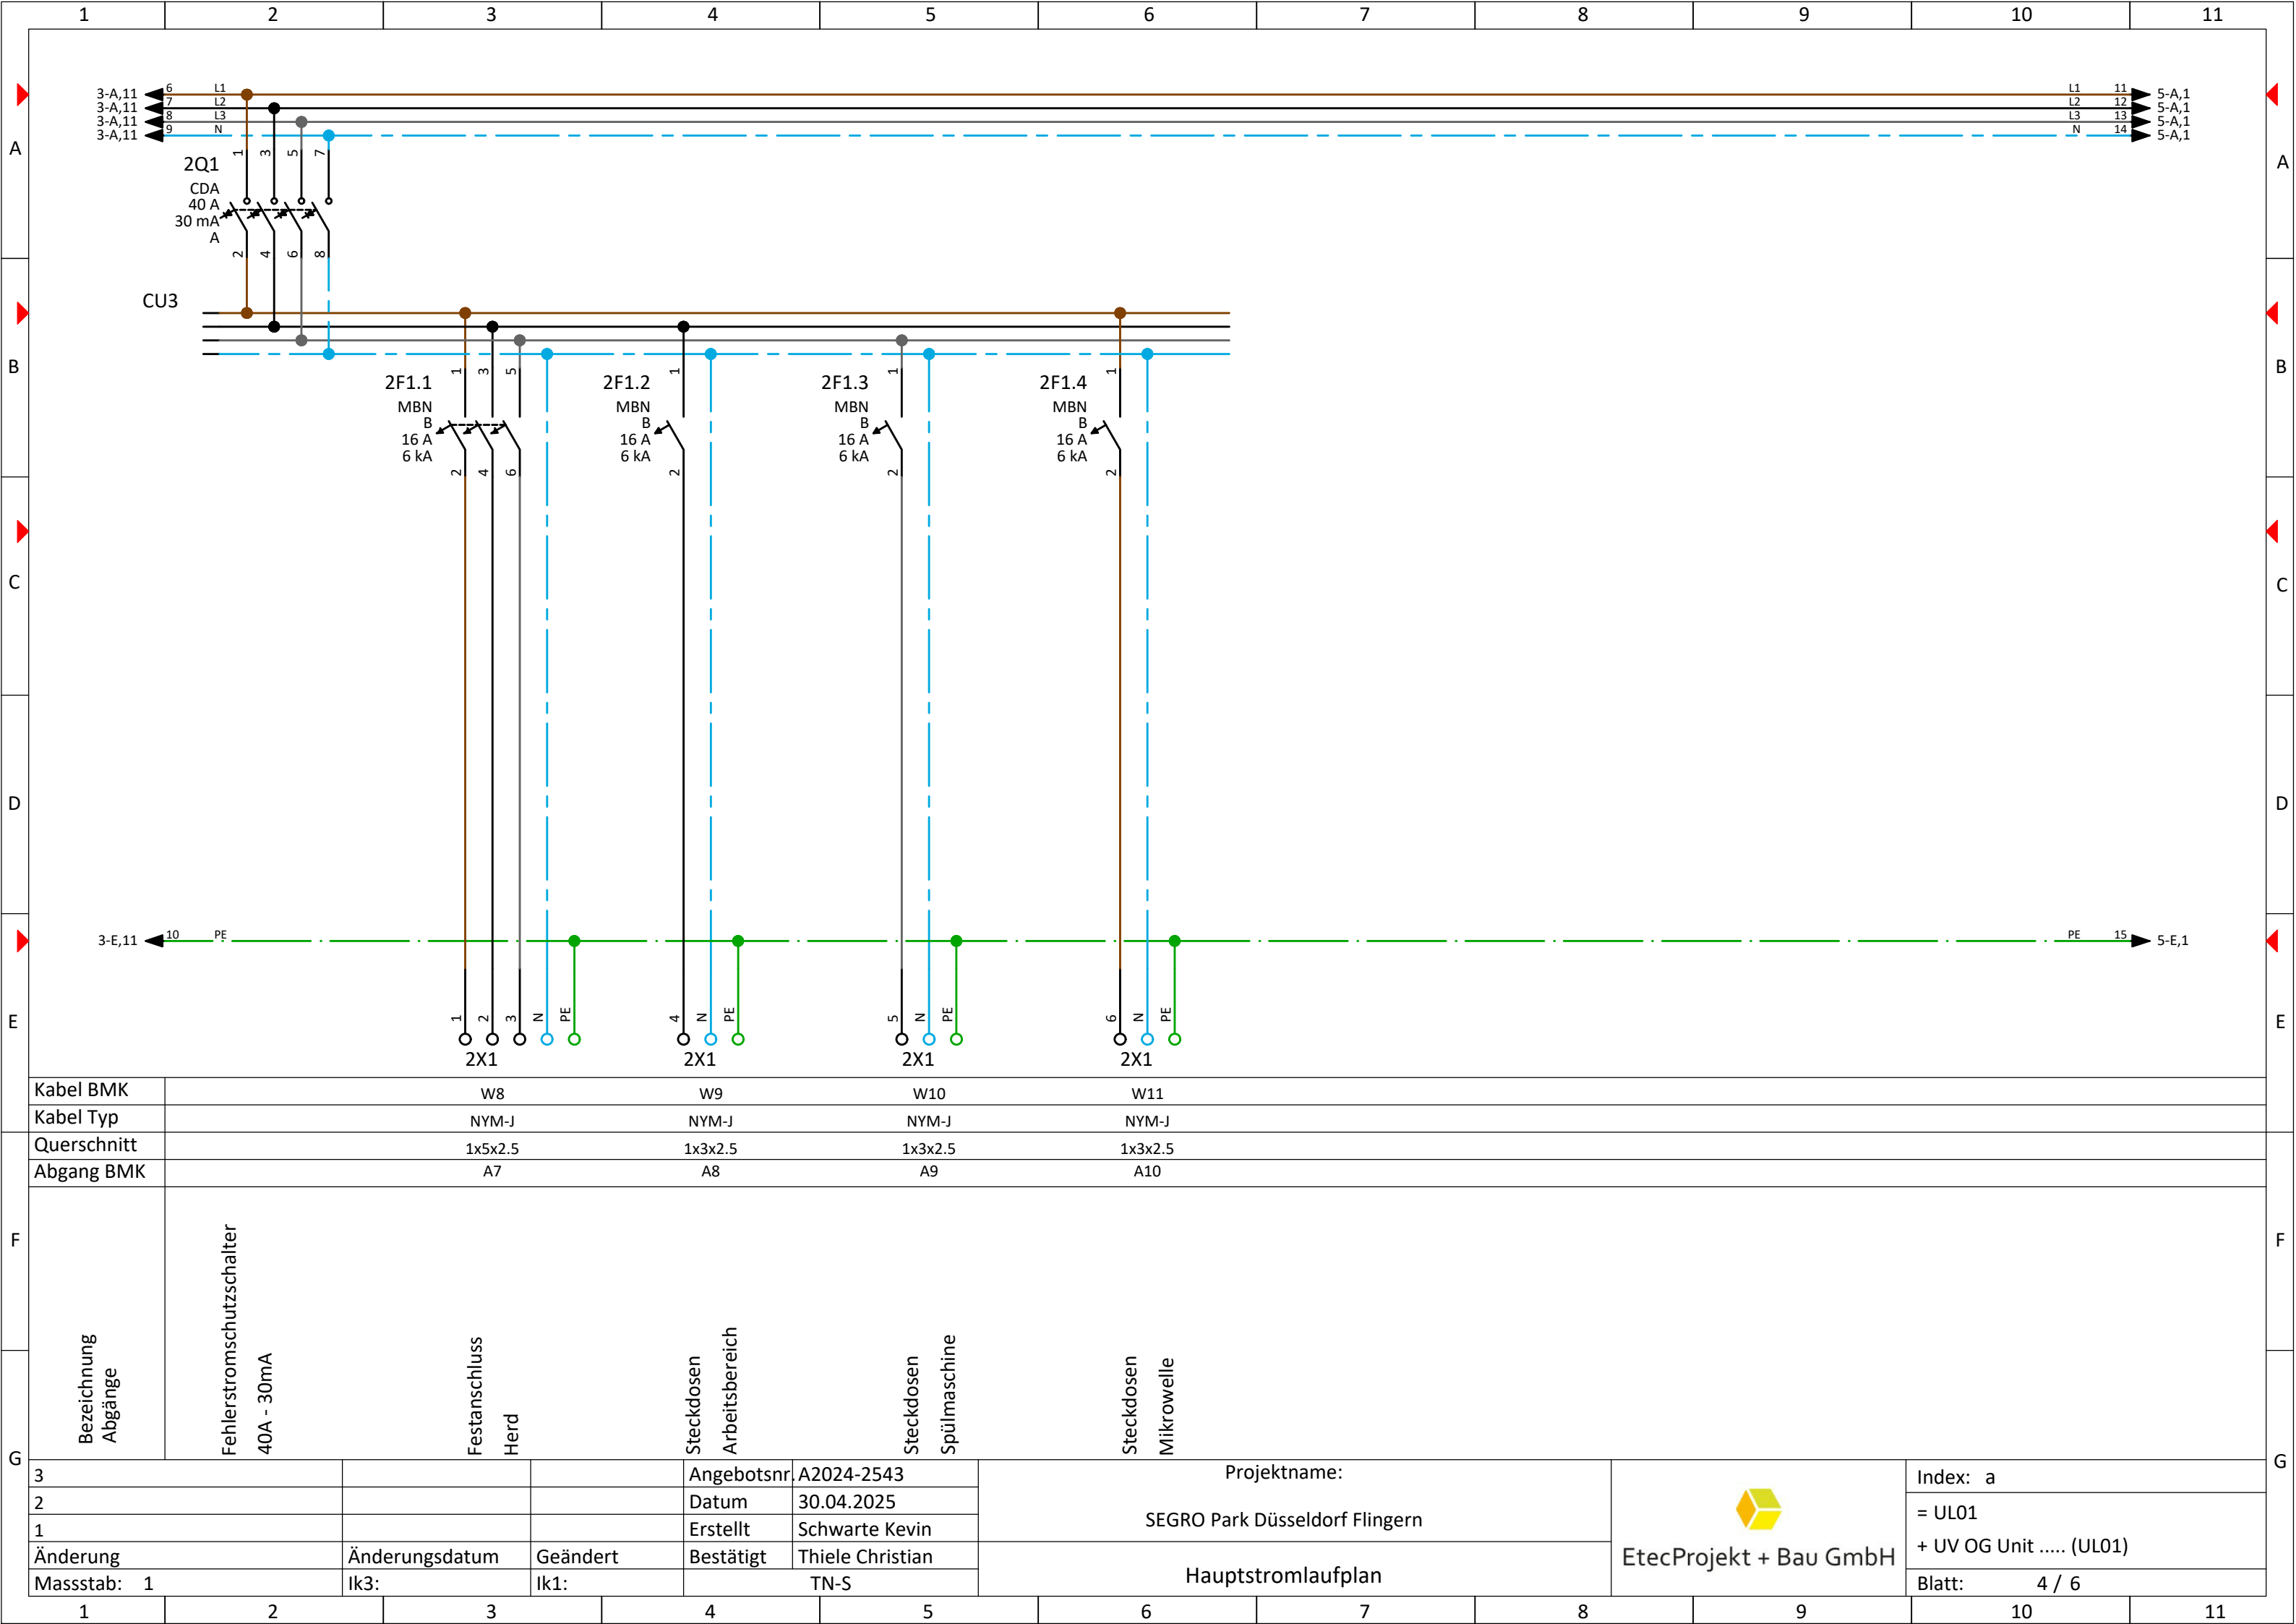


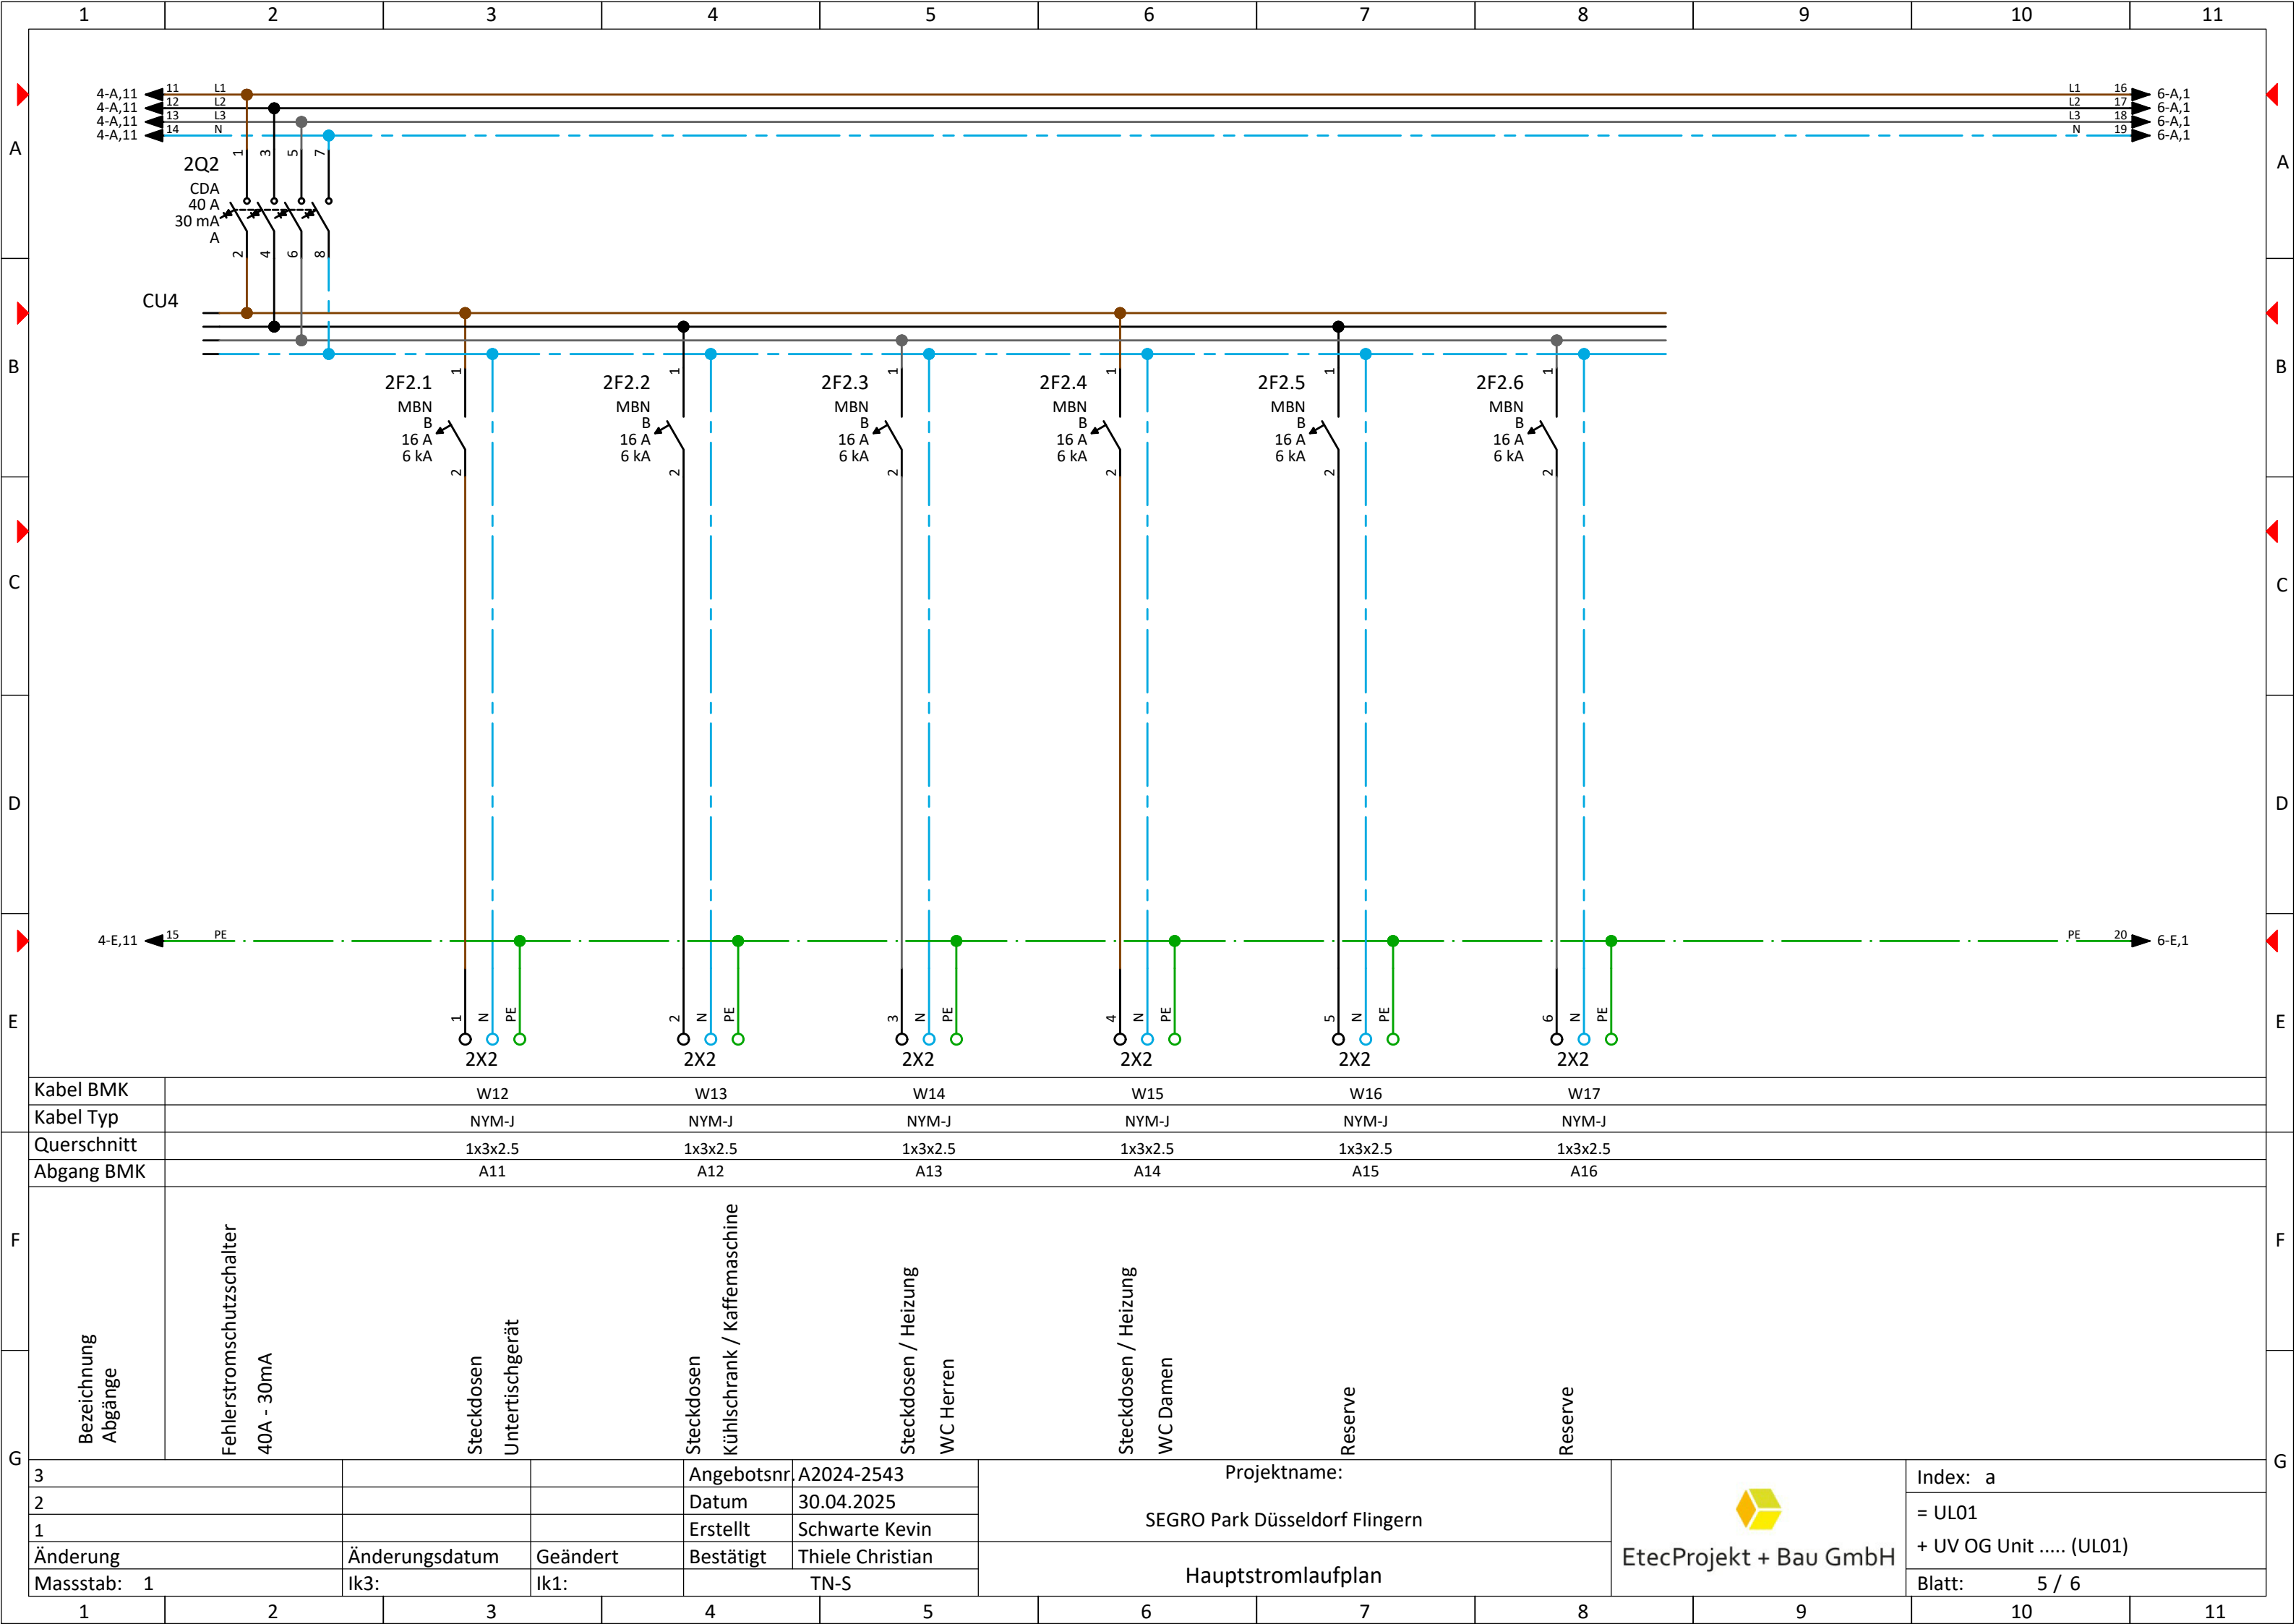

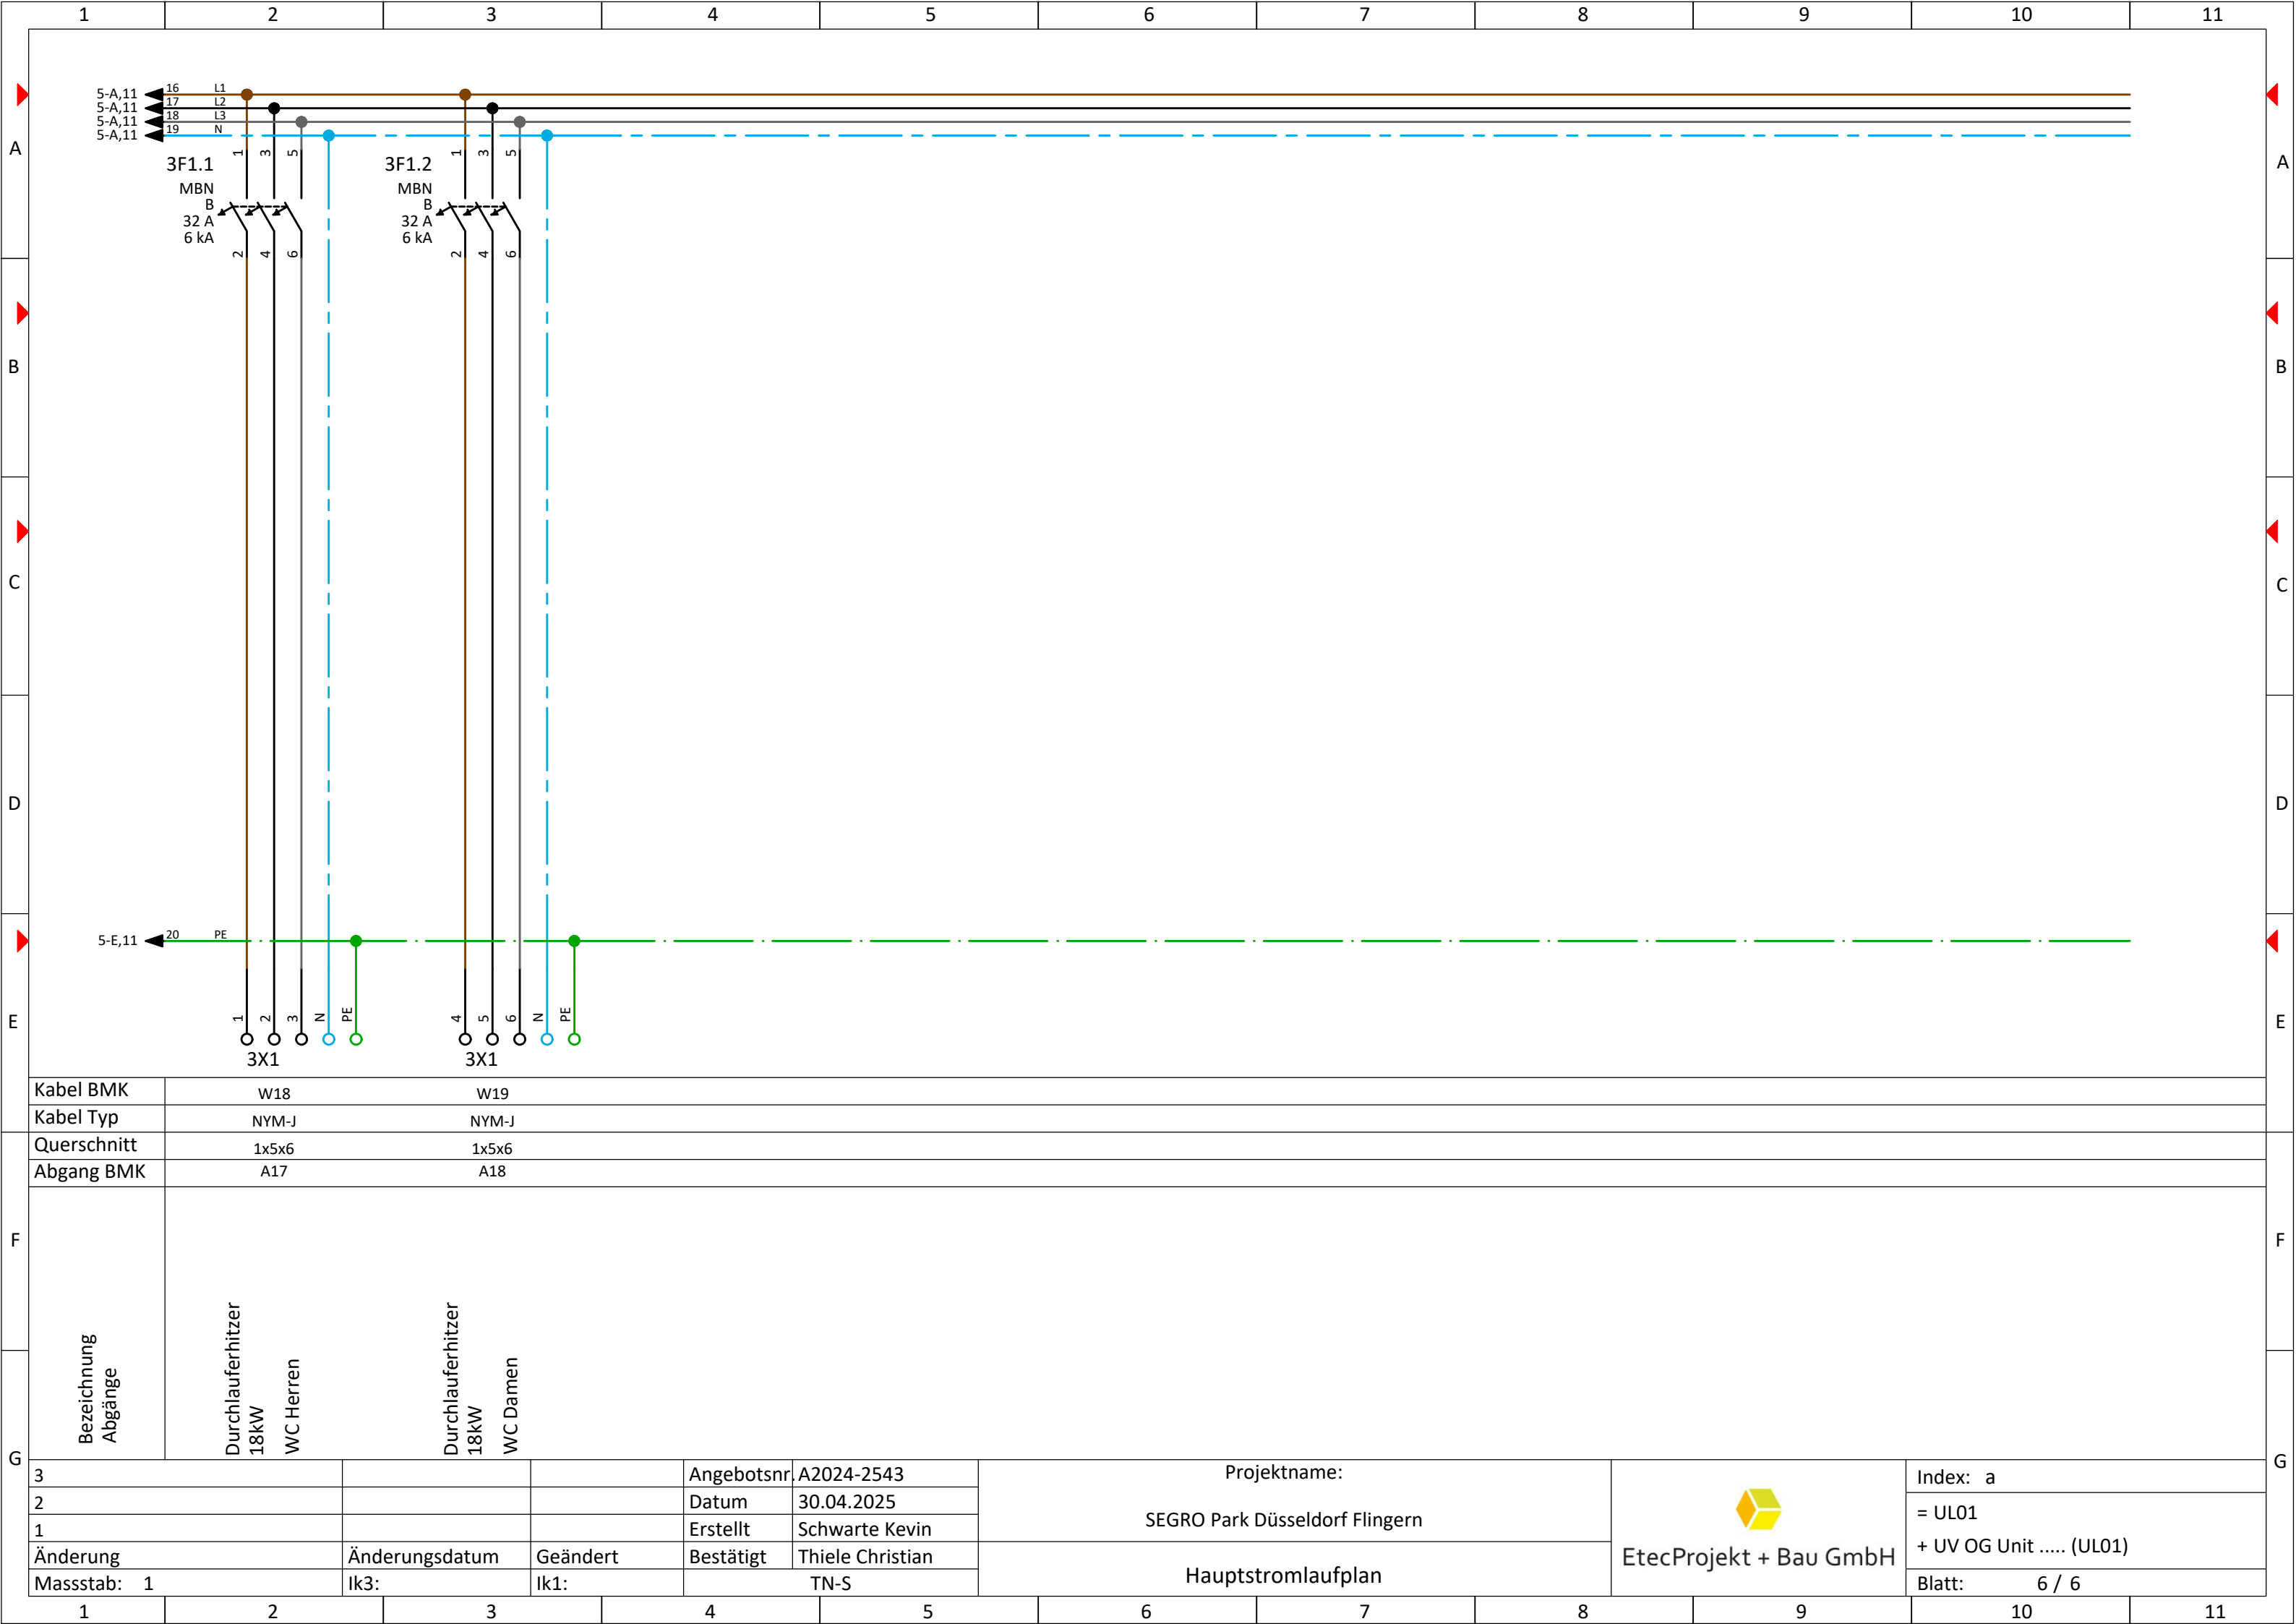

Kabel BMK	W18		W19				
Kabel Typ	NYM-J		NYM-J				
Querschnitt	1x5x6		1x5x6				
Abgang BMK	A17		A18				
Bezeichnung Abgänge							
3			Angebotsnr.	A2024-2543	Projektname: SEGRO Park Düsseldorf Flingern	 EtecProjekt + Bau GmbH	Index: a
2			Datum	30.04.2025			= UL01
1			Erstellt	Schwarte Kevin			+ UV OG Unit (UL01)
Änderung		Änderungsdatum	Geändert	Bestätigt	Thiele Christian		Hauptstromlaufplan
Massstab: 1		Ik3:	Ik1:	TN-S			

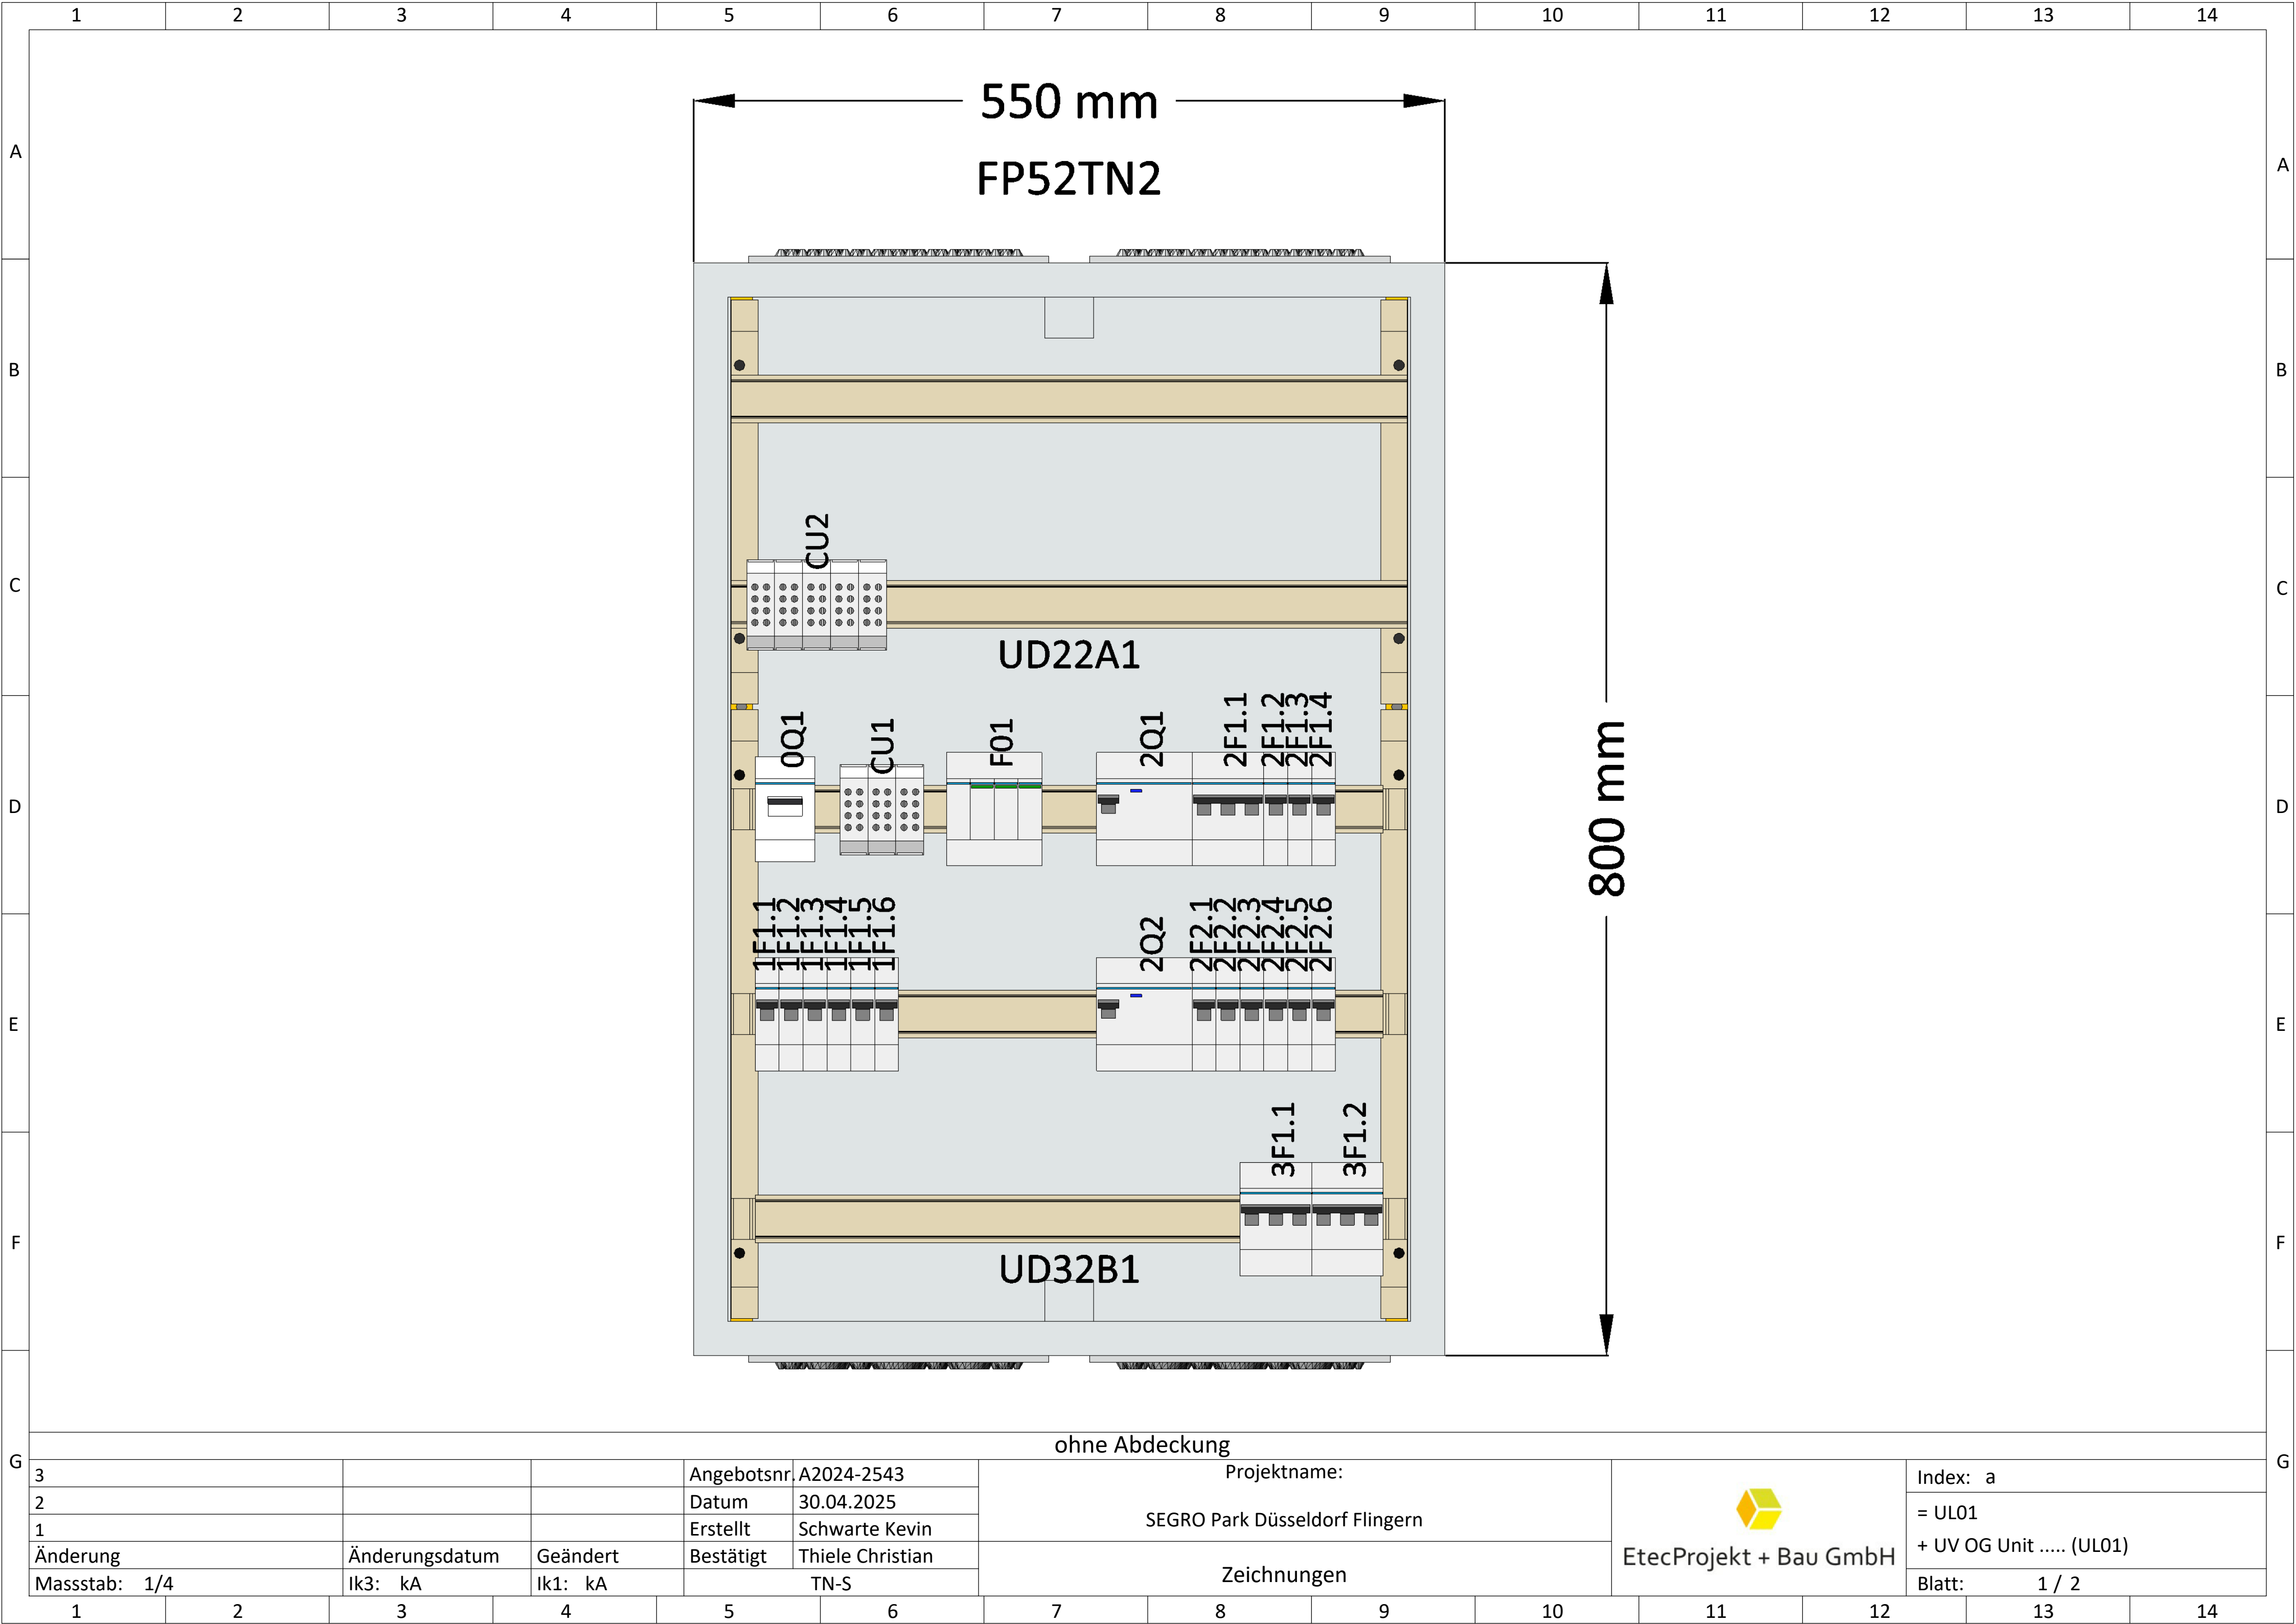

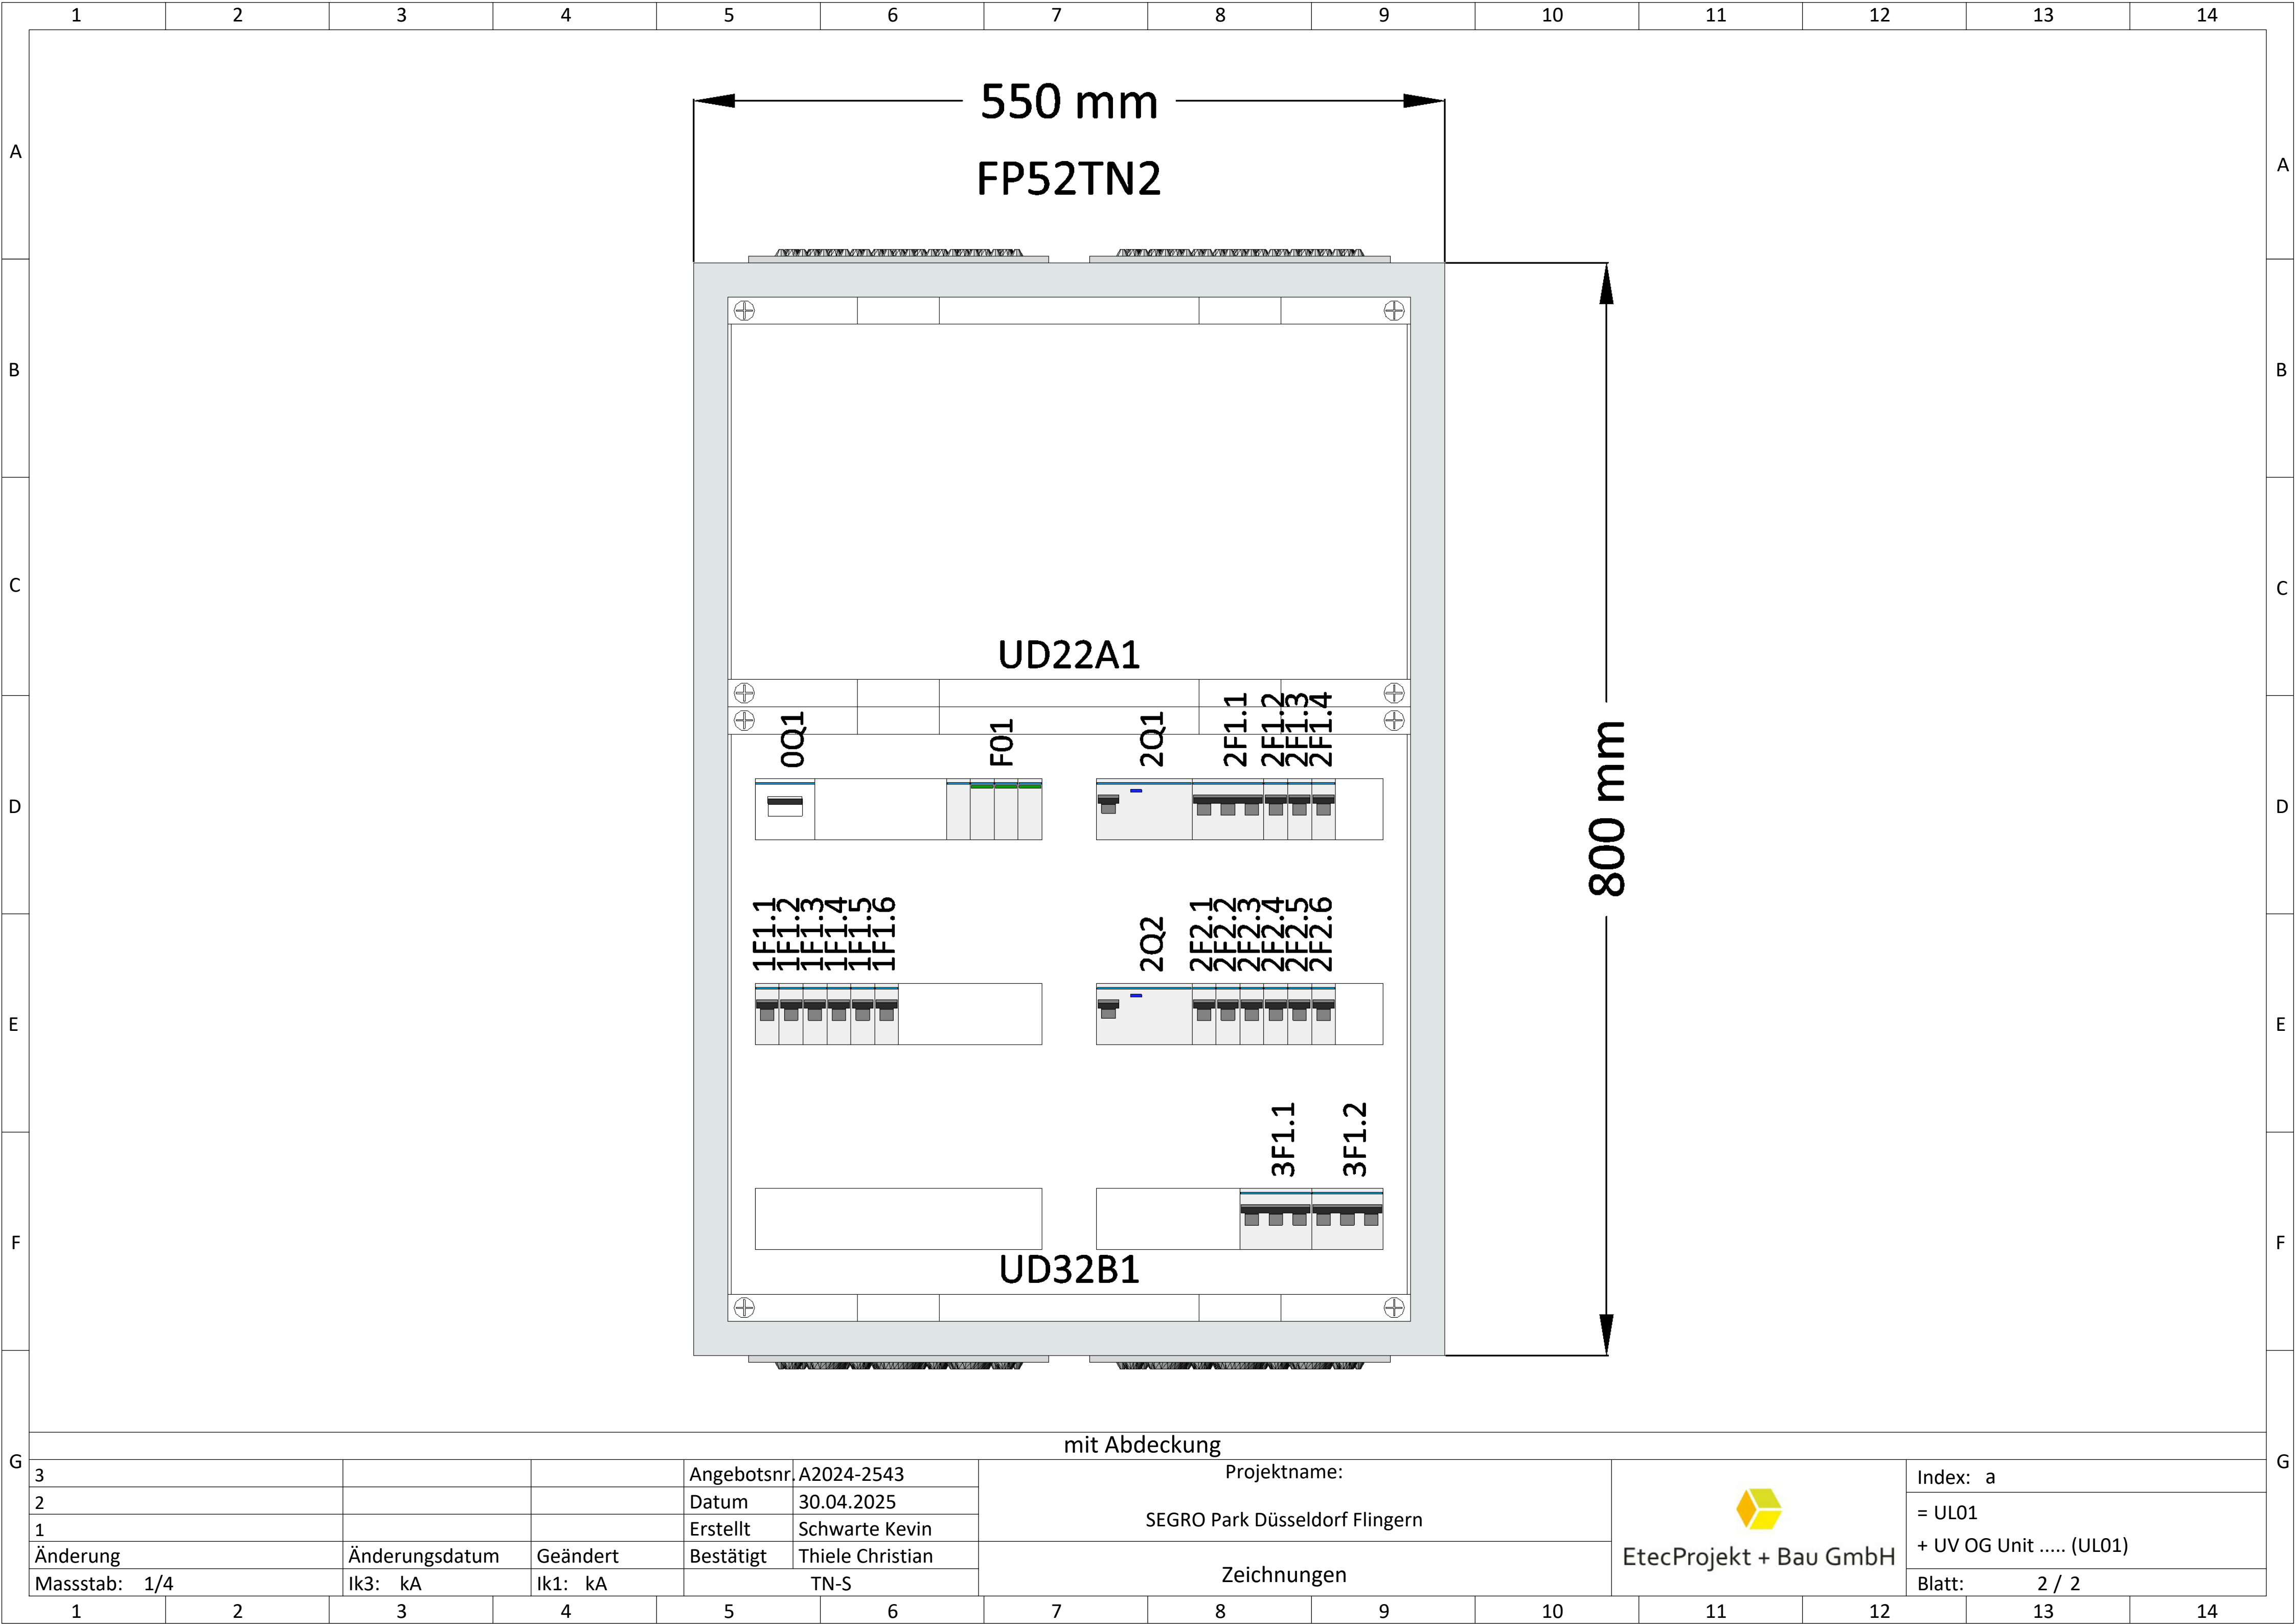

G	mit Abdeckung														G												
	3						Angebotsnr.	A2024-2543		Projektname: SEGRO Park Düsseldorf Flingern				 EtecProjekt + Bau GmbH		Index: a											
	2						Datum	30.04.2025								= UL01 + UV OG Unit (UL01)											
	1						Erstellt	Schwarte Kevin																			
	Änderung		Änderungsdatum		Geändert		Bestätigt	Thiele Christian		Zeichnungen						Blatt: 2 / 2											
	Massstab: 1/4		Ik3: kA		Ik1: kA		TN-S																				
1		2		3		4		5		6		7		8		9		10		11		12		13		14	