


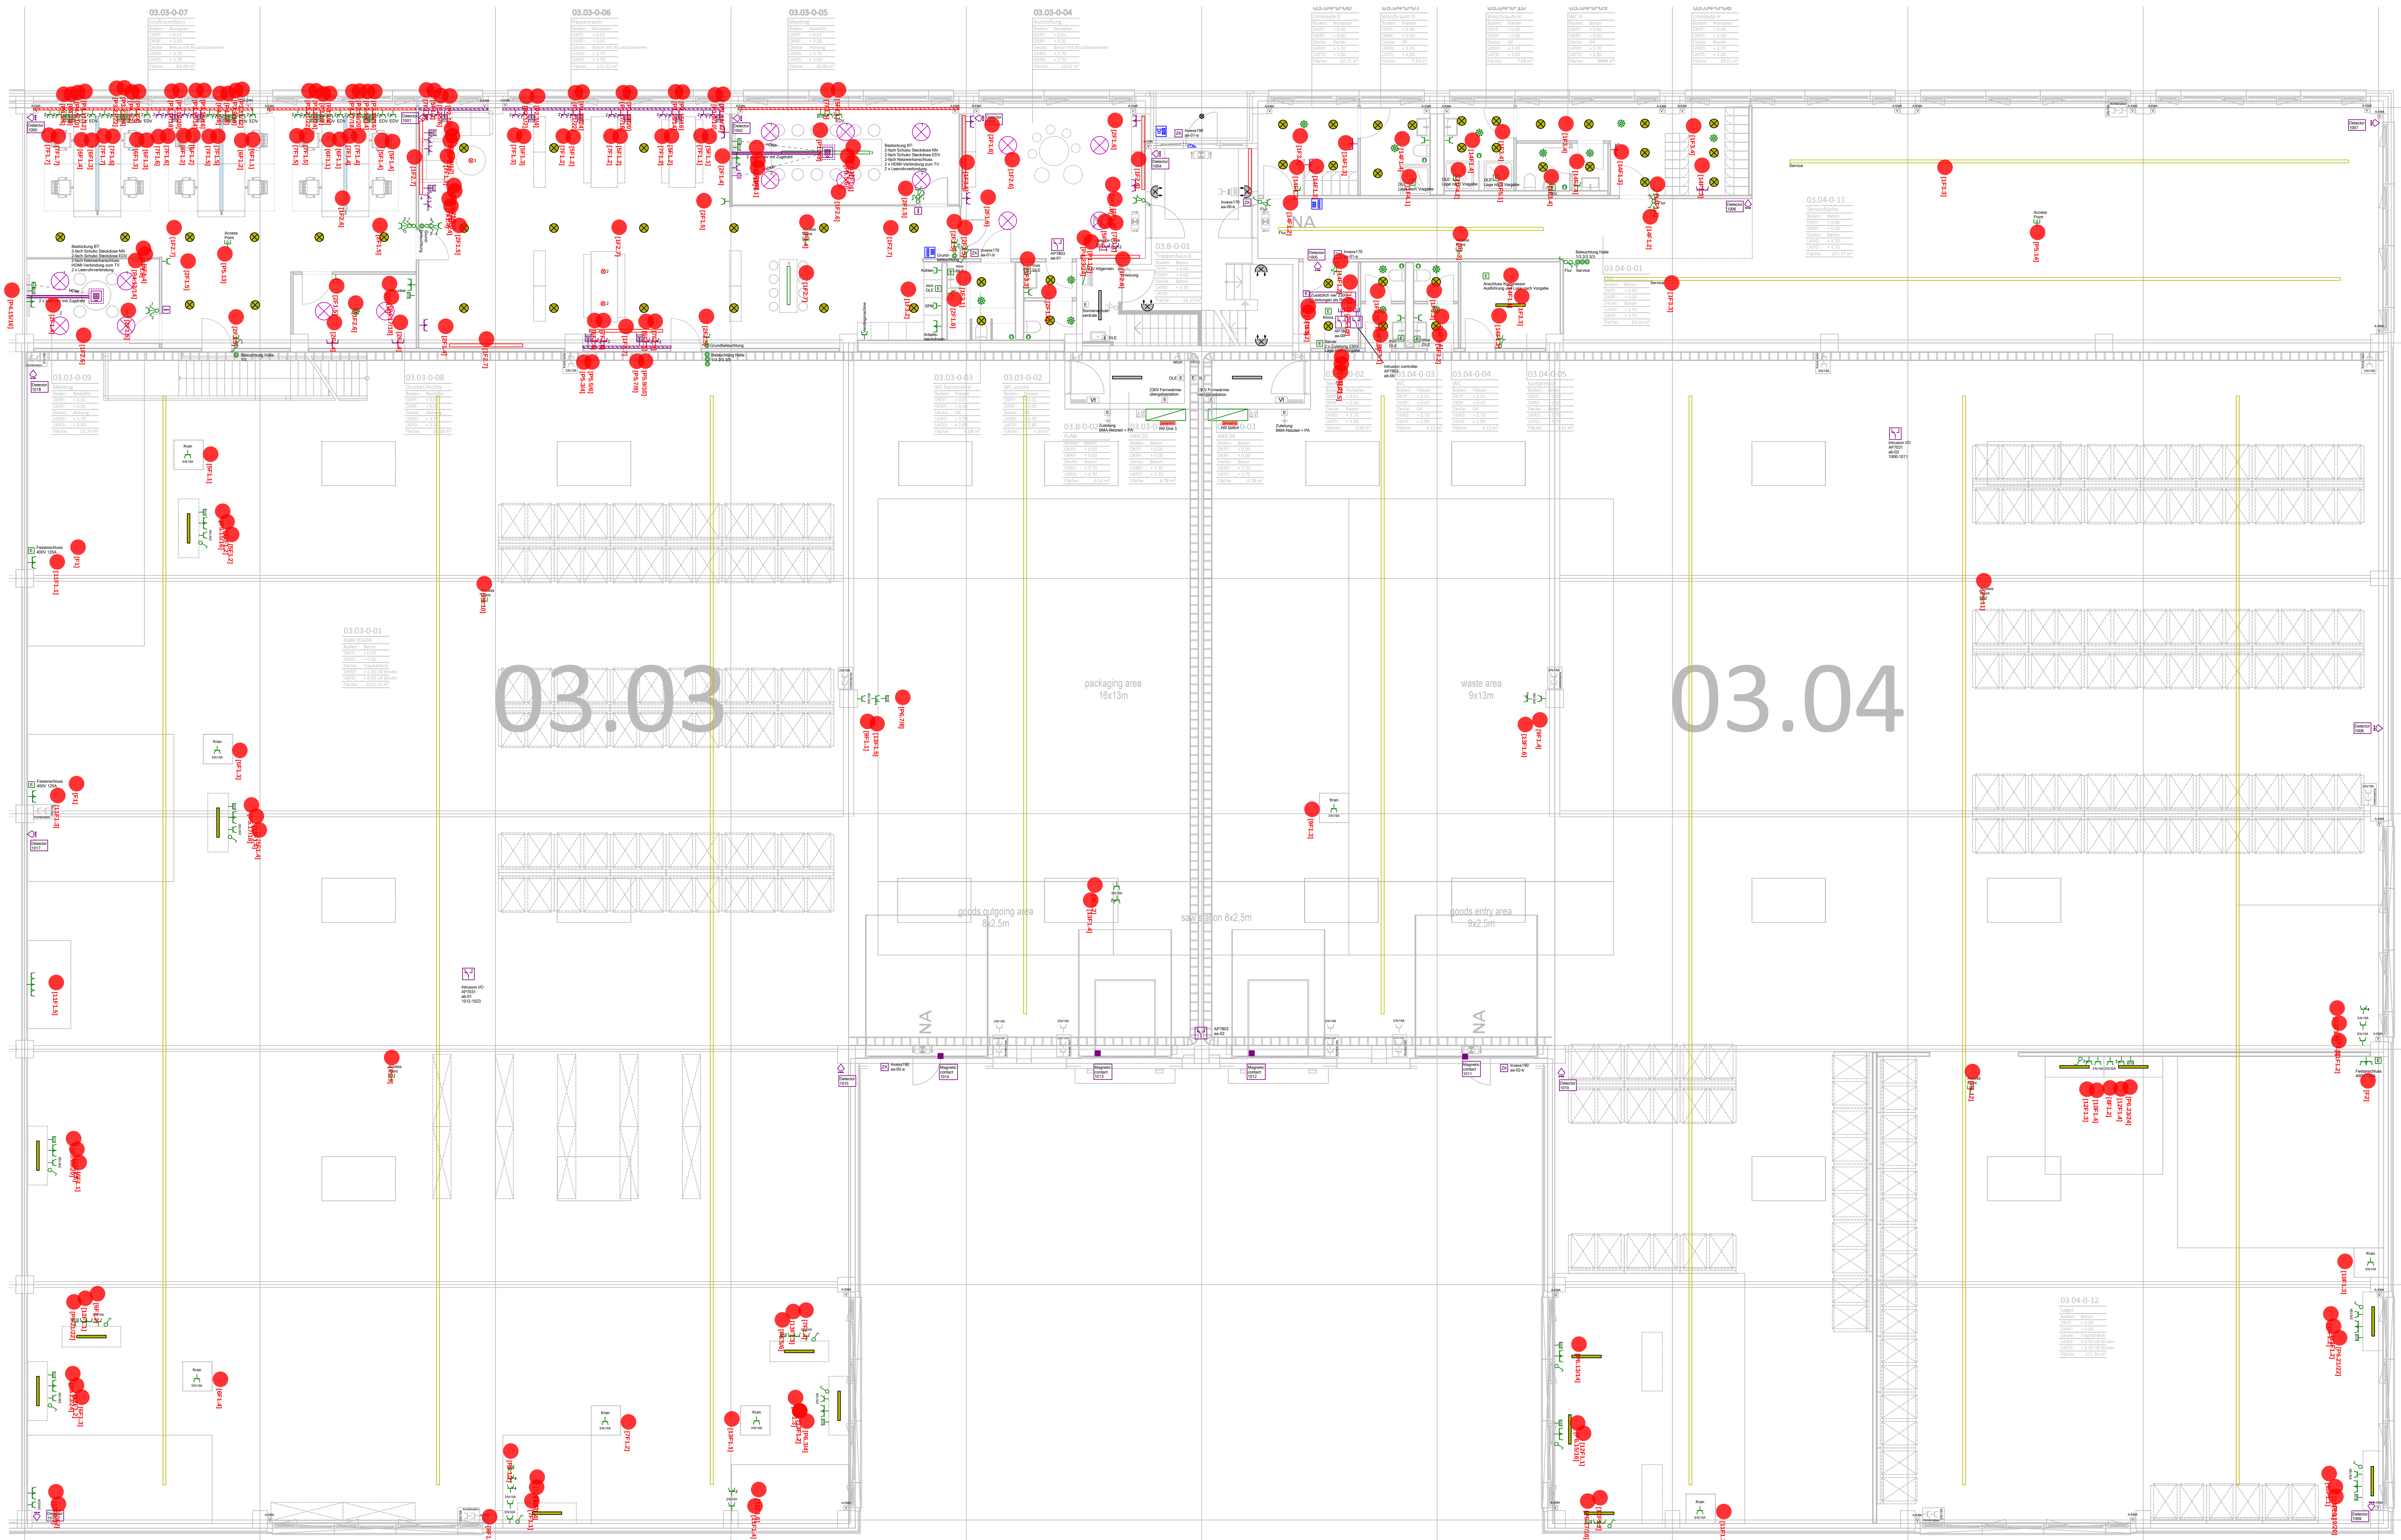

- Legende Elektrotechnik**
- APL Datenleitung Netzwerk
  - Daten-Anschlussdose 2x RJ45
  - Daten-Anschlussdose 1x RJ45
  - Abzweigdose EMA-Tür-/Fensterkontakte
  - Lufteraster
  - NWA Rauchabgangstaster
  - EMA Bewegungsmelder
  - EMA Magnet-Reedkontakt
  - Speicheranlage Außensprechstelle
  - Speicheranlage Innensprechstelle
  - Türöffner
  - Netzwerkanschluss Booking System Meetingraum
  - Zustandskontrolle Reader
  - Tür-Controller
  - Lichtband Arbeitsplätze
  - Pendelschiene
  - Lichtband
  - Retlungszeichen-Leuchte
  - LED-Anbau-FR-Leuchte
  - Anschluss für Decorative pendant light
  - Decken-Viandeleuchte mit Melder
  - LED-Aufbau-Downlight Flure Nebenräume
  - LED-Aufbau-Downlight Büro BAP
  - Erleuchtung allgemein
  - Potentialausgleichsschiene
  - Kabelbühne
  - Ausschalter
  - Seienschalter
  - Wechselschalter
  - Kreuzschalter
  - Taster ohne Glühlampe
  - Präsenzmelder
  - Schuko Steckdose 1-fach
  - Schuko Steckdose 2-fach waagrecht
  - CEE-Steckdose 5x 16A 5-pol.
  - CEE-Steckdose 6x 32A 5-pol.
  - CEE-Steckdose 5x 32A 5-pol.
  - Schuko Steckdose 2-fach
  - Schuko Steckdose 3-fach
  - Schuko Steckdose 4-fach
  - Schuko Steckdose 2-fach
  - Schuko 2-fach Steckdose
  - Elektrischer Anschluss, allgemein
  - Anschlusspunkt Lüfter
  - Brüstungskanal
  - Kunststoff-Isolierrohr
  - Bodentank

**SDF\_3\_5\_EP\_MA\_0\_003\_B\_V**

|                                                                                     |                                                                                        |
|-------------------------------------------------------------------------------------|----------------------------------------------------------------------------------------|
| Auftraggeber<br>SEGRO 15. Grundbesitz GmbH<br>Fichtenstrasse 33<br>40233 Düsseldorf | Bauvorhaben<br>SEGRO Park Düsseldorf Flingern<br>Höhenweg 271a-287<br>40233 Düsseldorf |
|-------------------------------------------------------------------------------------|----------------------------------------------------------------------------------------|

**EtecProjekt + Bau GmbH**  
Heinrich-Hertz-Straße 22a  
40699 Erkrath  
Tel.: 0211 - 210233 - 00  
Fax: 0211 - 210233 - 20  
Mail: info@etecprojekt.de

|       |                                                                  |             |              |
|-------|------------------------------------------------------------------|-------------|--------------|
| A     | Beleuchtung angepasst                                            | 02.04.2026  | ETEC         |
| B     | Installation nach Vorgabe erweitert in dunkelviolett dargestellt | 17.04.2026  | ETEC         |
| Index | Änderungen                                                       | geändert am | geändert von |

|                    |                                         |
|--------------------|-----------------------------------------|
| Blatt: 1           | Projekt: SEGRO Park Düsseldorf Flingern |
| Größe: 1355*841    | Zeichnung: Elektrotechnik LI03          |
| Urspr.: COP        | Einheit: 03+04 EG                       |
| Datei: ETEC06042   | MA Grundfos Germany GmbH                |
| Stand: 27.02.202   | Gewerk: Elektrotechnik                  |
| Datum: 27.03.2026  | Maßstab: 1:75                           |
| Bearb.: 27.03.2026 |                                         |
| Gepr.: 27.03.2026  |                                         |