


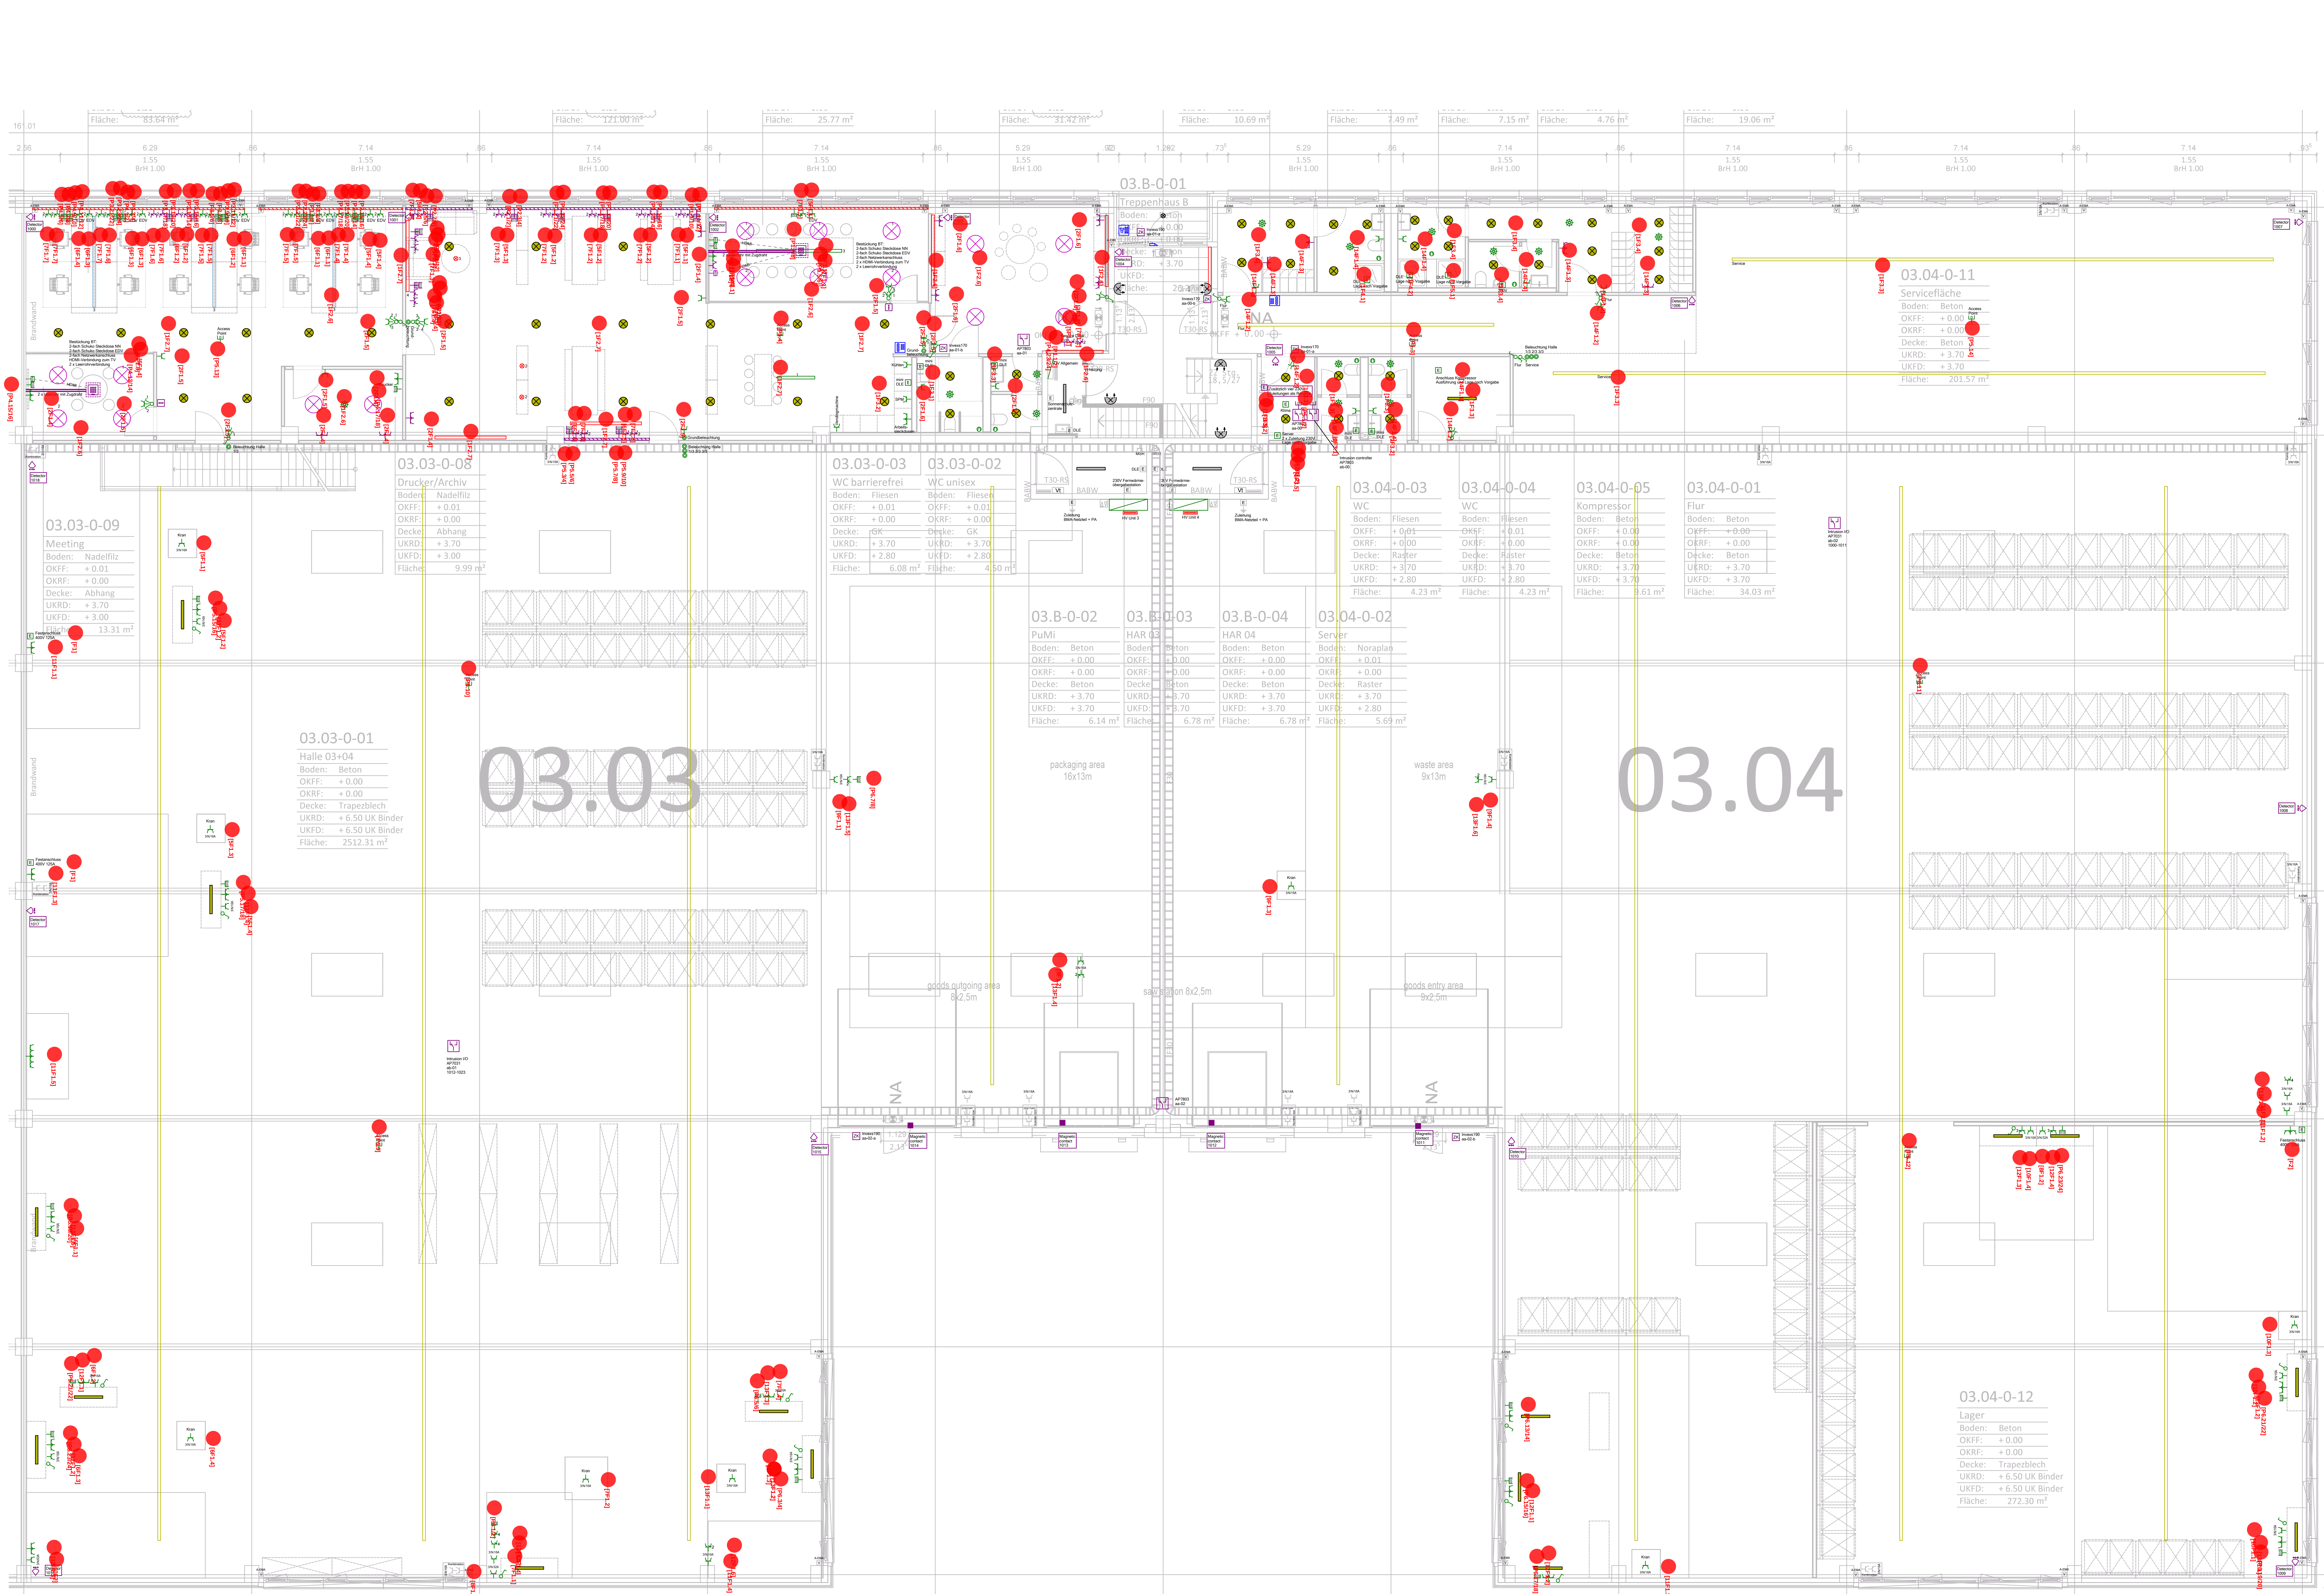

- Legende Elektrotechnik**
- APL Datenleitung Netzwerk
 - Daten-Anschlussdose 2x RJ45
 - Daten-Anschlussdose 1x RJ45
 - Abzweigdose EMA-Tür-/Fensterkontakte
 - Lufteraster
 - NWA Rauchabgangstaster
 - EMA Bewegungsmelder
 - EMA Magnet Reedkontakt
 - Sprechanlage Außensprechstelle
 - Sprechanlage Innensprechstelle
 - Türöffner
 - Netzwerkanschluss Booking System Meetingraum
 - Zustandskontrolle Reader
 - Tür-Controller
 - Lichtband Arbeitsplätze
 - Pendelschiene
 - Lichtband
 - Retlungszeichen-Leuchte
 - LED-Anbau-FR-Leuchte
 - Anschluss für Decorative pendant light
 - Decken-Vandeleuchte mit Melder
 - LED-Aufbau-Downlight, Flure Nebenräume
 - LED-Aufbau-Downlight Büro BAP
 - Erldung allgemein
 - Potentialausgleichsschiene
 - Kabelbühne
 - Ausschalter
 - Seienschalter
 - Wechselschalter
 - Kreuzschalter
 - Taster ohne Glühlampe
 - Präsenzmelder
 - Schuko Steckdose 1-fach
 - Schuko Steckdose 2-fach waagrecht
 - CEE-Steckdose 5x 16A 5-pol.
 - CEE-Steckdose 5x 32A 5-pol.
 - CEE-Steckdose 5x 32A 5-pol.
 - Schuko Steckdose 2-fach
 - Schuko Steckdose 3-fach
 - Schuko Steckdose 4-fach
 - Schuko Steckdose 2-fach
 - Schuko 2-fach Steckdose
 - Elektrischer Anschluss, allgemein
 - Anschlusspunkt Lüfter
 - Brüstungskanal
 - Kunststoff-Isolierrohr
 - Bodentank

SDF_3_5_EP_MA_0_003_D_V

Auftraggeber SEGRO 15. Grundbesitz GmbH Fichtenstrasse 33 40233 Düsseldorf		Bauvorhaben SEGRO Park Düsseldorf Flingern Höhenweg 271a-287 40233 Düsseldorf	
---	--	--	--

EtecProjekt + Bau GmbH
Heinrich-Hertz-Straße 22a
40699 Erkrath
Tel.: 0211 - 210233 - 00
Fax: 0211 - 210233 - 20
Mail: info@etecprojekt.de

A	Beleuchtung angepasst	03.04.2026	ETEC
B	Installation nach Vorgabe erweitert in dunkelviolett dargestellt	17.04.2026	ETEC
C	Änderung laut E-Mail Herr Duran	19.05.2026	ETEC
D	Grundriss Index H übernommen	12.06.2026	ETEC
Index	Änderungen	geändert am	geändert von

Blatt: 1	Projekt: SEGRO Park Düsseldorf Flingern
Größe: 1355*841	
Urspr.: COP	Zeichnung: Elektrotechnik L103
Datei: ETEC0042	Einheit: 03+04 EG
Stand: 27.02.202	MA Grundfos Germany GmbH
Datum: 27.03.2026	Gewerk:
Bearb: 27.03.2026	ETEC
Gepr: 27.03.2026	
Elektrotechnik	
Maßstab: 1:75	