


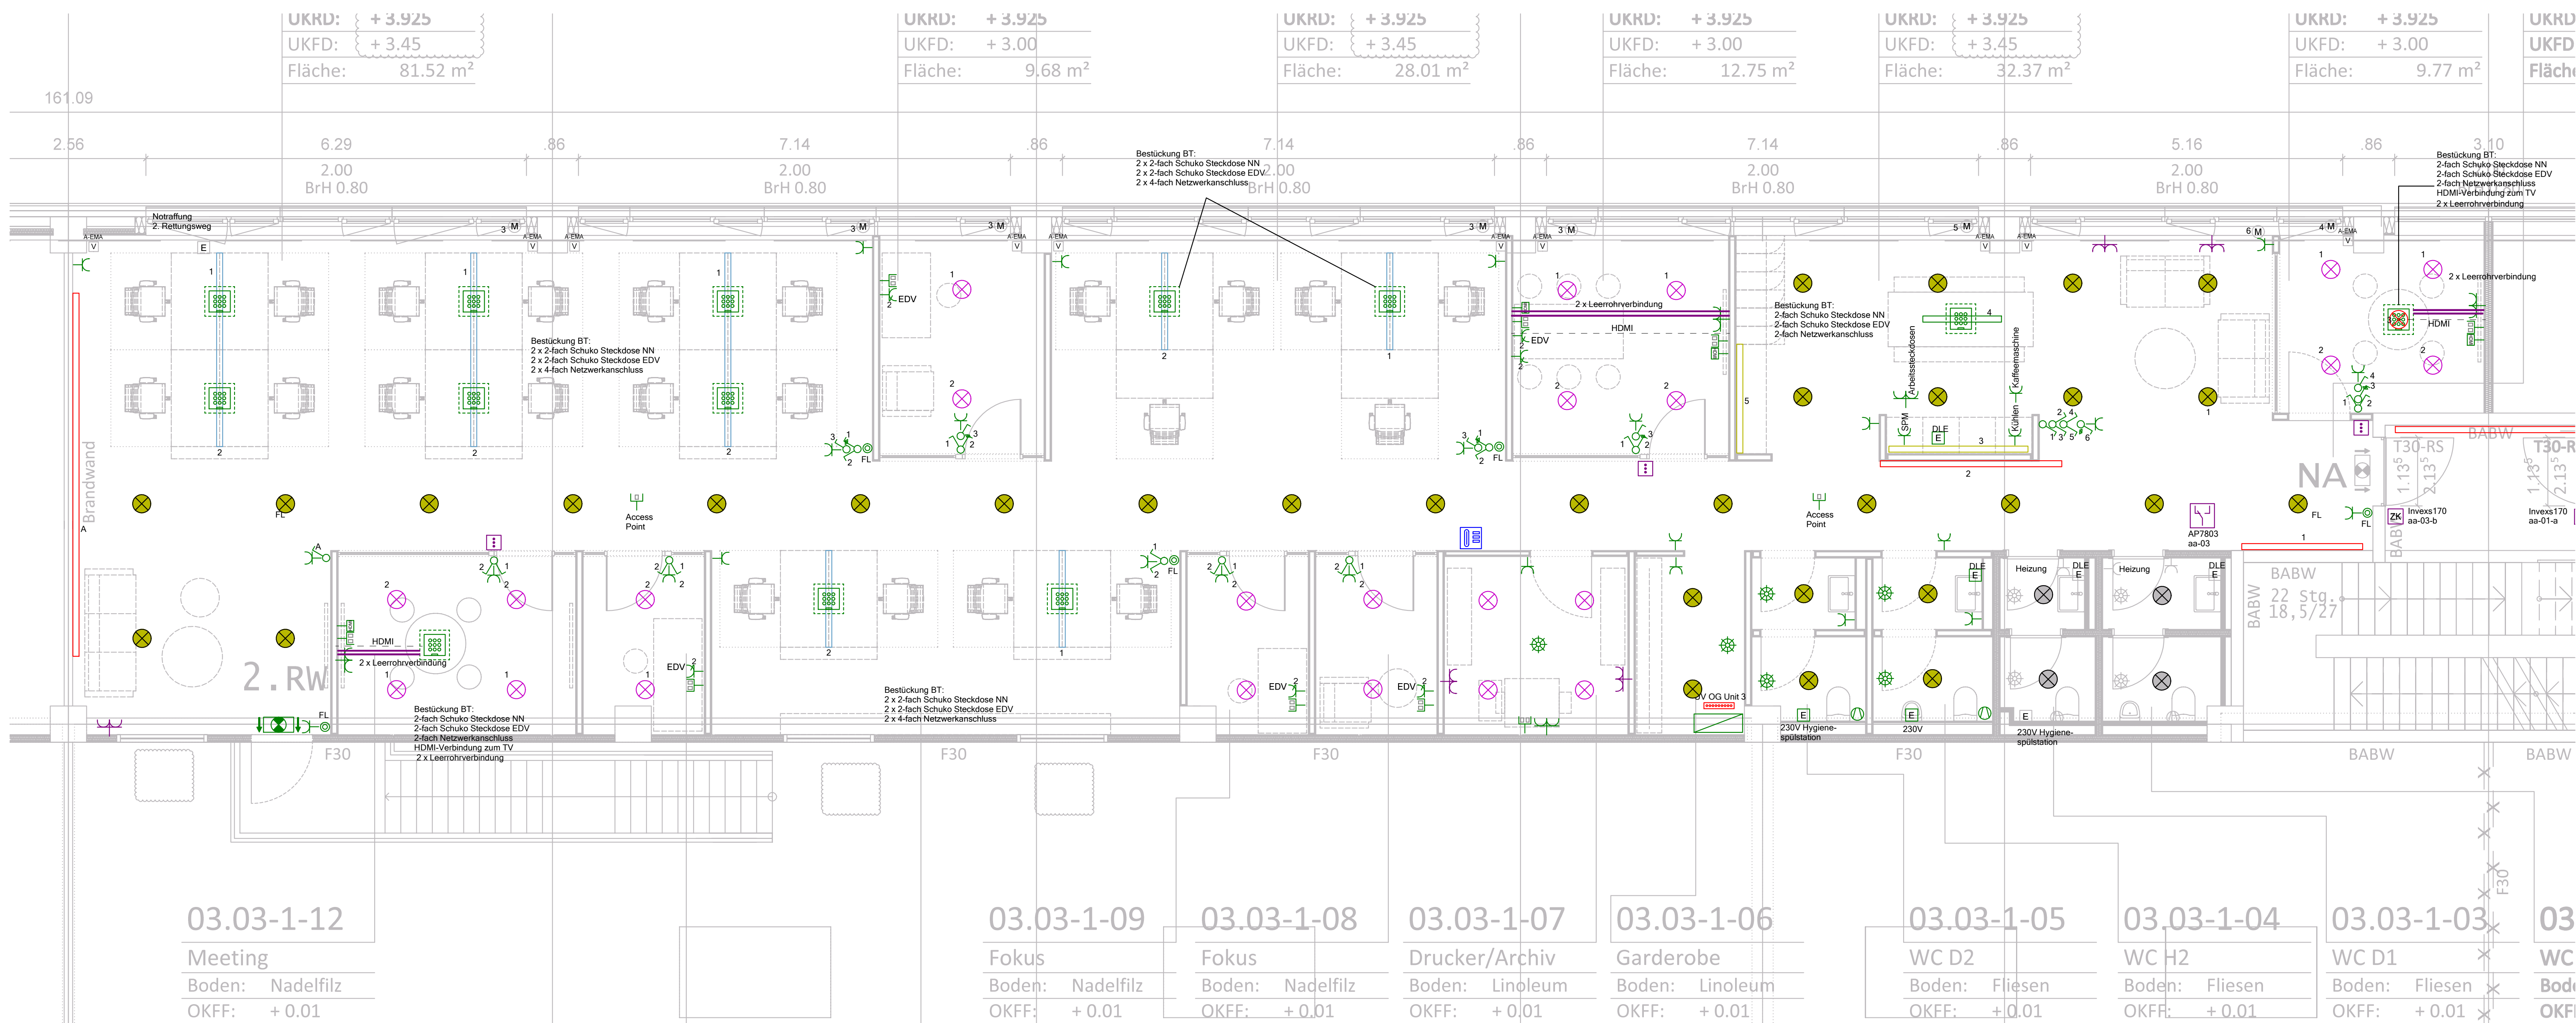

- Legende Elektrotechnik**
- Elektronen-Anschlussdose 2x RJ45
 - Abzweigdose EMA-Tür-/ Fensterkontakte
 - Sprechanlage Innensprechstelle
 - Netzwerkanschluss Booking System Meetingraum
 - Zurückkontrolle Reader
 - Tür-Controller
 - Lichtband Arbeitsplätze
 - Lichtschiene mit Spots
 - LED Stripe
 - Pendelschiene
 - LED-Aufbau-Downlight Flure Nebenräume
 - Retungszeichen-Leuchte
 - Potentialausgleichschiene
 - Ausschalter
 - Serienschalter
 - Jalousieschalter
 - Taster ohne Glühlampe
 - Präsenzmelder
 - Schuko 2-fach Steckdose EDV
 - Schuko 1-fach Steckdose
 - Schuko 2-fach Steckdose waagrecht
 - Elektrischer Anschluss, allgemein
 - Ventilator
 - Motor
 - Bodenlank
 - Kunststoff-Isolierrohr



SDF_3_5_EP_MA_1_003_D_V

Auftraggeber	Bauvorhaben
SEGRO 15. Grundbesitz GmbH Fichtenstrasse 33 40233 Düsseldorf	SEGRO Park Düsseldorf Flingern Höhenweg 271a-287 40233 Düsseldorf

**EtecProjekt + Bau GmbH**

Heinrich-Hertz-Straße 22a
40699 Erkrath
Tel.: 0211 - 210233 - 00
Fax: 0211 - 210233 - 20
Mail: info@etecprojekt.de

A	Beleuchtung angepasst	02.04.2026	ETEC
B	Installation nach Vorgabe erweitert dunkelviolett dargestellt	17.04.2026	ETEC
C	Anpassung laut E-Mail Herr Djuran	19.05.2026	ETEC
D	Grundriss Index F übernommen	12.06.2026	ETEC
Index	Änderungen	geändert am	geändert von

Blatt: 1	Projekt: SEGRO Park Düsseldorf Flingern
Größe: A0	Zeichnung: Elektrotechnik LI03
Unspr. COP	Einheit 03+04 OG
Datei: ETEC043	MA Grundfos Germany GmbH
Stand: 27.03.2026	Gewerk: Elektrotechnik
Datum: 27.03.2026	Name: ETEC
Bearb. 27.03.2026	Maßstab: 1:50
Gepr. 27.03.2026	