


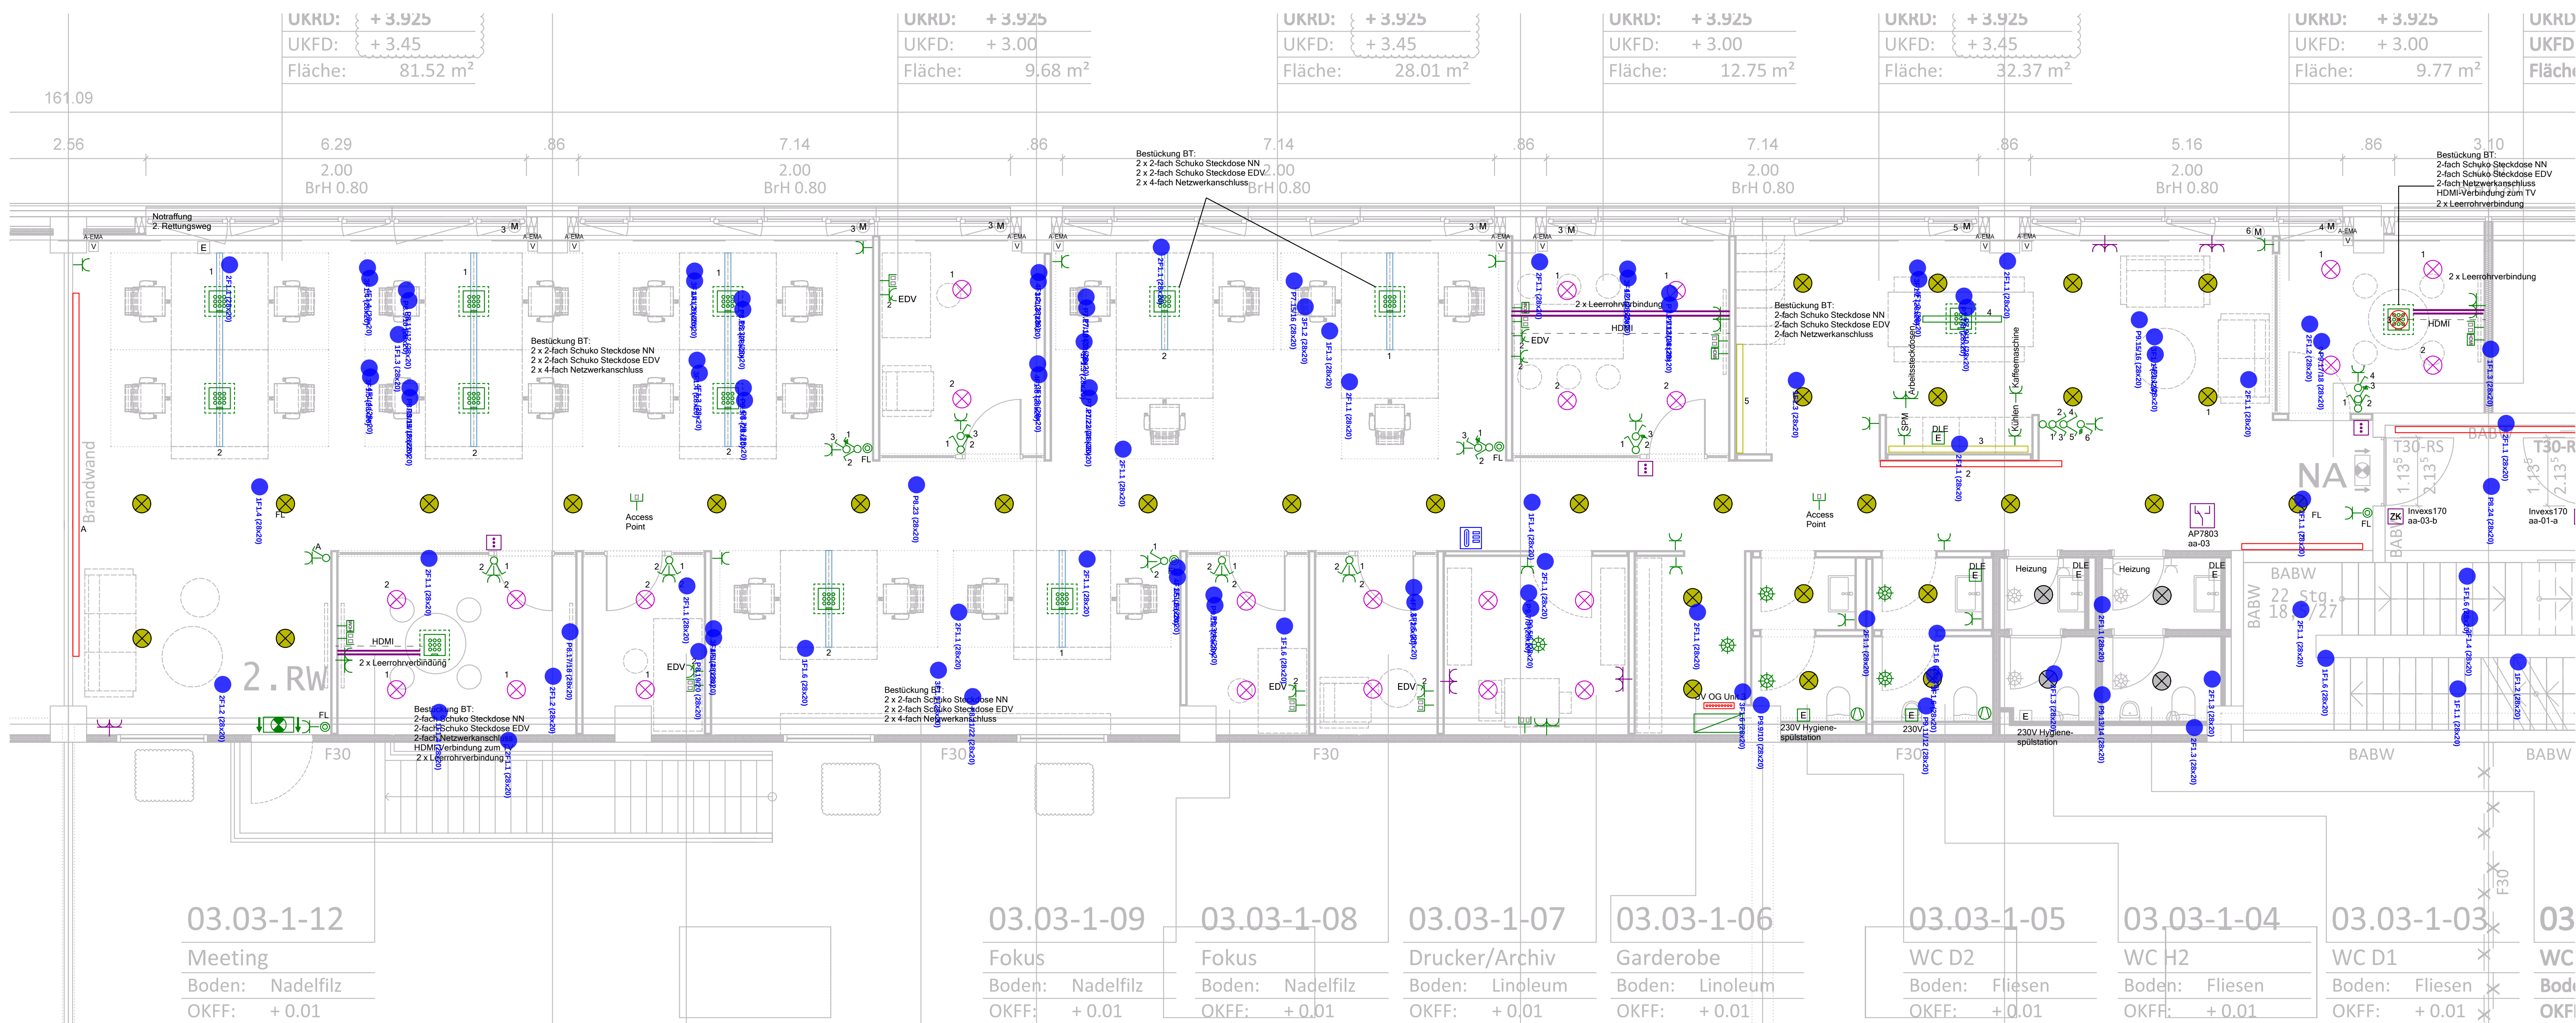

- Legende Elektrotechnik**
- Daten-Anschlussdose 2x RJ45
 - Abzweigdose EMA-Tür/ Fensterkontakte
 - Sprechanlage Innensprechstelle
 - Zutrittskontrolle Reader
 - Tür-Controller
 - Lichtband Arbeitsplätze
 - Lichtschiene mit Spots
 - LED Stripe
 - Pendelschiene
 - LED-Aufbau-Downlight Flure Nebenräume
 - Retlungszeichen-Leuchte
 - Potentialausgleichschiene
 - Ausschalter
 - Serienschalter
 - Jalousieschalter
 - Taster ohne Glühlampe
 - Präsenzmelder
 - Schuko 2-fach Steckdose EDV
 - Schuko 2-fach Steckdose
 - Schuko 2-fach Steckdose
 - Schuko 2-fach Steckdose waagrecht
 - Elektrischer Anschluss, allgemein
 - Ventilator
 - Motor
 - Bodenlank
 - Kunststoff-Isolierrohr



SDF_3_5_EP_MA_1_003_D_V

Auftraggeber	Bauherr
SEGRO 15. Grundbesitz GmbH	SEGRO Park Düsseldorf Flingern
Fichtenstrasse 33	Höhenweg 271a-287
40233 Düsseldorf	40233 Düsseldorf



EtecProjekt + Bau GmbH

Heinrich-Hertz-Straße 22a
40699 Erkrath
Tel.: 0211 - 210233 - 00
Fax: 0211 - 210233 - 20
Mail: info@etecprojekt.de

A	Beleuchtung angepasst	02.04.2026	ETEC
B	Installation nach Vorgabe erweitert dunkelviolett dargestellt	17.04.2026	ETEC
C	Anpassung laut E-Mail Herr Duran	19.05.2026	ETEC
D	Grundriss Index F übernommen	12.06.2026	ETEC
Index	Änderungen	geändert am	geändert von

Blatt: 1	Projekt: SEGRO Park Düsseldorf Flingern
Größe: A0	Zeichnung: Elektrotechnik LI03
Urspr. COP	Einheit 03+04 OG
Datei: ETEC043	MA Grundfos Germany GmbH
Stand: 27.03.2026	Gewerk: Elektrotechnik
Bearb. 27.03.2026 ETEC	Maßstab: 1:50
Gepr. 27.03.2026	