


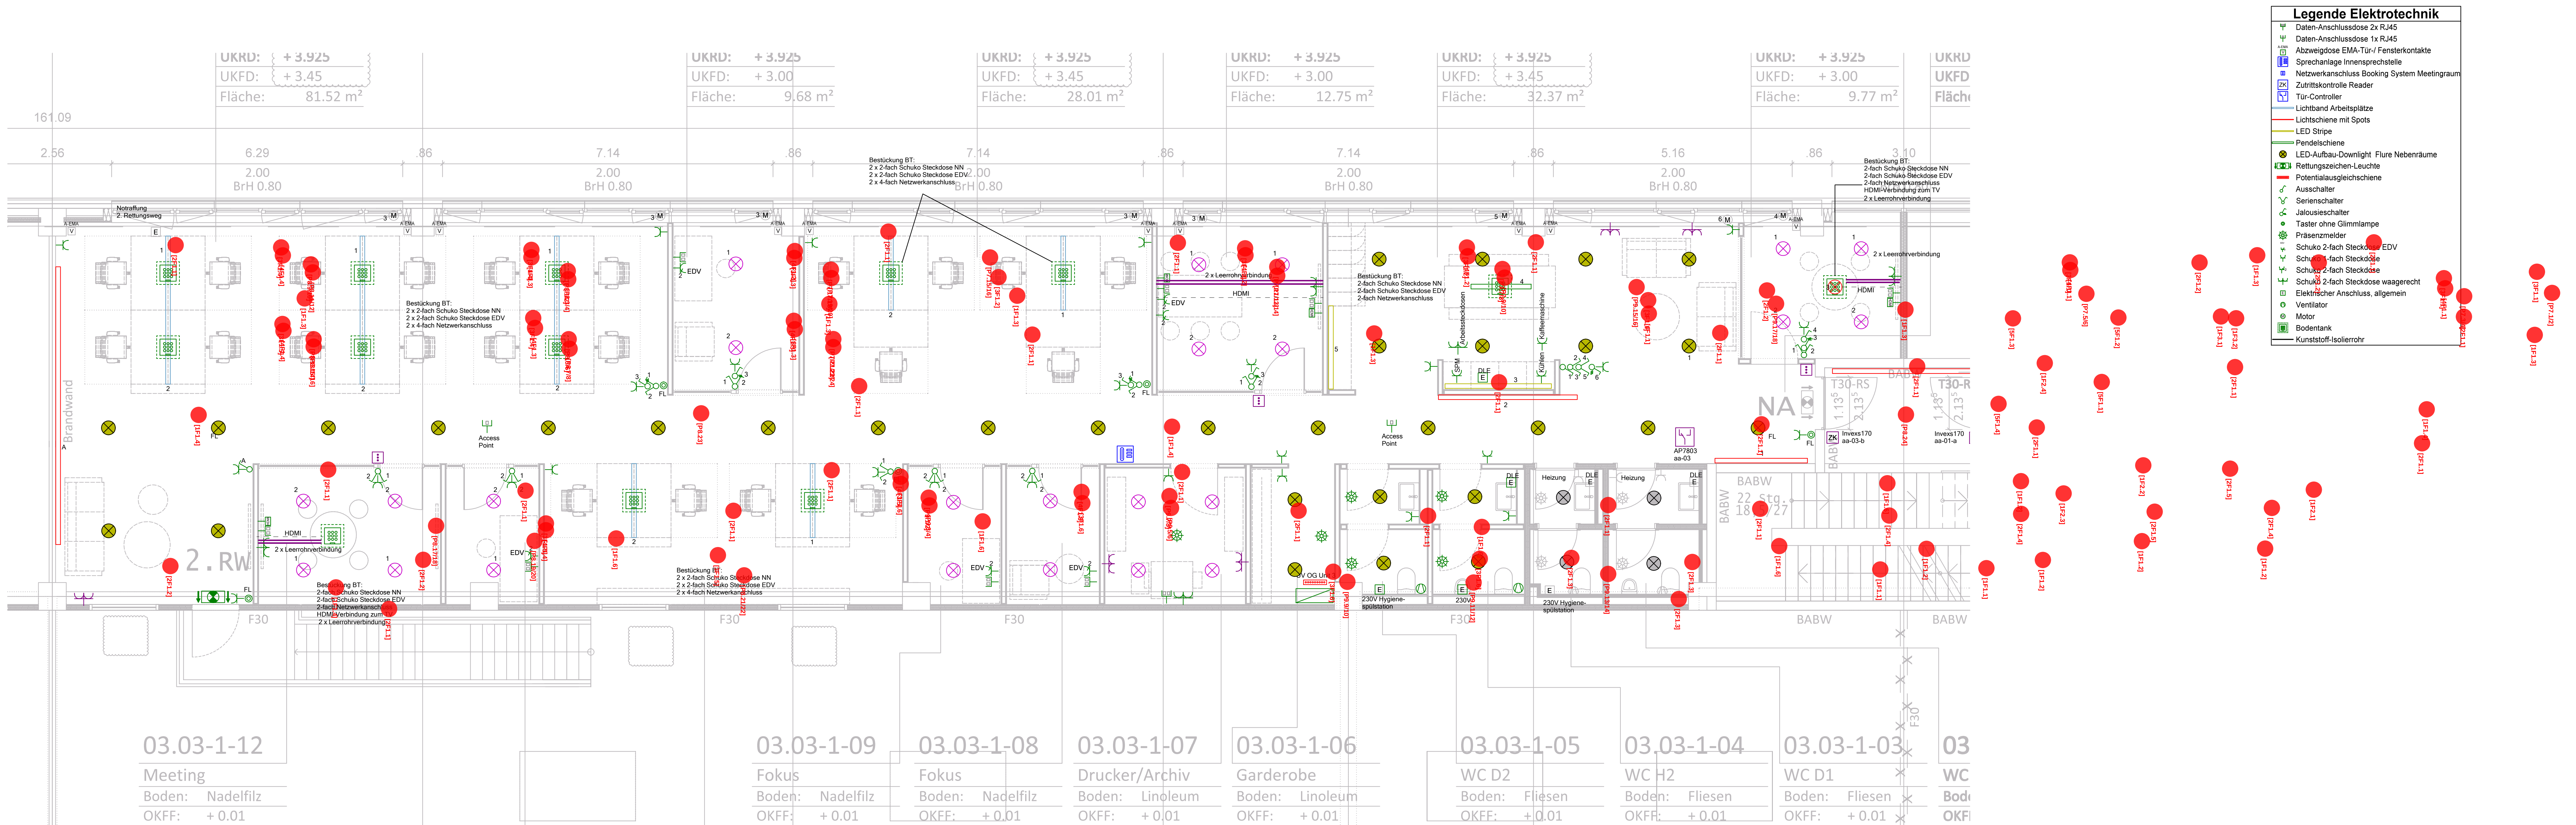

SDF_3_5_EP_MA_1_003_D_V

Auftraggeber	Bauherr
SEGRO 15. Grundbesitz GmbH	SEGRO Park Düsseldorf Flingern
Fichtenstrasse 33	Höhenweg 271a-287
40233 Düsseldorf	40233 Düsseldorf

EtecProjekt + Bau GmbH	Heinrich-Hertz-Straße 22a
	40699 Erkrath
	Tel.: 0211 - 210233 - 00
	Fax: 0211 - 210233 - 20
	Mail: info@etecprojekt.de

A	B	C	D	Index
Beleuchtung angepasst	Installation nach Vorgabe erweitert dunkelviolett dargestellt	Anpassung laut E-Mail Herr Duran	Grundriss Index F übernommen	Änderungen
02.04.2026	17.04.2026	19.05.2026	12.06.2026	geändert am
ETEC	ETEC	ETEC	ETEC	geändert von

Blatt: 1	Projekt: SEGRO Park Düsseldorf Flingern
Größe: A0	Zeichnung: Elektrotechnik LI03
Urspr: COP	Einheit 03+04 OG
Datei: ETEC043	MA Grundfos Germany GmbH
Stand: 27.03.2026	Gewerk: Elektrotechnik
Datum: 27.03.2026	Name: ETEC
Gepr: 27.03.2026	Maßstab: 1:50