



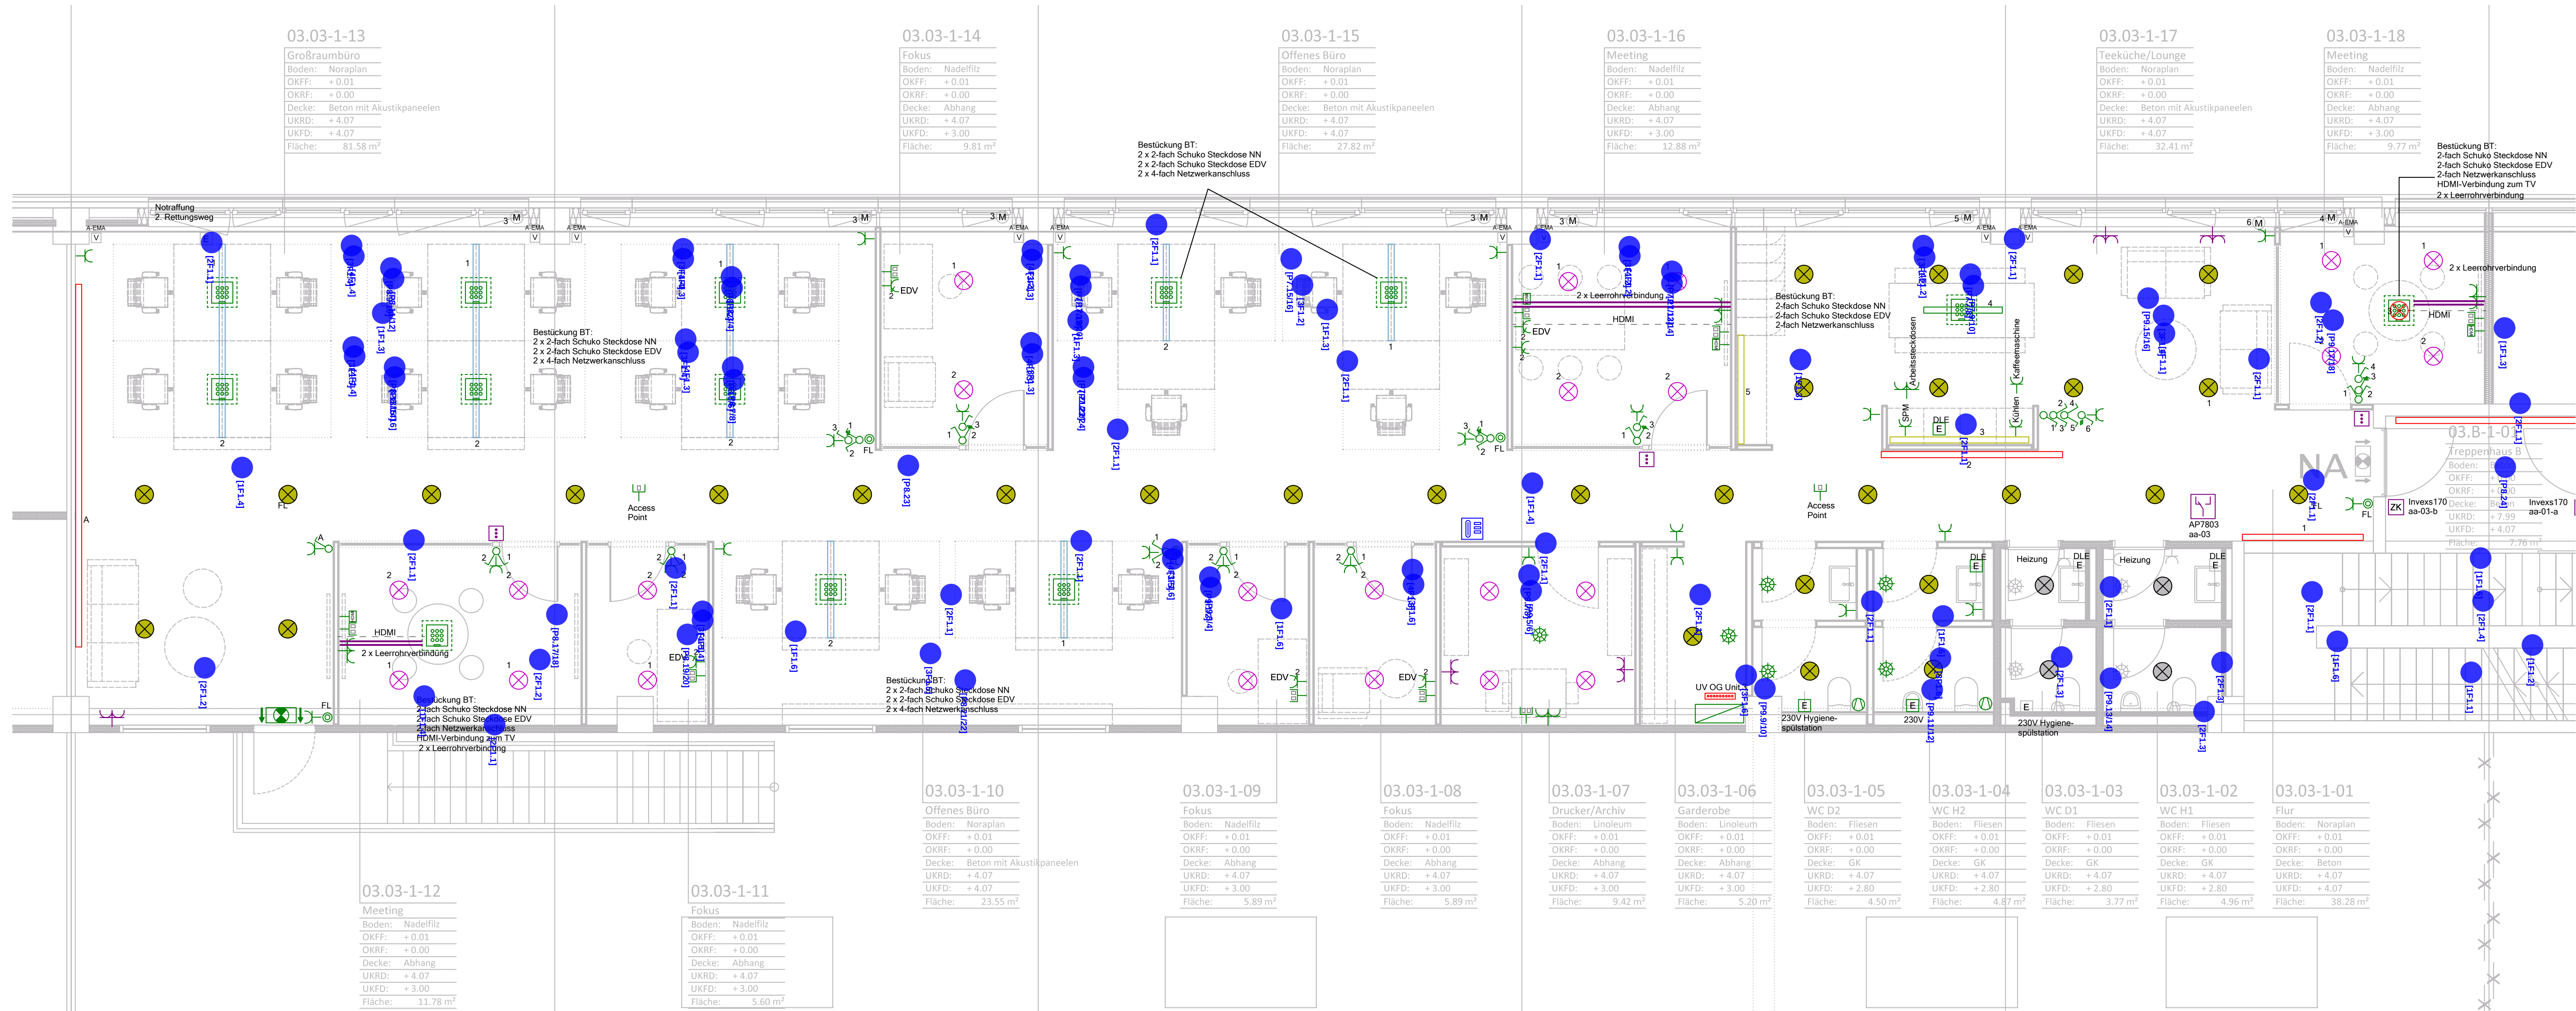

Legende Elektrotechnik	
	Daten-Anschlussdose 2x RJ45
	Daten-Anschlussdose 1x RJ45
	Abzweigdose EMA-Tür / Fensterkontakte
	Sprechanlage Innensprechstelle
	Netzwerkschloss Booking System Meetingraum
	Zutrittskontrolle Reader
	Tür-Controller
	Lichtband Arbeitsplätze
	Lichtschiene mit Spots
	LED Stripe
	Pendelschiene
	LED-Aufbau-Downlight Flure Nebenräume
	Rettungszeichen-Leuchte
	Potentialausgleichsschiene
	Ausschalter
	Serienschalter
	Jakusieschalter
	Taster ohne Klimmperle
	Präsenzmelder
	Schuko 2-fach Steckdose EDV
	Schuko 1-fach Steckdose
	Schuko 2-fach Steckdose waagrecht
	Elektrischer Anschluss, allgemein
	Ventilator
	Motor
	Bodentank
	Kunststoff-Isolierrohr

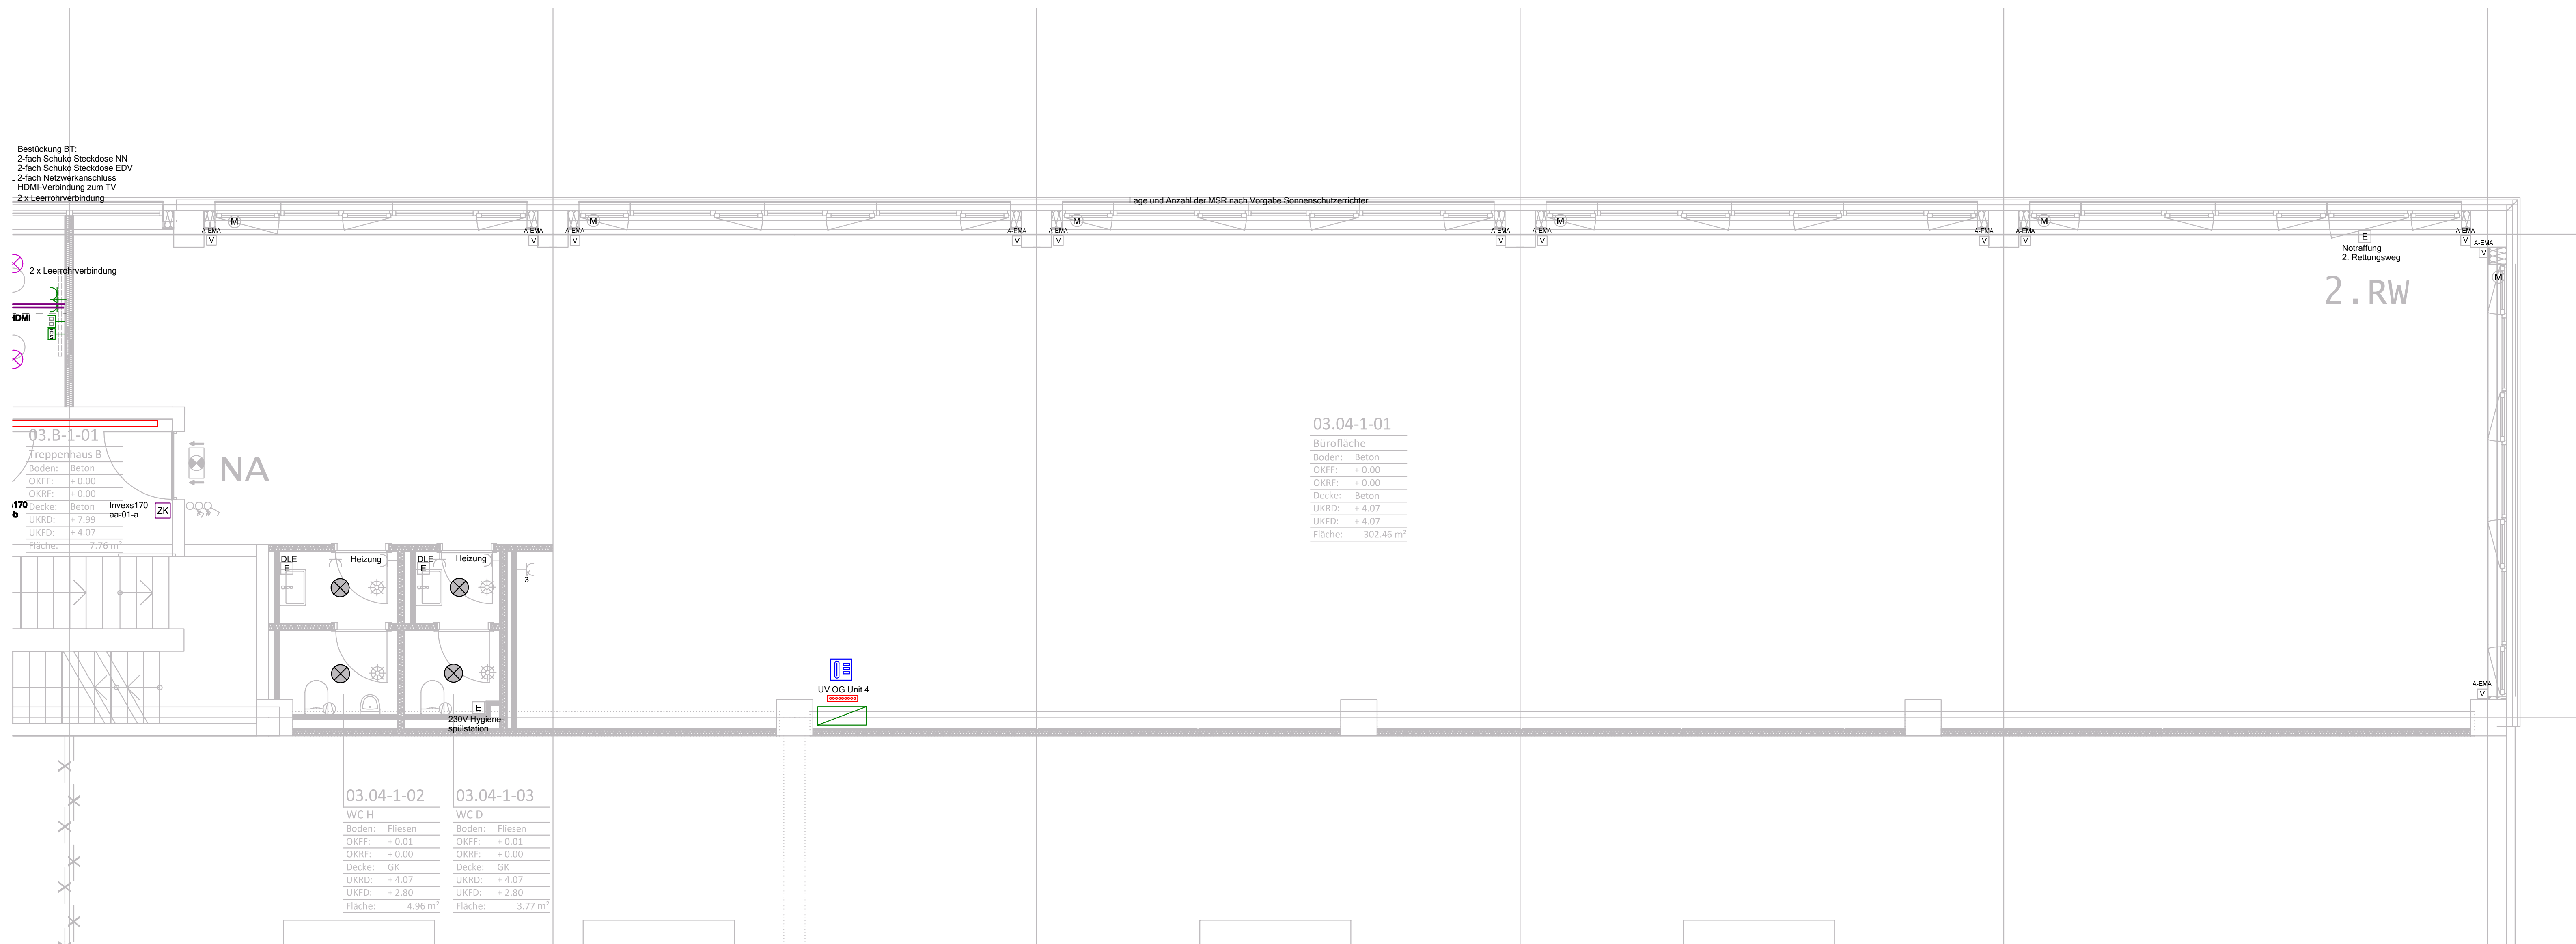

SDF_3_5_EP_MA_1_003_B_V

Auftraggeber	Bauvorhaben
SEGRO 15. Grundbesitz GmbH Fichtenstrasse 33 40233 Düsseldorf	SEGRO Park Düsseldorf Flingern Höherweg 271a-287 40233 Düsseldorf

	Heinrich-Hertz-Straße 22a 40699 Erkrath Tel.: 0211 - 210233 - 00 Fax: 0211 - 210233 - 20 Mail: info@etecprojekt.de
--	--

A	B	Index	Änderungen	geändert am	geändert von
Beleuchtung angepasst	02.04.2026	ETEC			
Installation nach Vorgabe erweitert dunkelviolett dargestellt	17.04.2026	ETEC			

Blatt: 1		Projekt: SEGRO Park Düsseldorf Flingern	
Größe: A0			
Urspr. COP		Zeichnung: Elektrotechnik LJ03	
Datei: ETEC0403		Einheit 03+04 OG	
Stand 27.03.2026		MA Grundfos Germany GmbH	
Datum	Name	Gewerk: Elektrotechnik	Maßstab: 1:50
Bezir. 27.03.2026	ETEC		
Gespr. 27.03.2026			